

КОМПАС-3D v24 Учебная версия © 2025 ООО "АСКОН-Системы проектирования", Россия Все права защищены.

Перв. примен.


Справ. №

Подп. и дата

Взам. инв. №

Инв. № подл.

Не для коммерческого использования

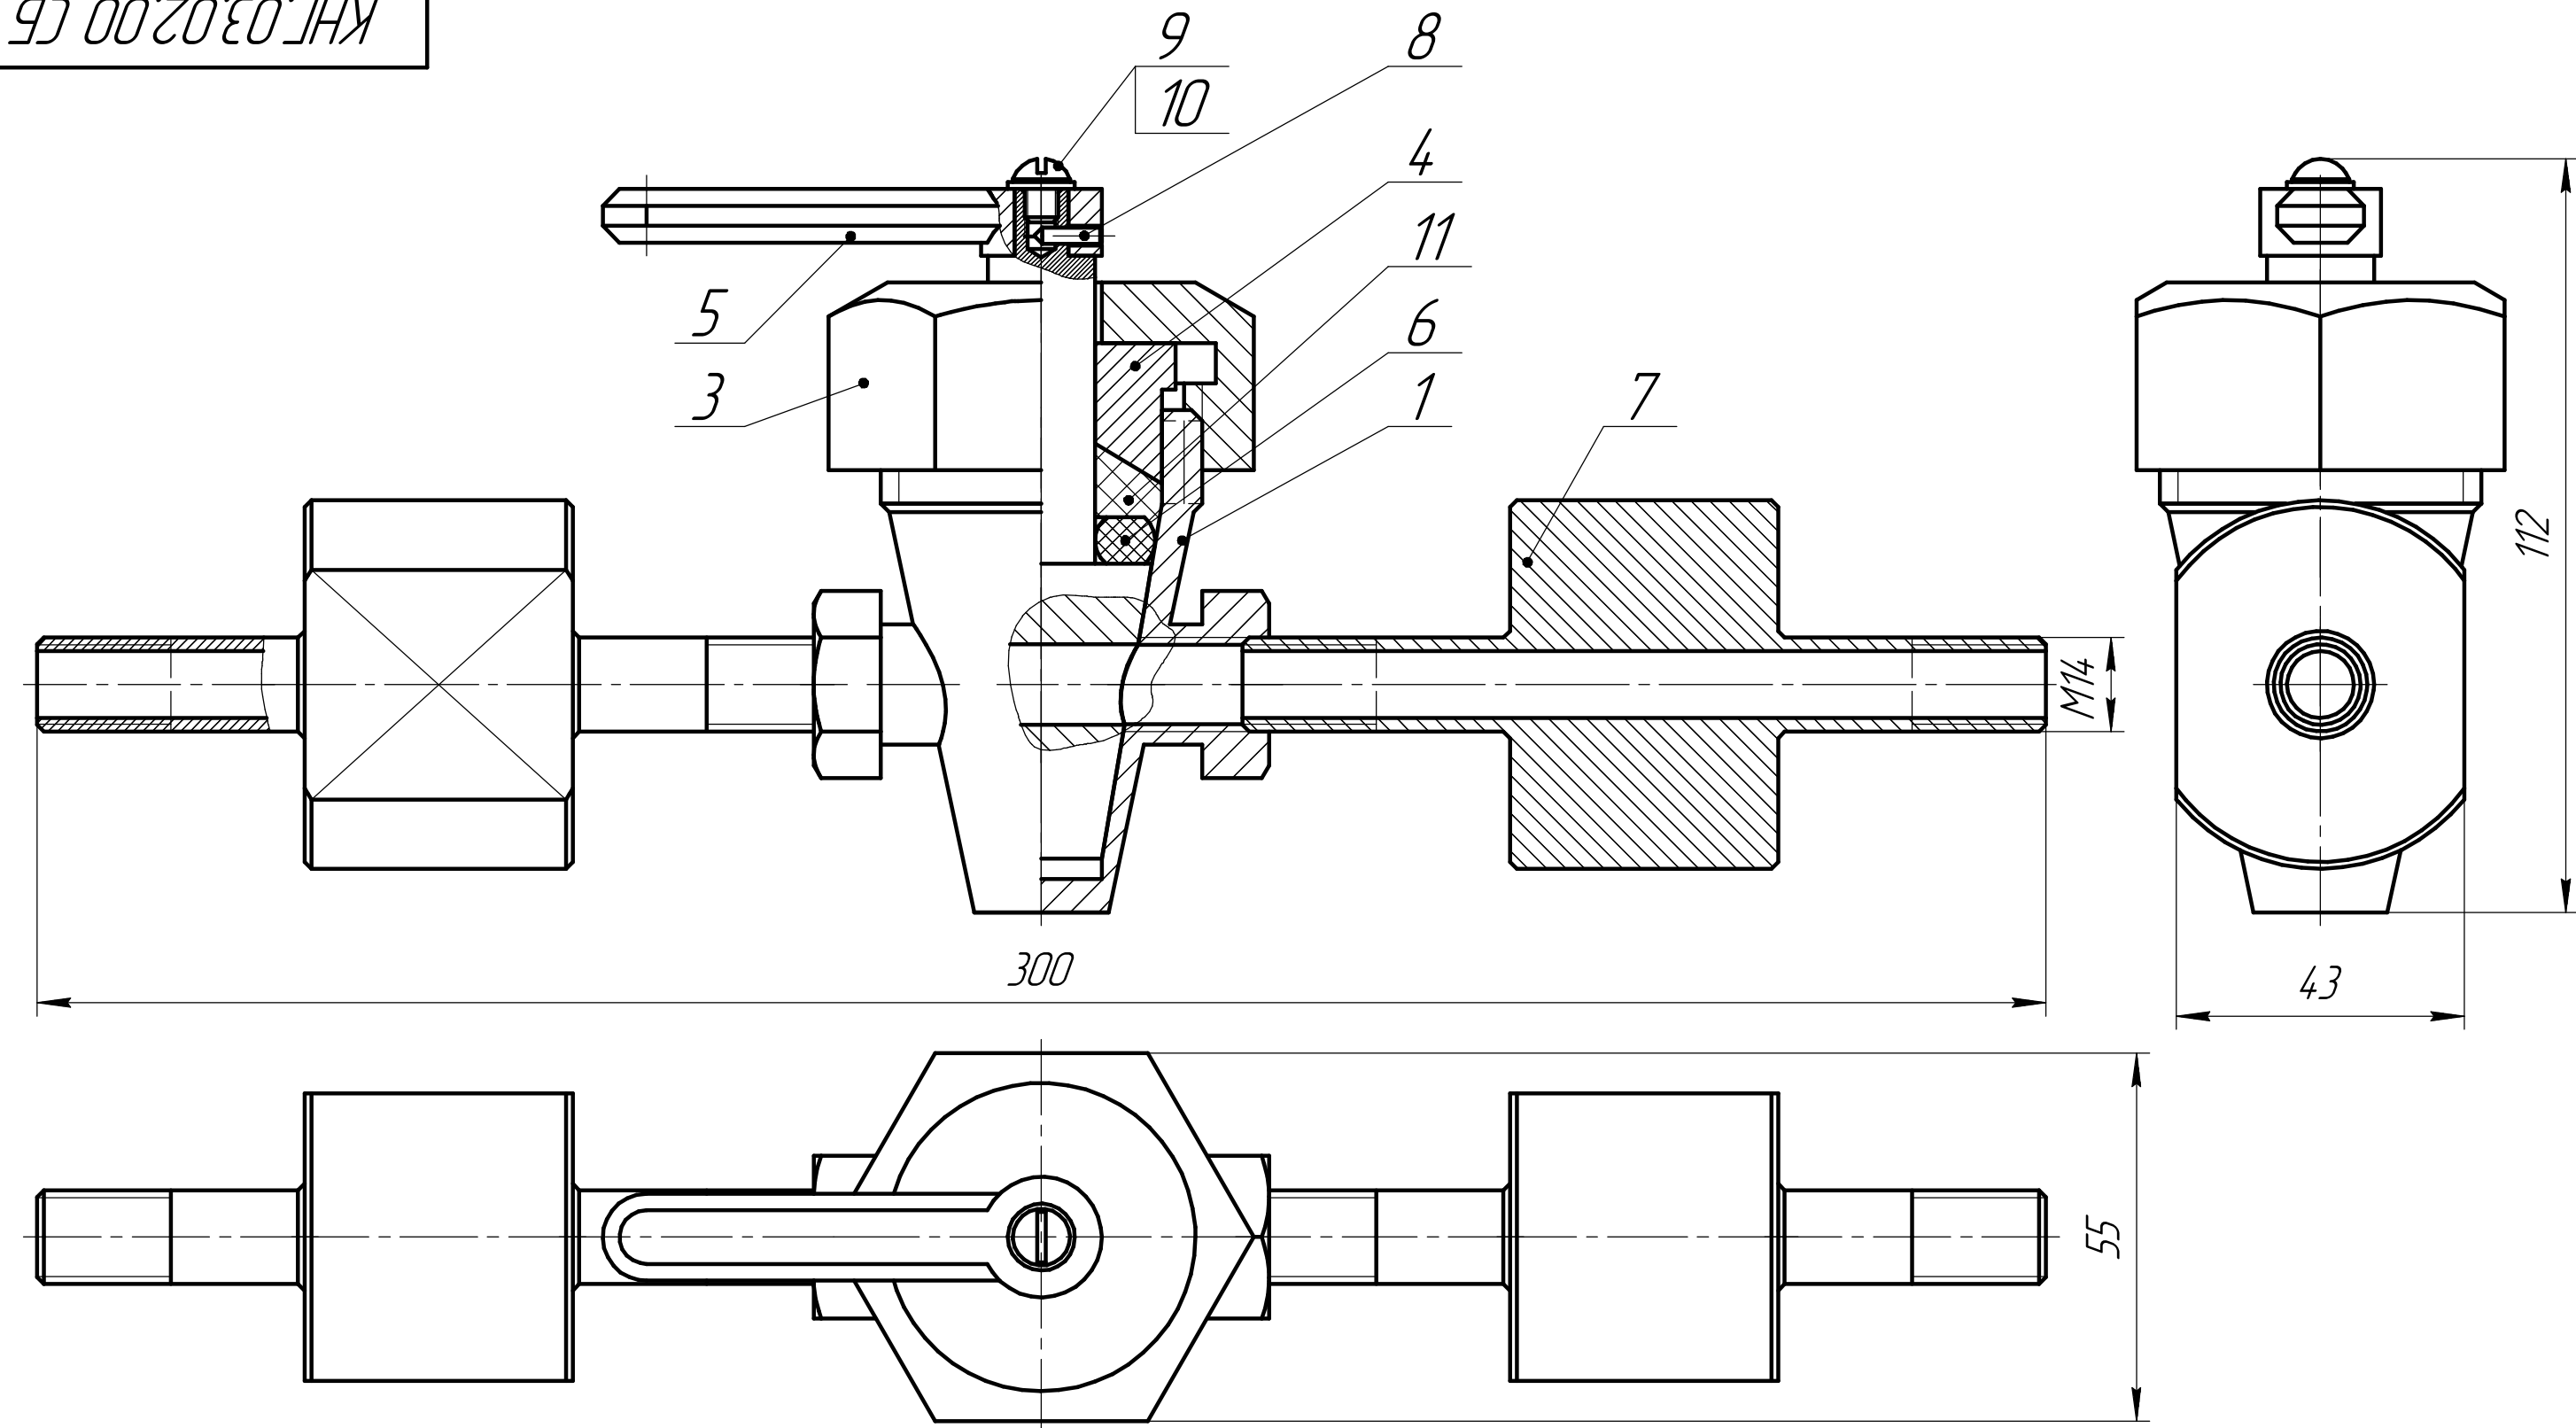

					КНГ.03.02.00 СБ			
Изм.	Лист	№ докум.	Подп.	Дата	Узел пробковый с водопроводной арматурой Сборочный чертёж	Лит.	Масса	Масштаб
Разраб.	Батулин						2,43	1:1
Пров.	Третьяков							
Т.контр.						Лист	Листов	1
Н.контр.					ПГУПС			
Утв.					АТ-531-з			

Копировал

Формат А3