

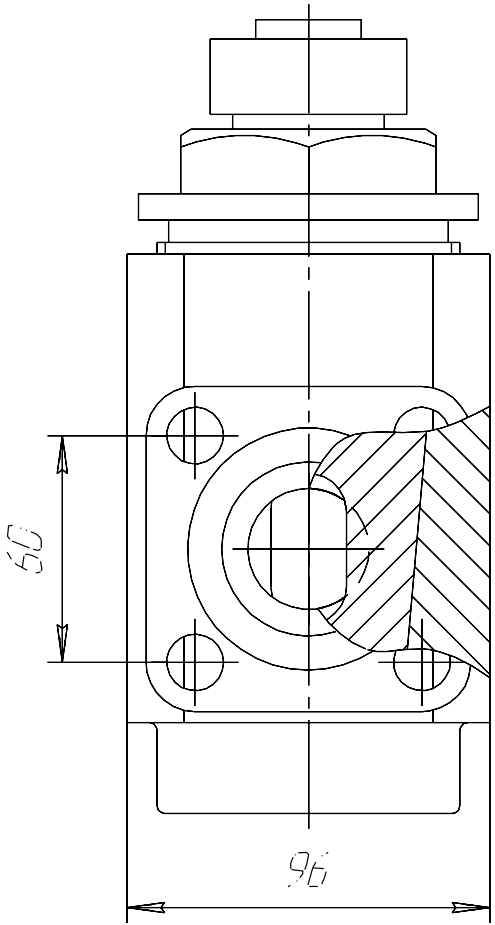
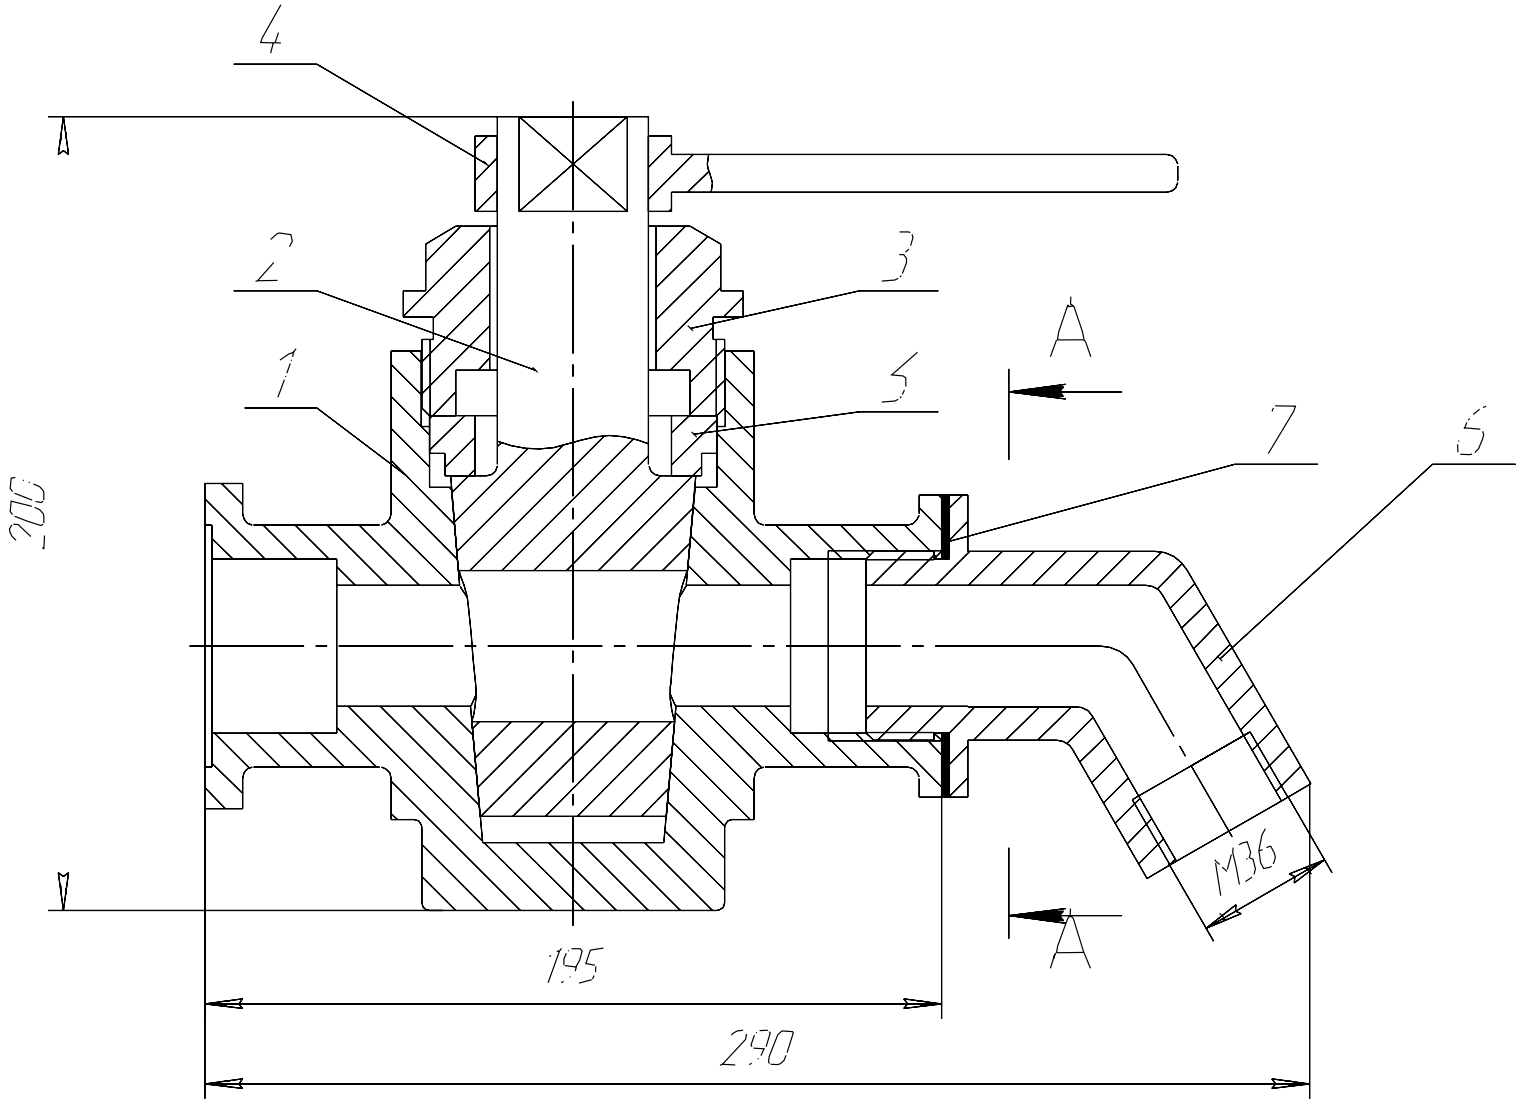


M400 03 00 00 C6

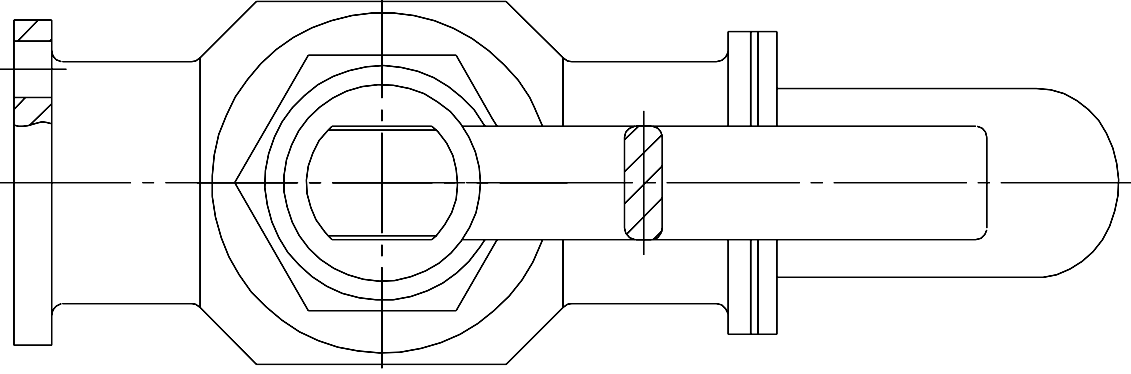

A-A

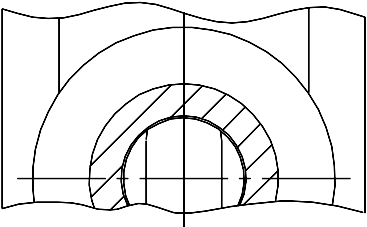

					M400 03 00 00 C6			
Изм Разраб Проез Т контр Н контр Узв	Лист	№ докум	Лод	Дата	Кран сливной Сборочный чертеж	Лит	Масса	Масштаб
		Дорохов					12,85	1:1
		Лузанова						
						Лист	Листов	1
						Лулс ЛТ-519-3		