

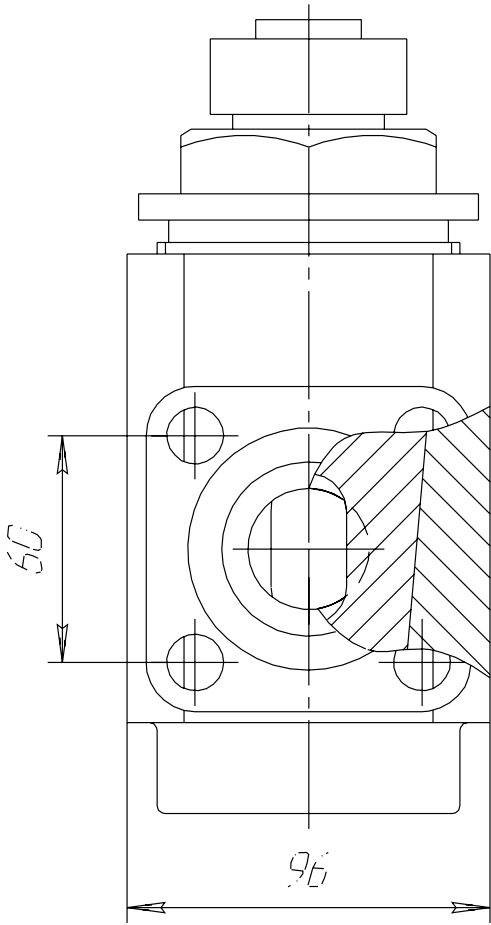
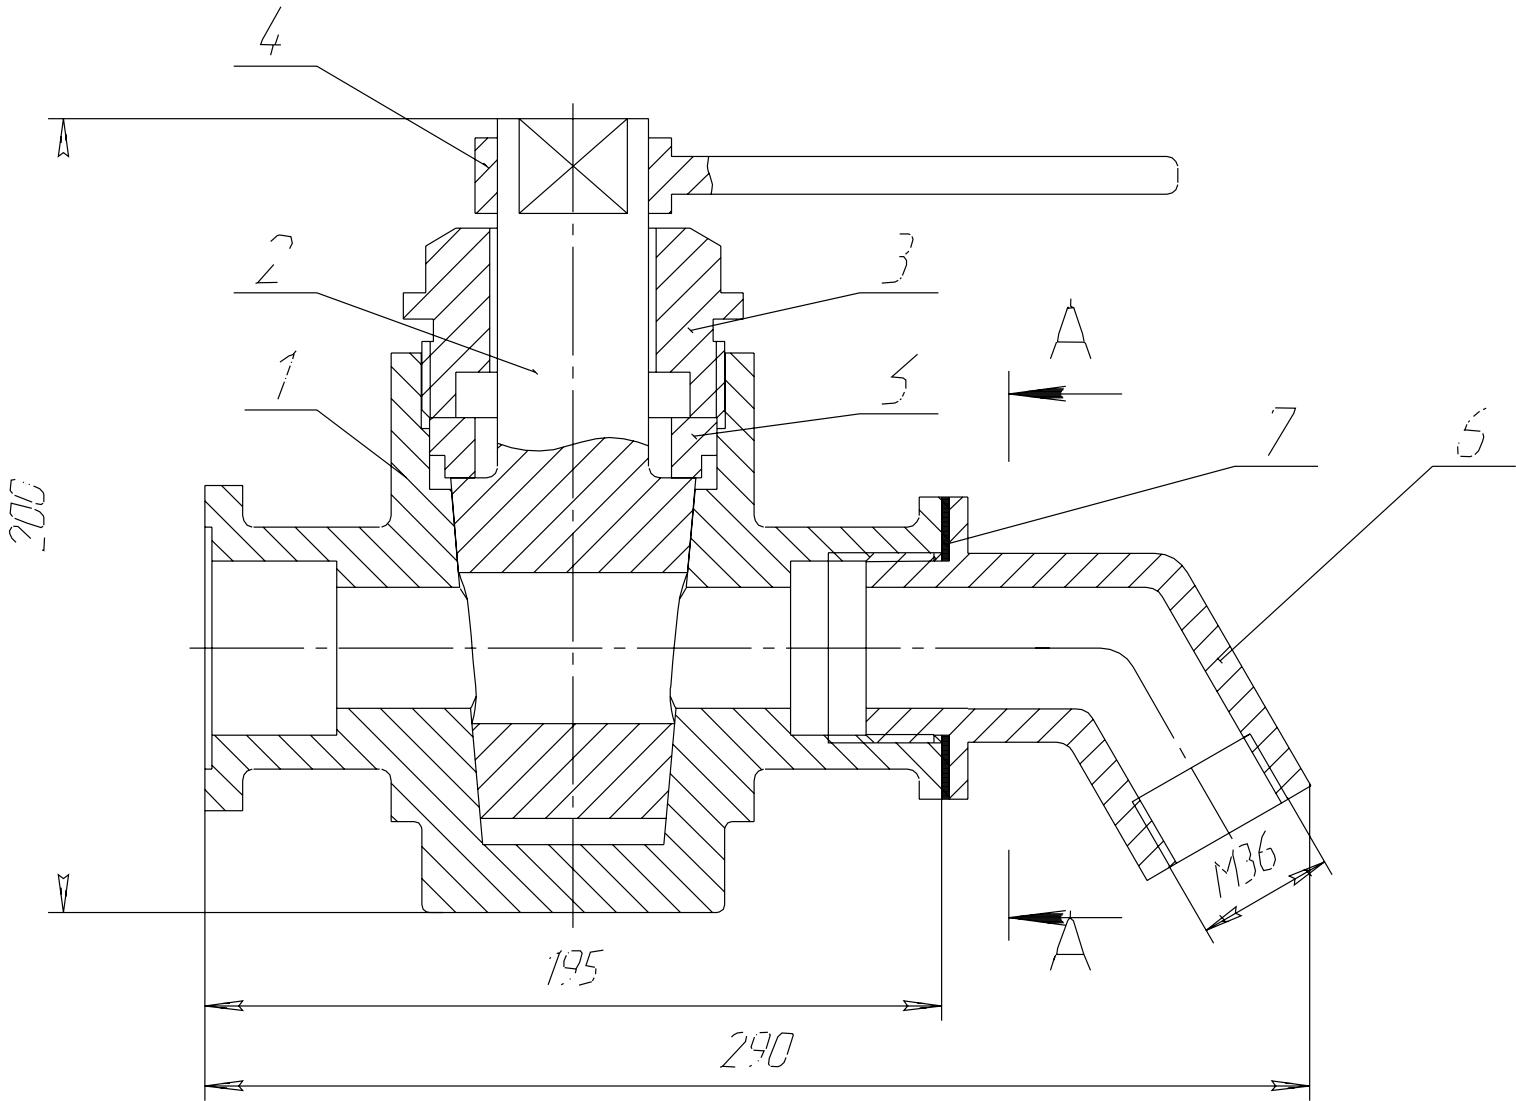


M400 03 00 00 C6

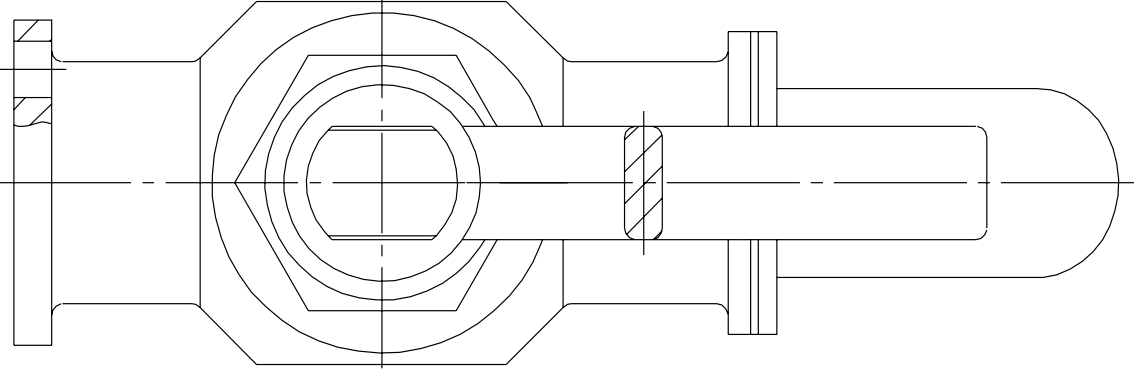

A-A

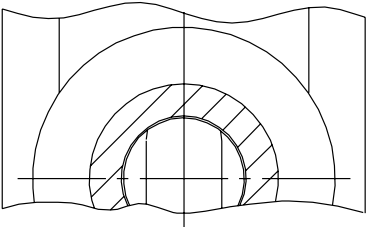

					M400 03 00 00 C6							
Изм	Лист	№ докум	Лод	Дата	Кран сливной Сборочный чертеж			Лит		Масса	Масштаб	
Разраб		Дорохов									12,85	1:1
Проез		Лузанова										
Т контр								Лист		Листов 1		
								Лулс				
Н контр								ЛТ-519-3				
Утв												