

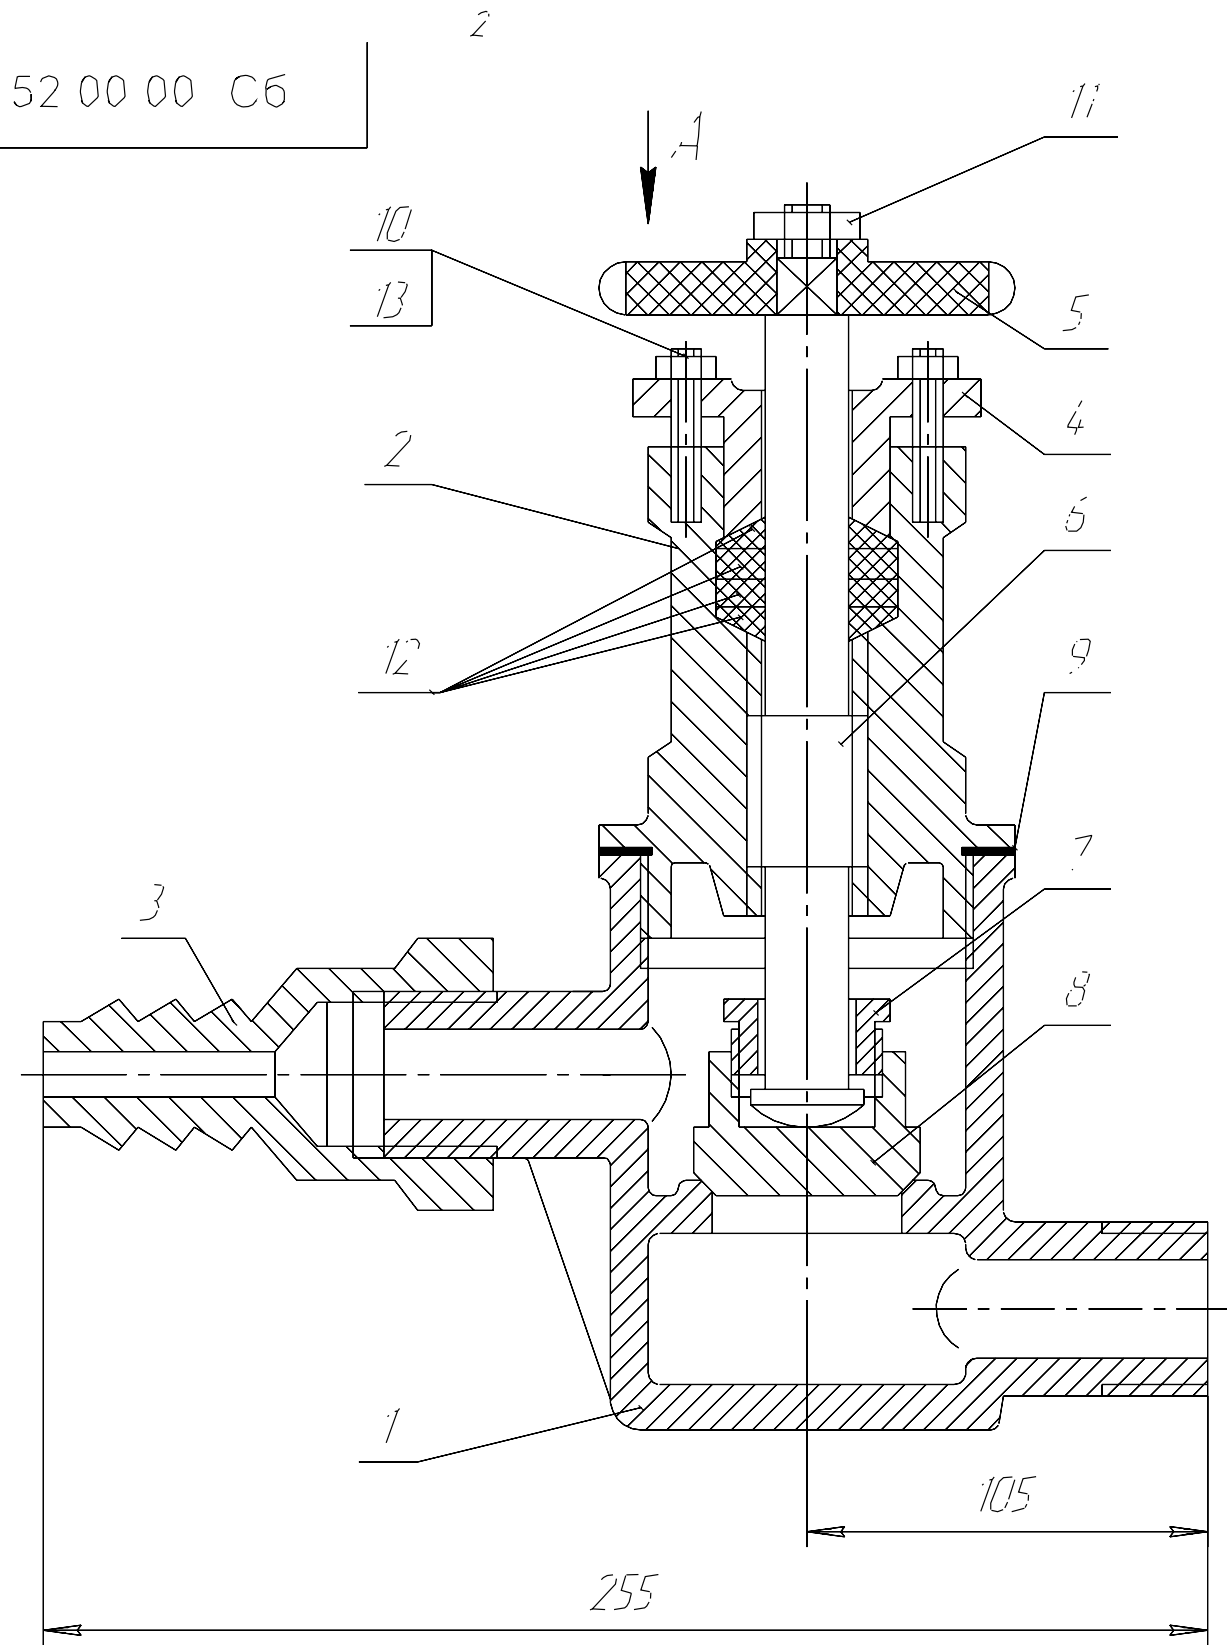
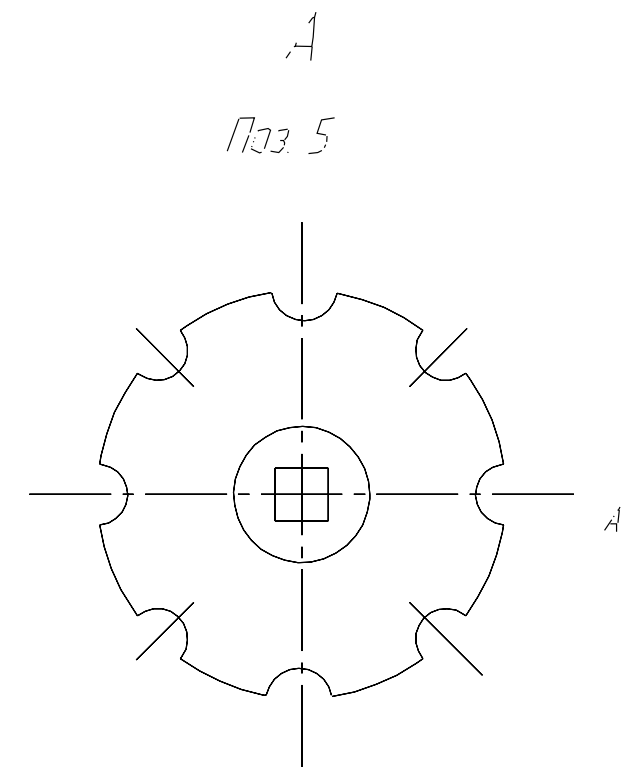


M400 52 00 00 C6

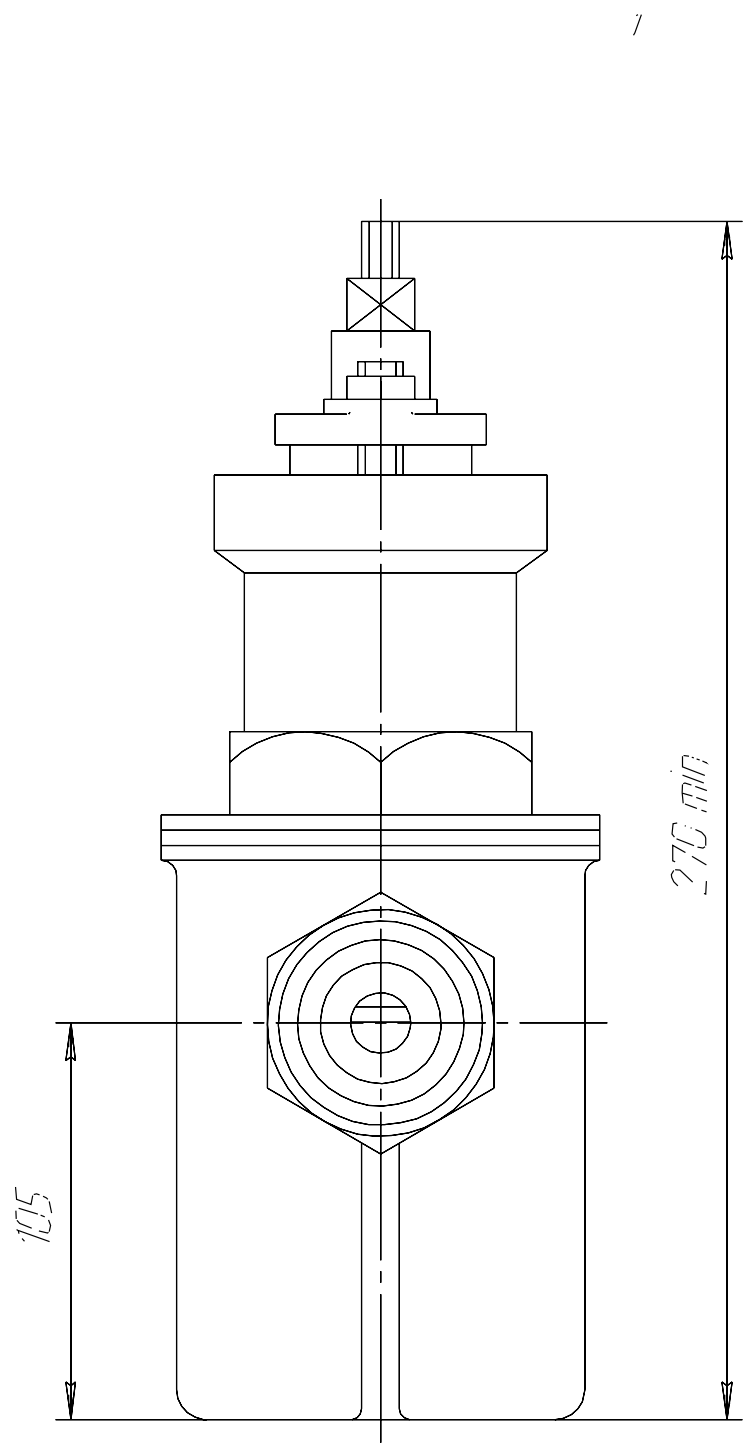

Детали поз 5, 11 усл. не показаны

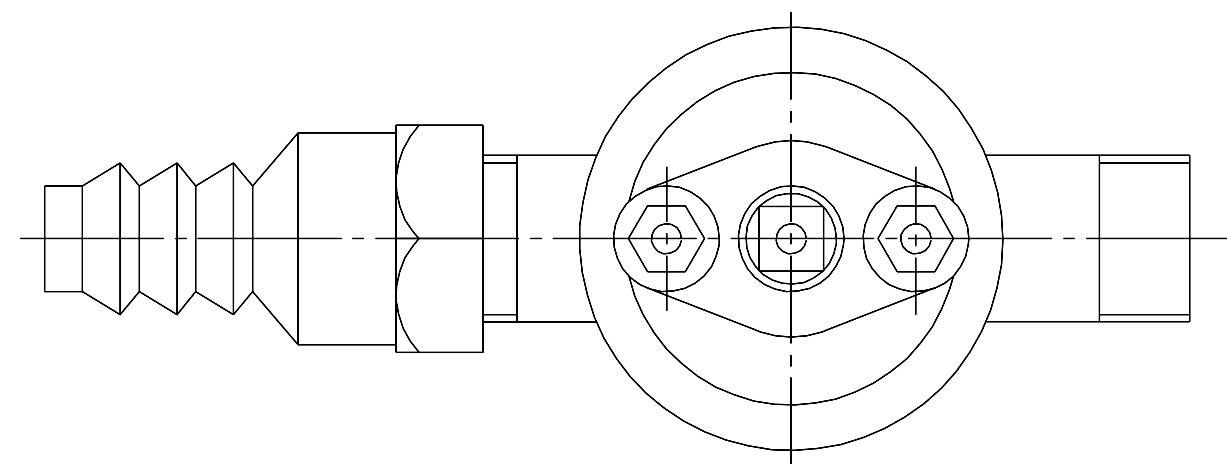

					M400 52 00 00 C6			
					Клиан Сборочный чертеж	Лит	Масса	Масштаб
Изм	Лист	№ докум	Лод	Дата				1:2
Разраб		Сухорев Д О						
Проез		Лузанова						
Т контр						Лист	Листов	1
Н контр						ЛТ-519-3		
Утв								