

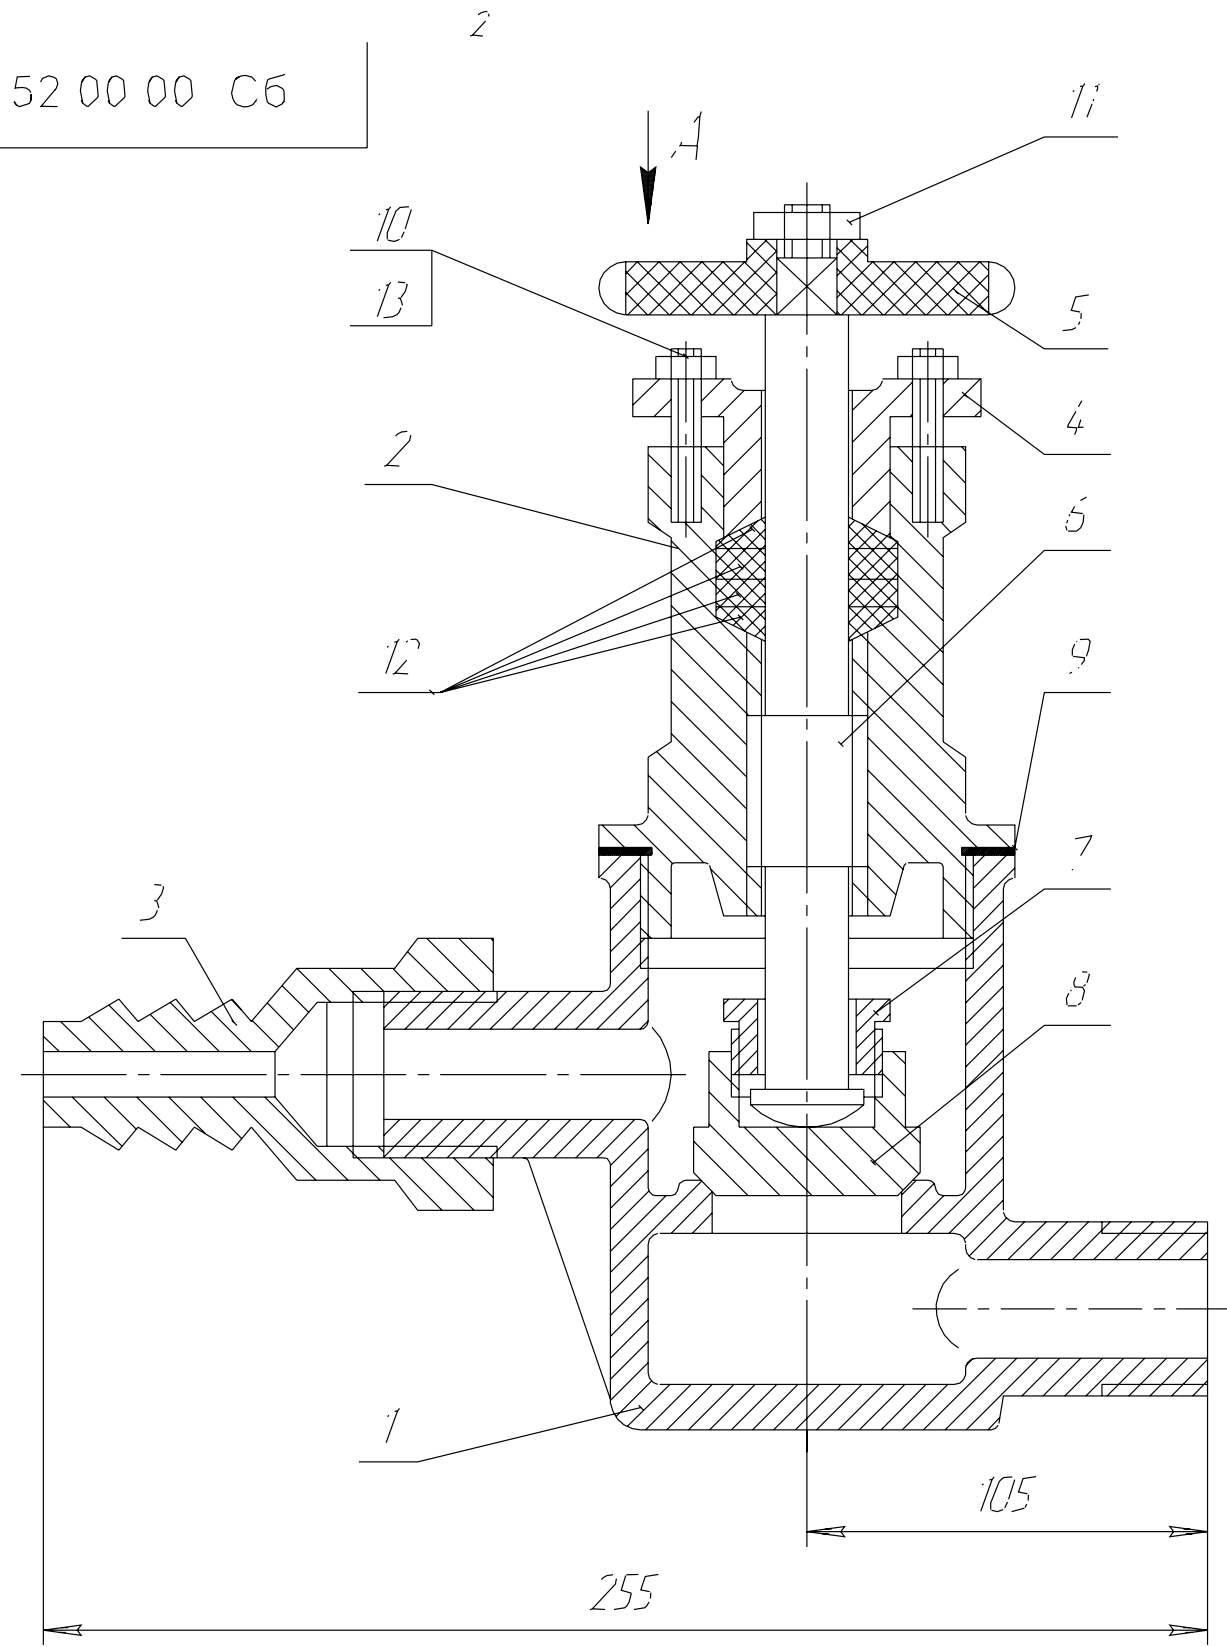
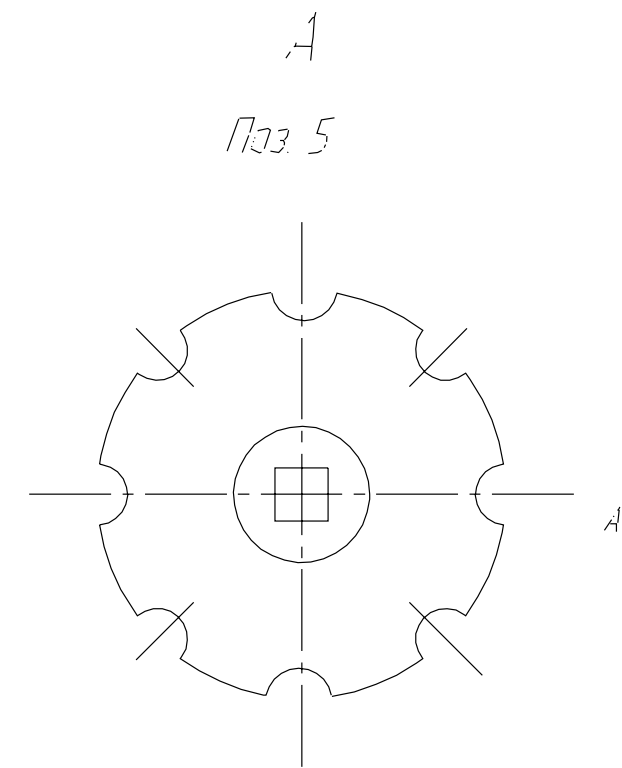


M400 52 00 00 C6

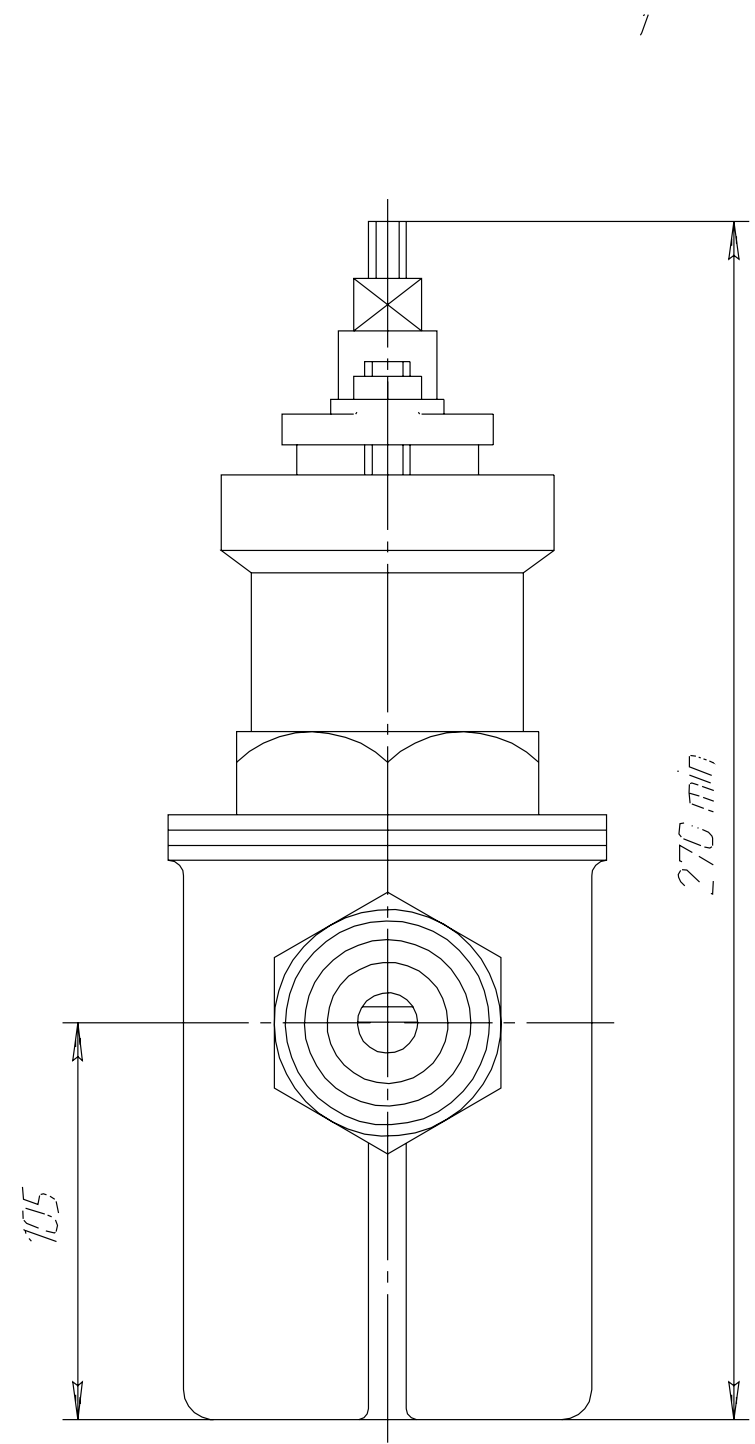

Детали поз 5, 11 усл. не показаны

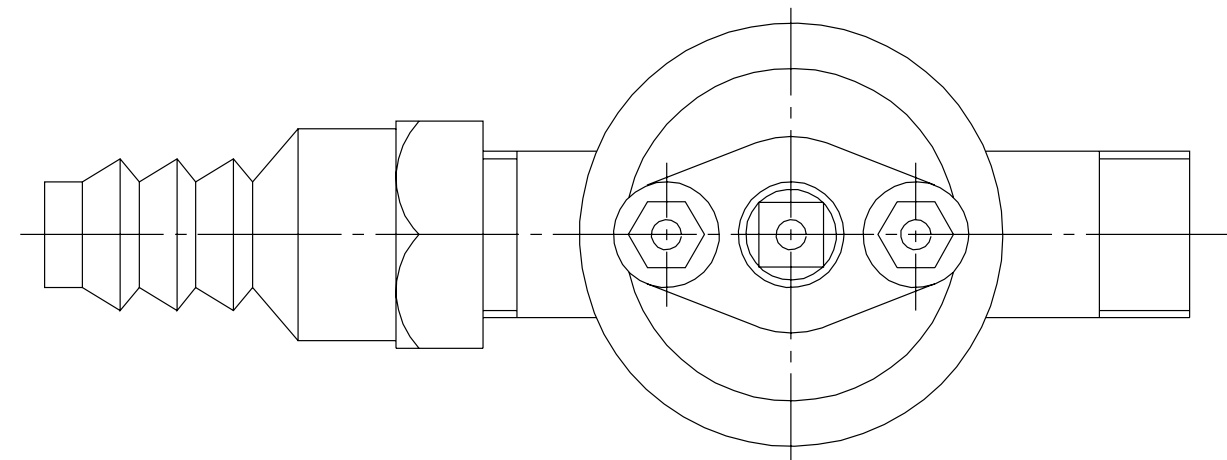

					M400 52 00 00 C6				
					Клиан Сборочный чертеж	Лит	Масса	Масштаб	
Изм	Лист	№ докум	Лод	Дата				1:2	
Разраб		Сухорос Д О							
Арх		Лузанова							
Т контр						Лист	Листов	1	
					ЛТ-519-3				
Н контр									
Утв									