
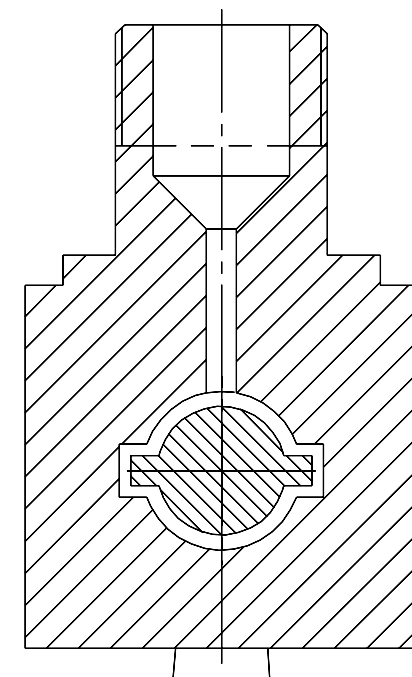
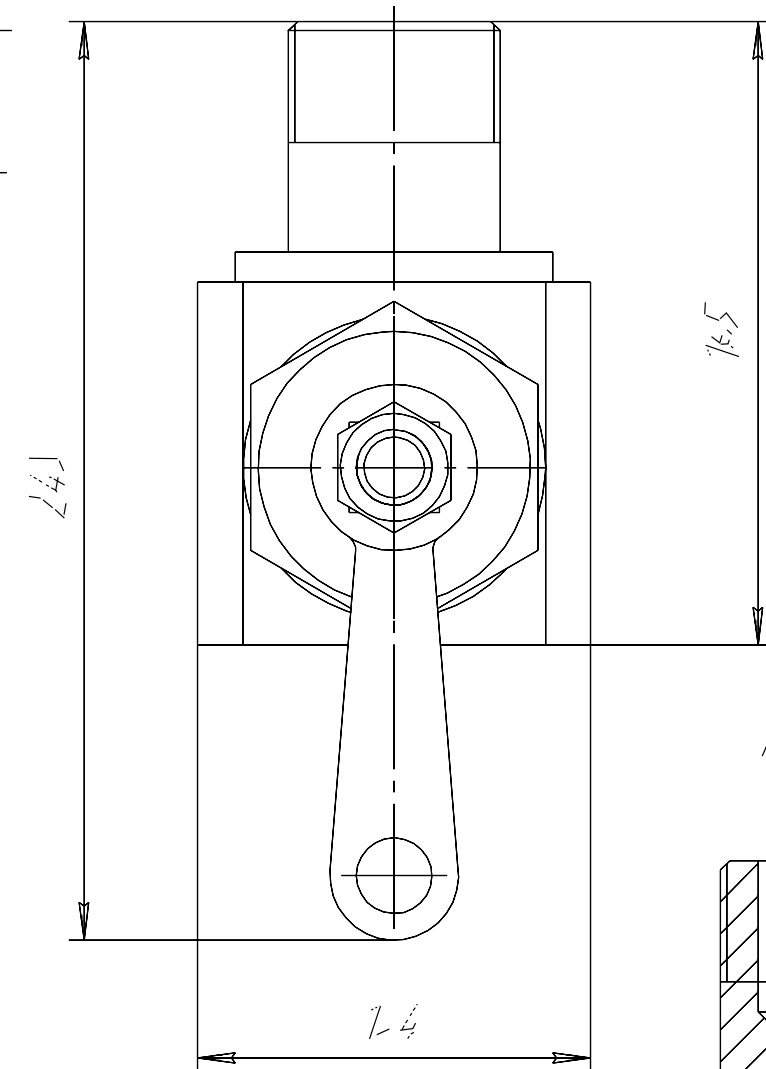


М400 60 00 00 С6

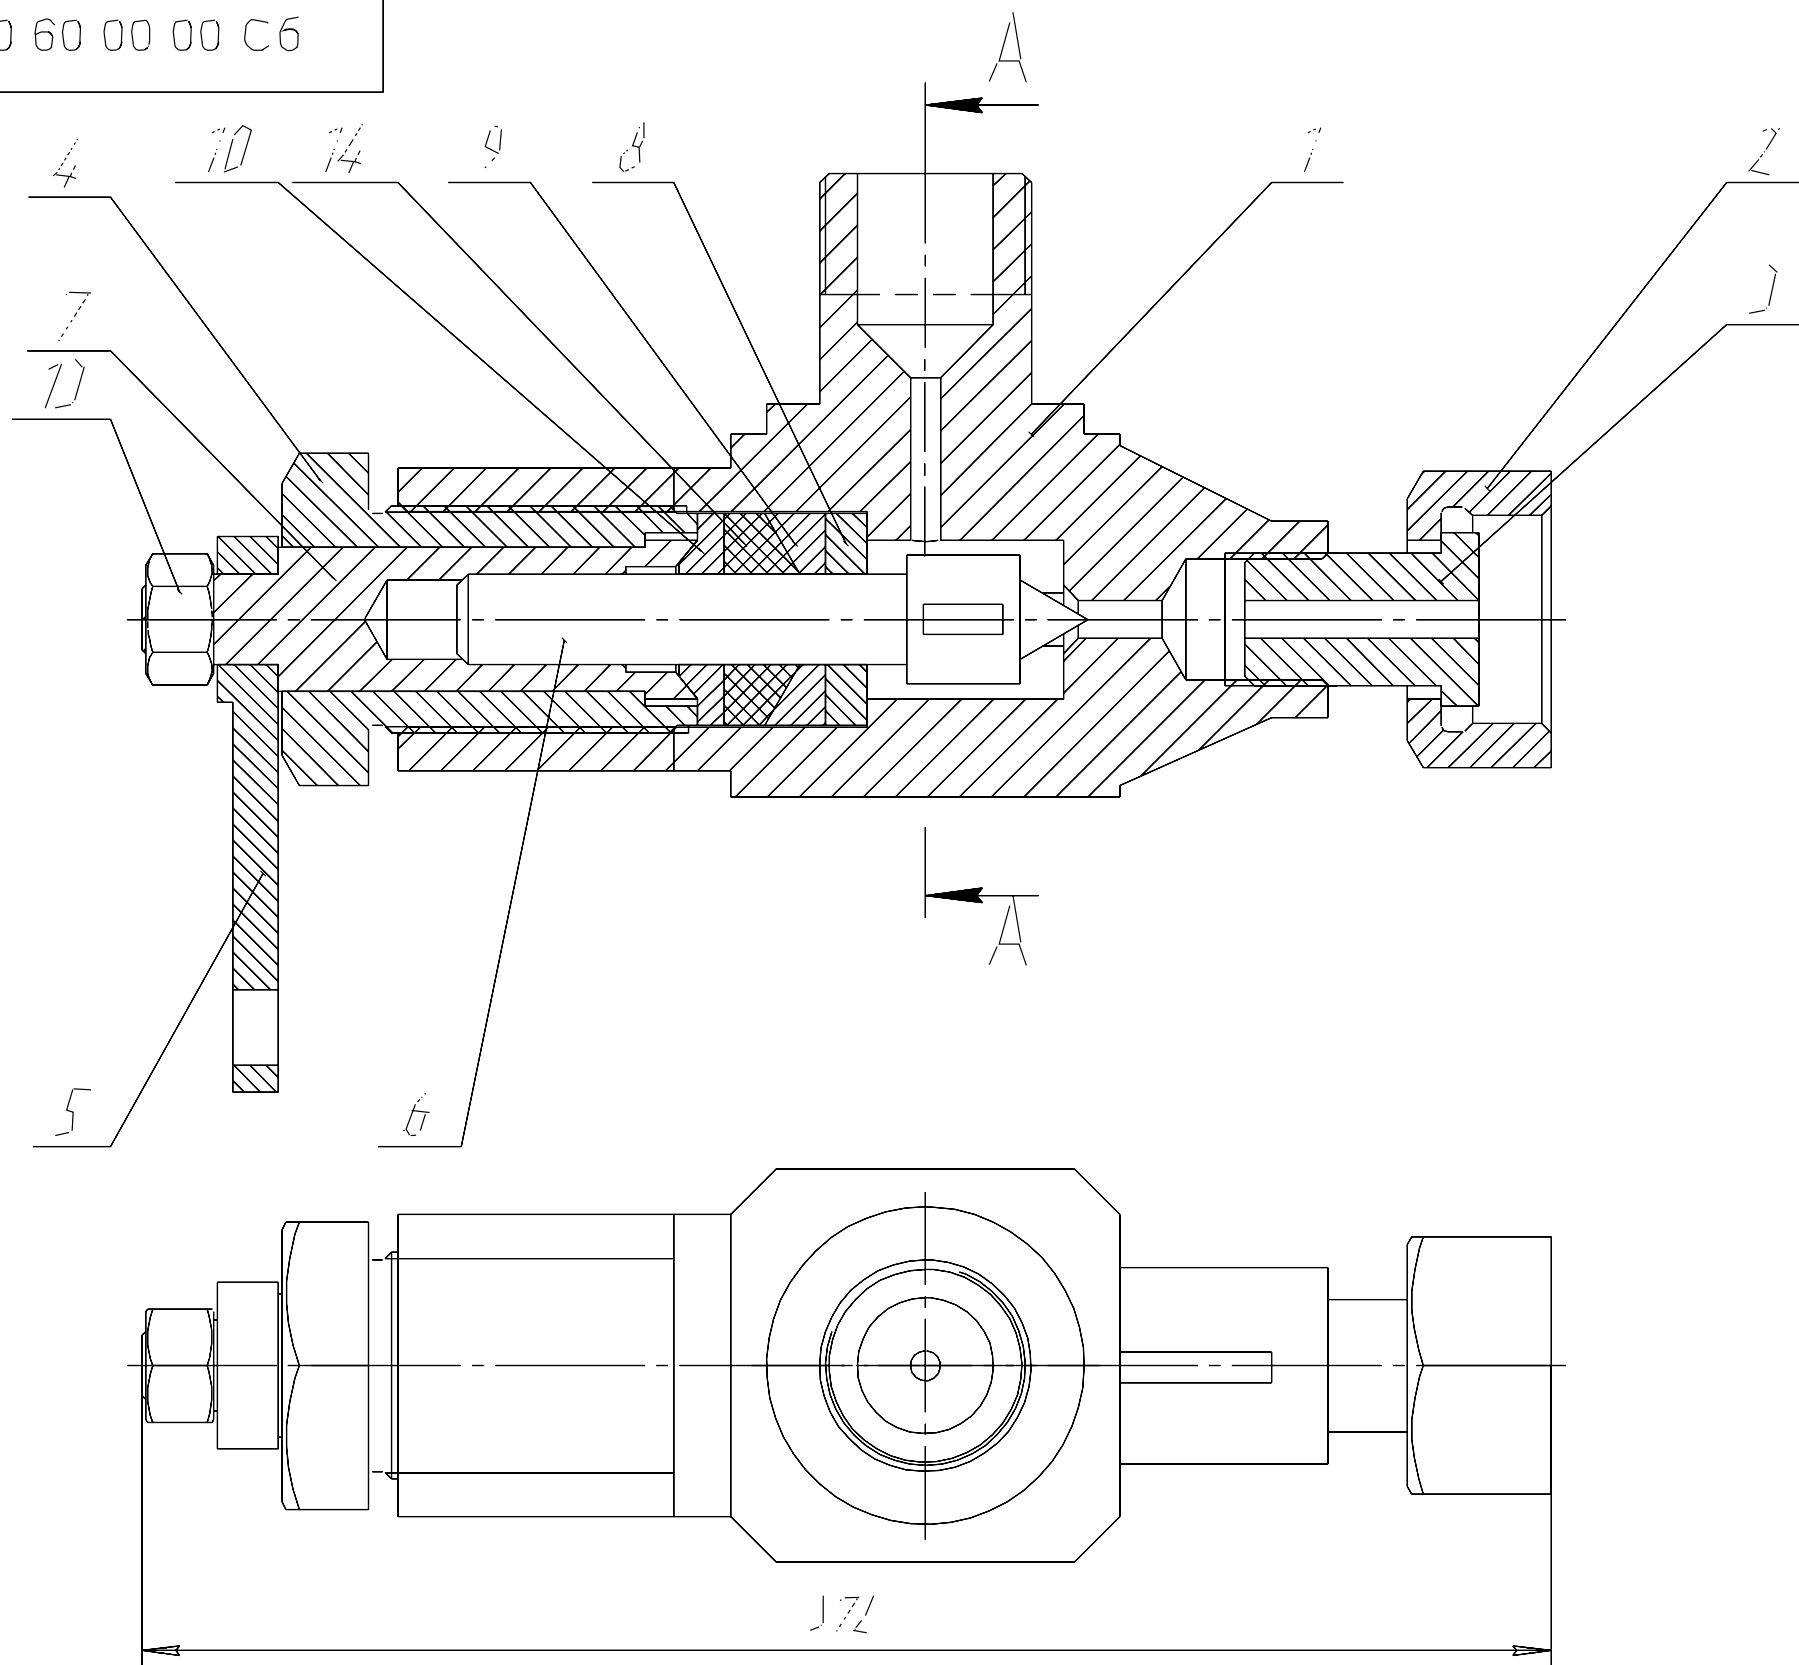

					М400 60 00 00 С6			
Изм	Лист	№ докум	Лодд	Дата	Вентиль Сборочный чертеж	Лист	Масса	Мгсштгб
Разрб		Федорова К.А.						1/
Проз		Лузанова						
Т контр						Лист	Листов	1
Н контр						Т-519-3		
Удк								