
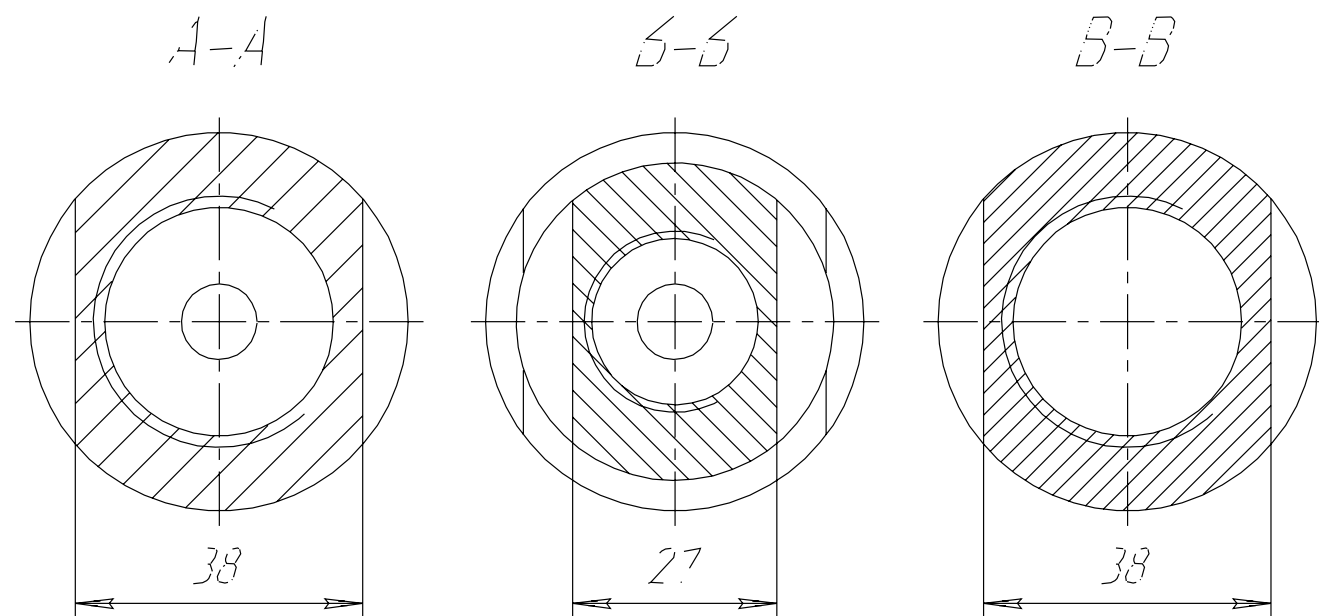


КНДЗДЗООСБ

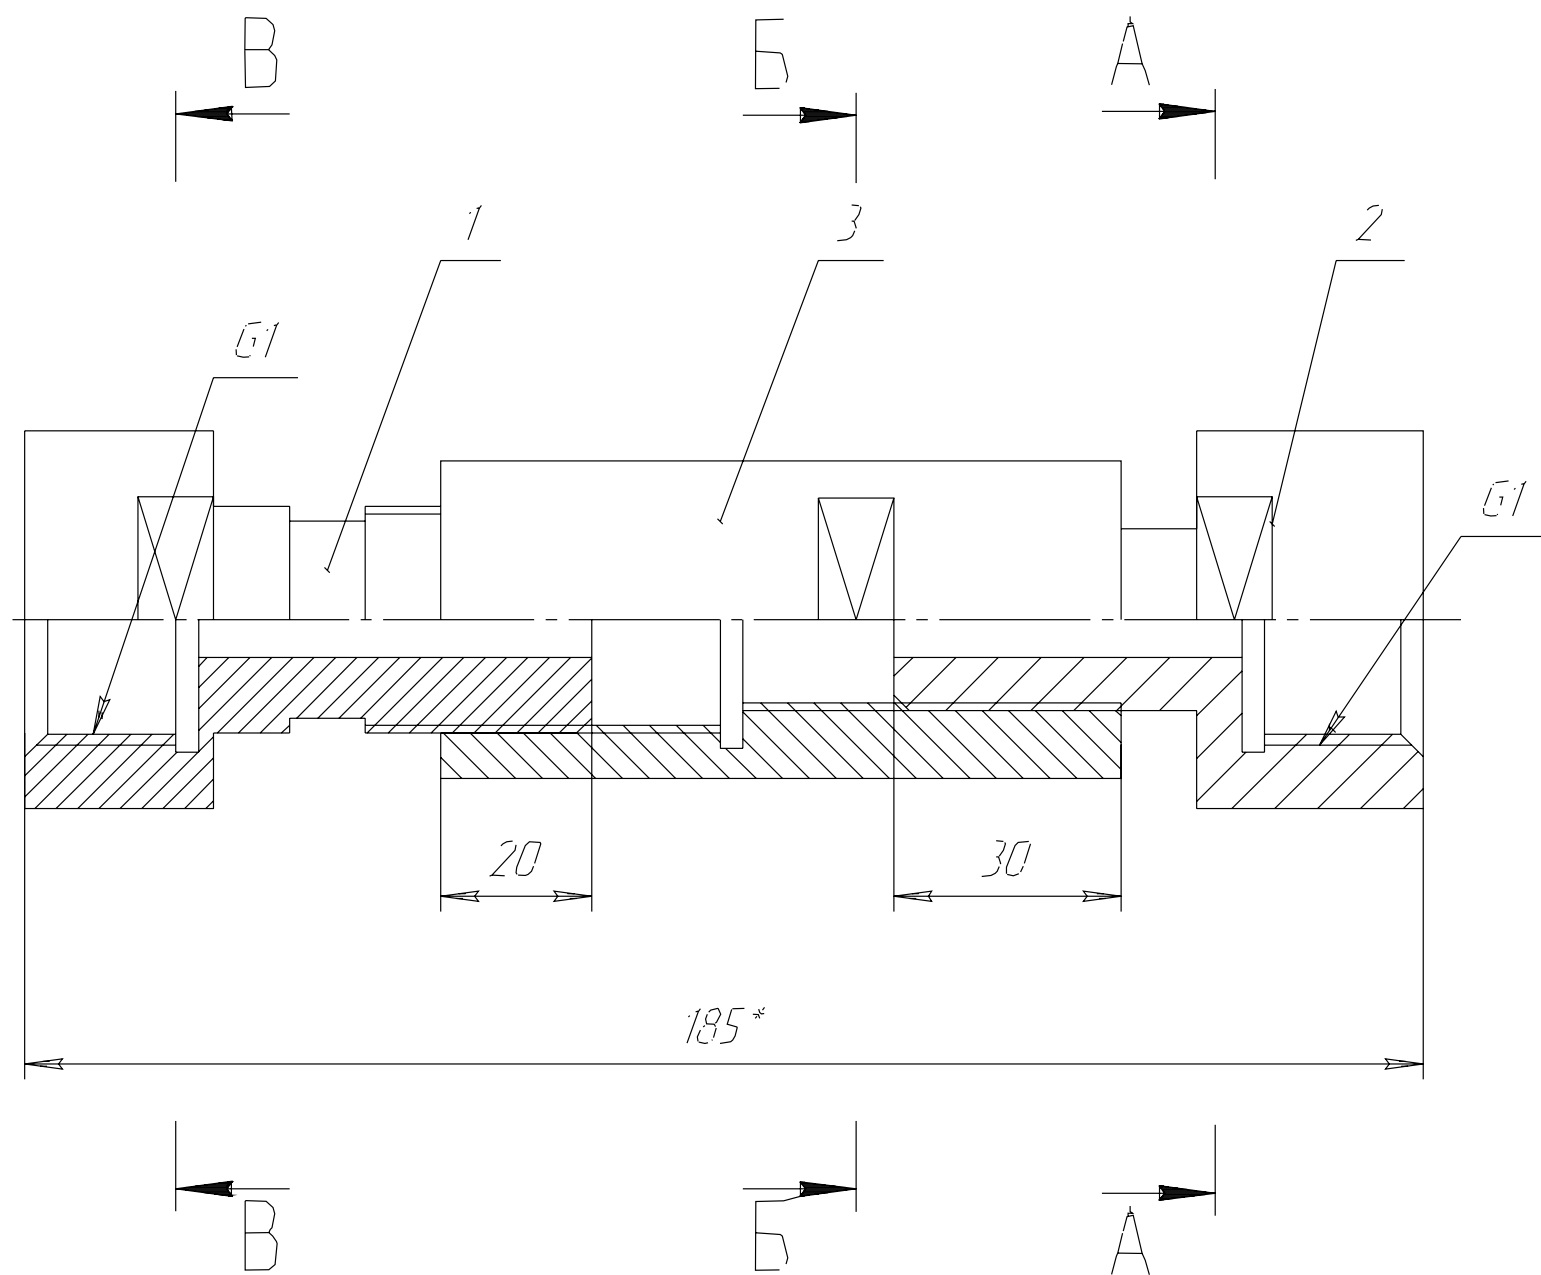

*Размер для справок

					КНДЗДЗООСБ			
					Узе Сборочный чертеж	Лист	Масштаб	Масштаб
Исполн	№ докум	Дата						1:1
Разраб	Деталь							
Проб	Издание					Лист	Листов	1
Техник						ПГУП		
Ректор						У-519-8		
Умд								