
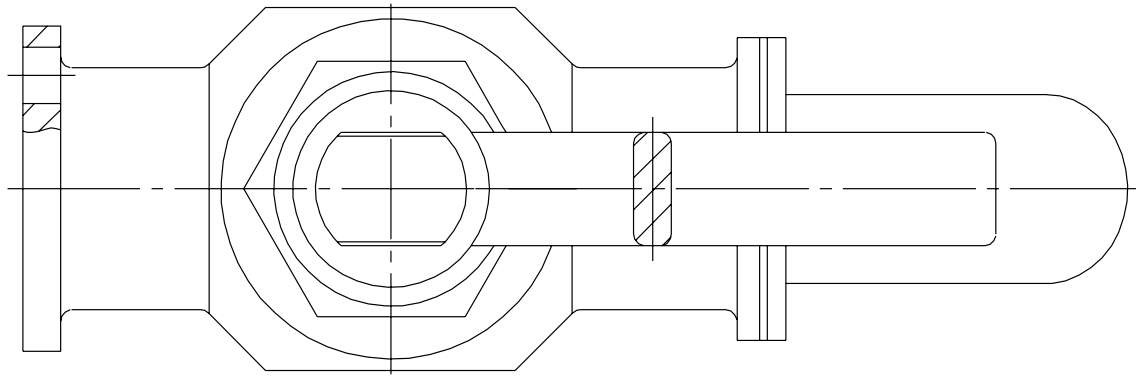
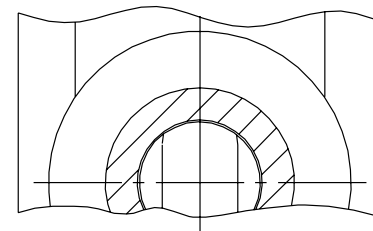
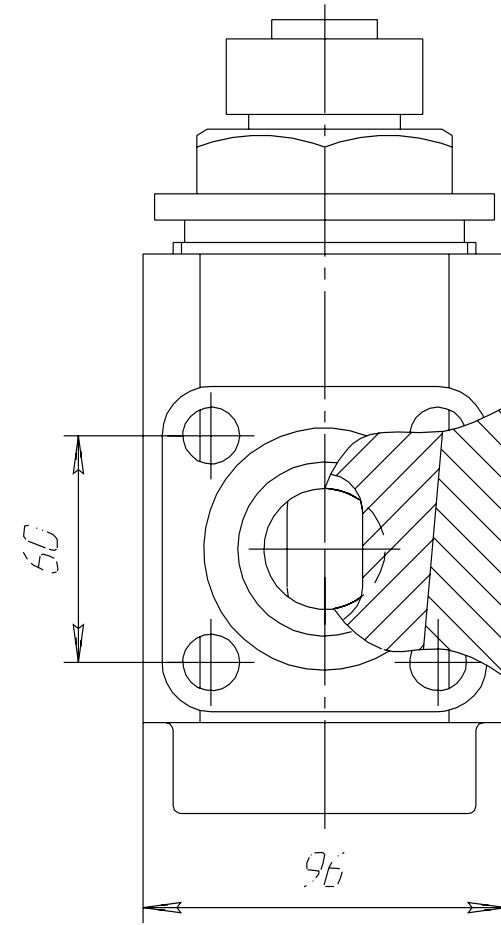


WYBUDOWA

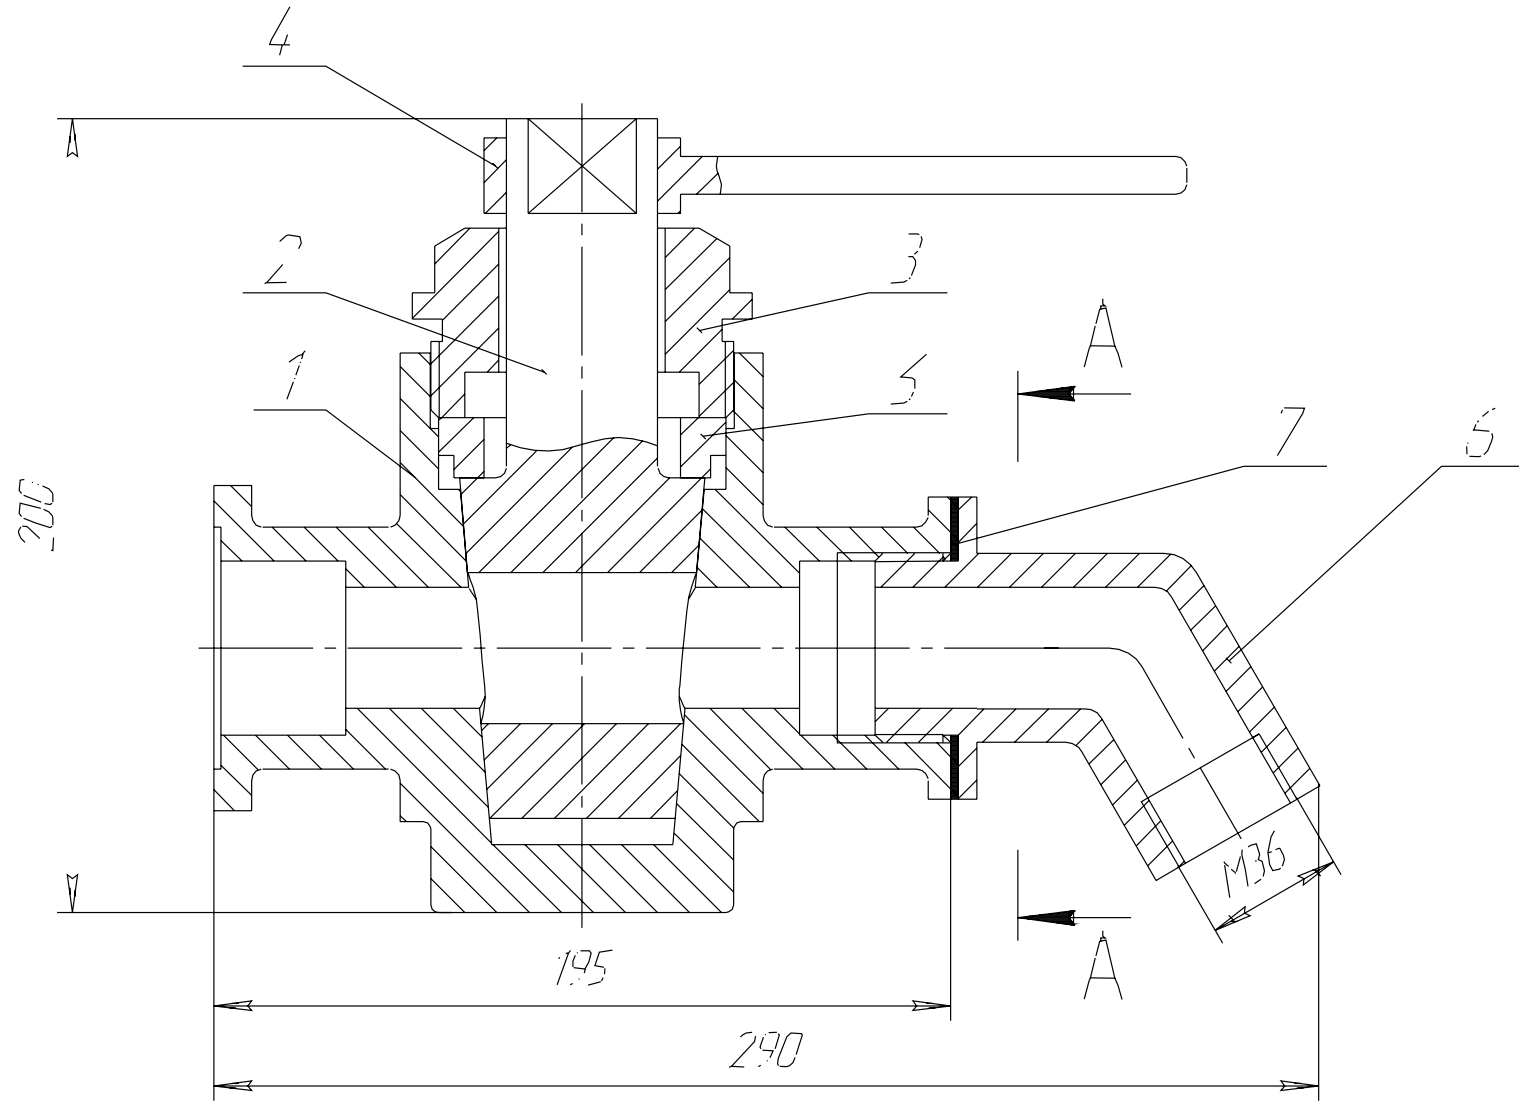

					М400.03.00.00.СБ			
Изм.	Лист	№ докум.	Подп.	Дата	Кран с краном Сборочный чертеж	Лист	Масштаб	Масштаб
Разраб.	Доработ.						1:2,85	1:1
Проб.	Контроль							
Техника						Лист	Листов	1
						ПРЧ		
Разраб.						У-519-8		
Стр.								