
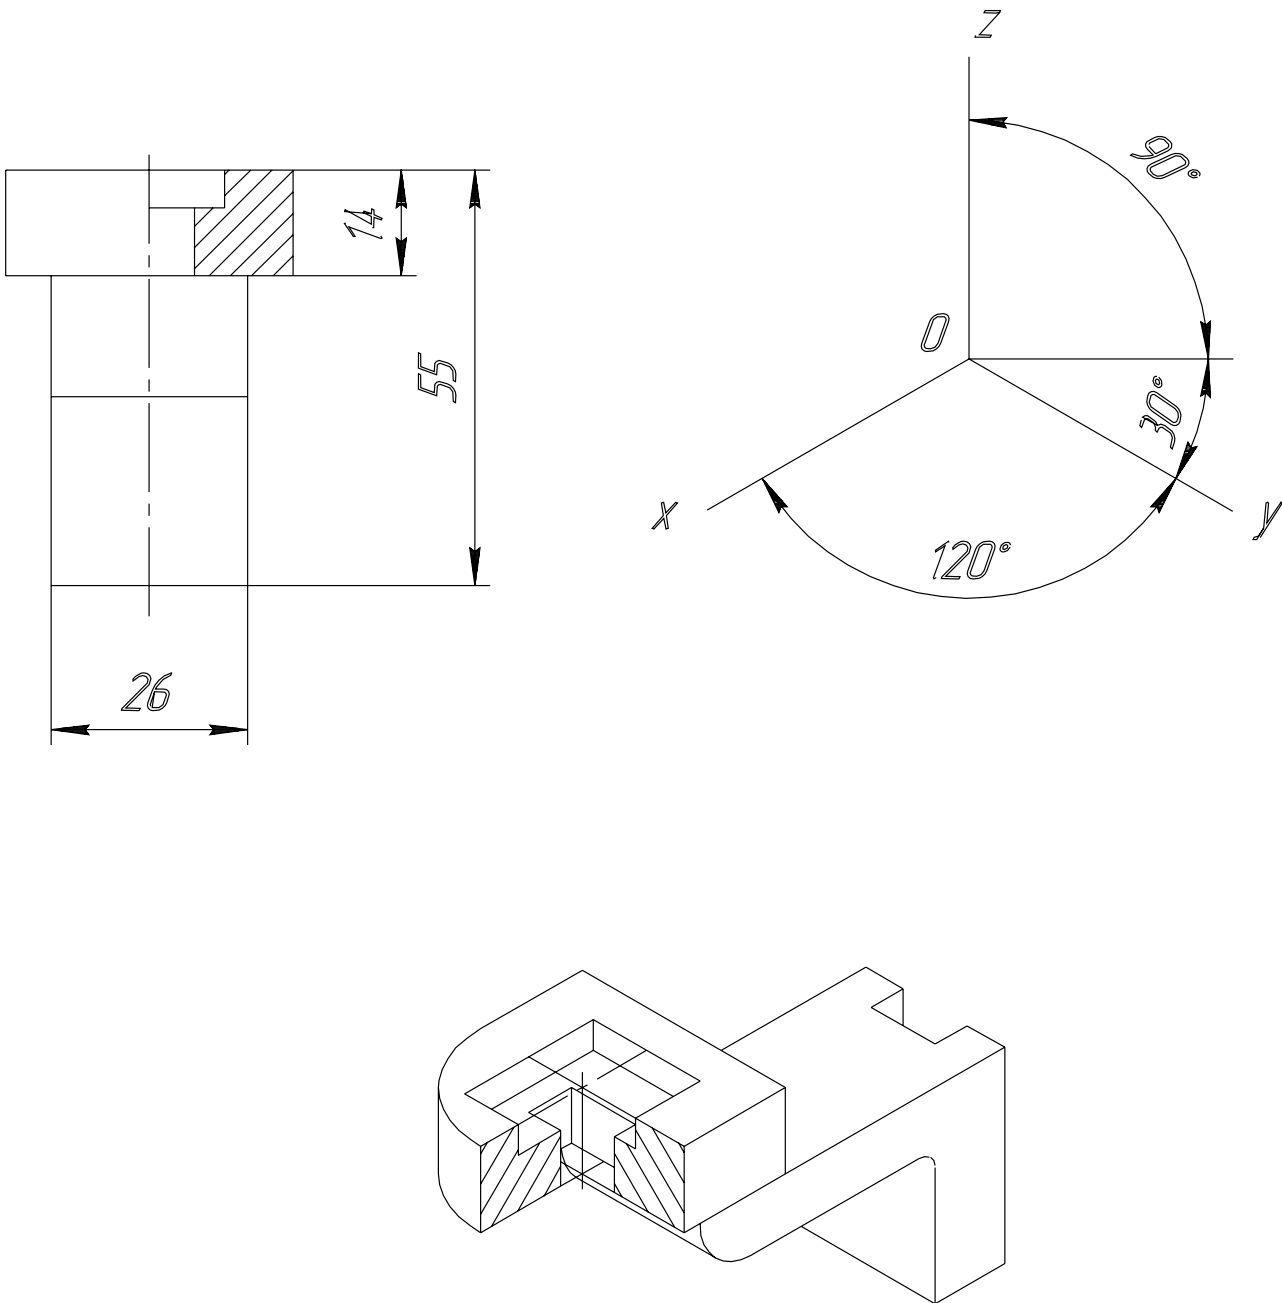


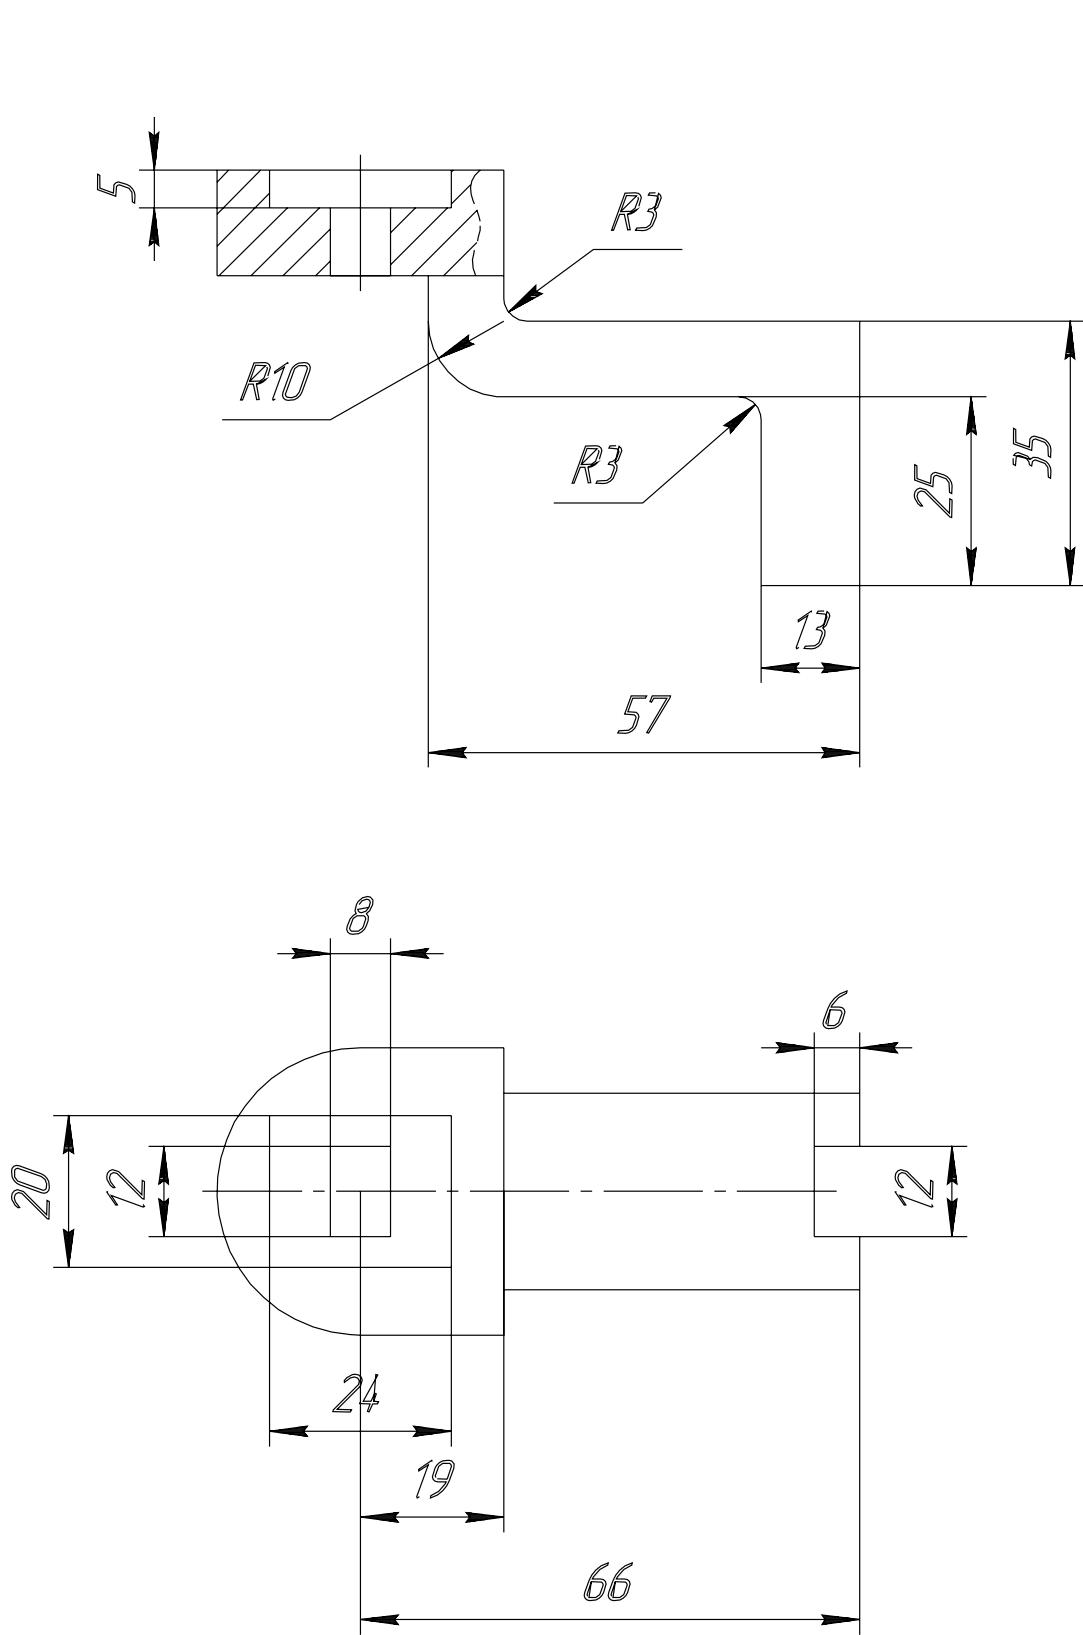

					КНГ.02.03.02			
Изм.	Лист	№ докум.	Подп.	Дата	Деталь	Лист	Масса	Масштаб
Разраб.	Дорохов						0,29	1:1
Проб.	Пузанава					Лист	Листов	1
Т.контр.								
Н.контр.					Сталь 10 ГОСТ 1050-88			ПГУП
Утв.								ЛТ-519-3