

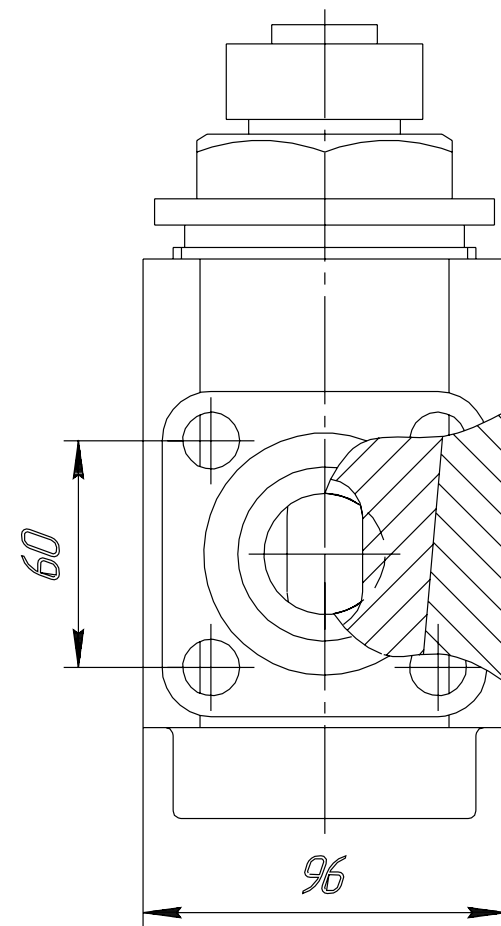
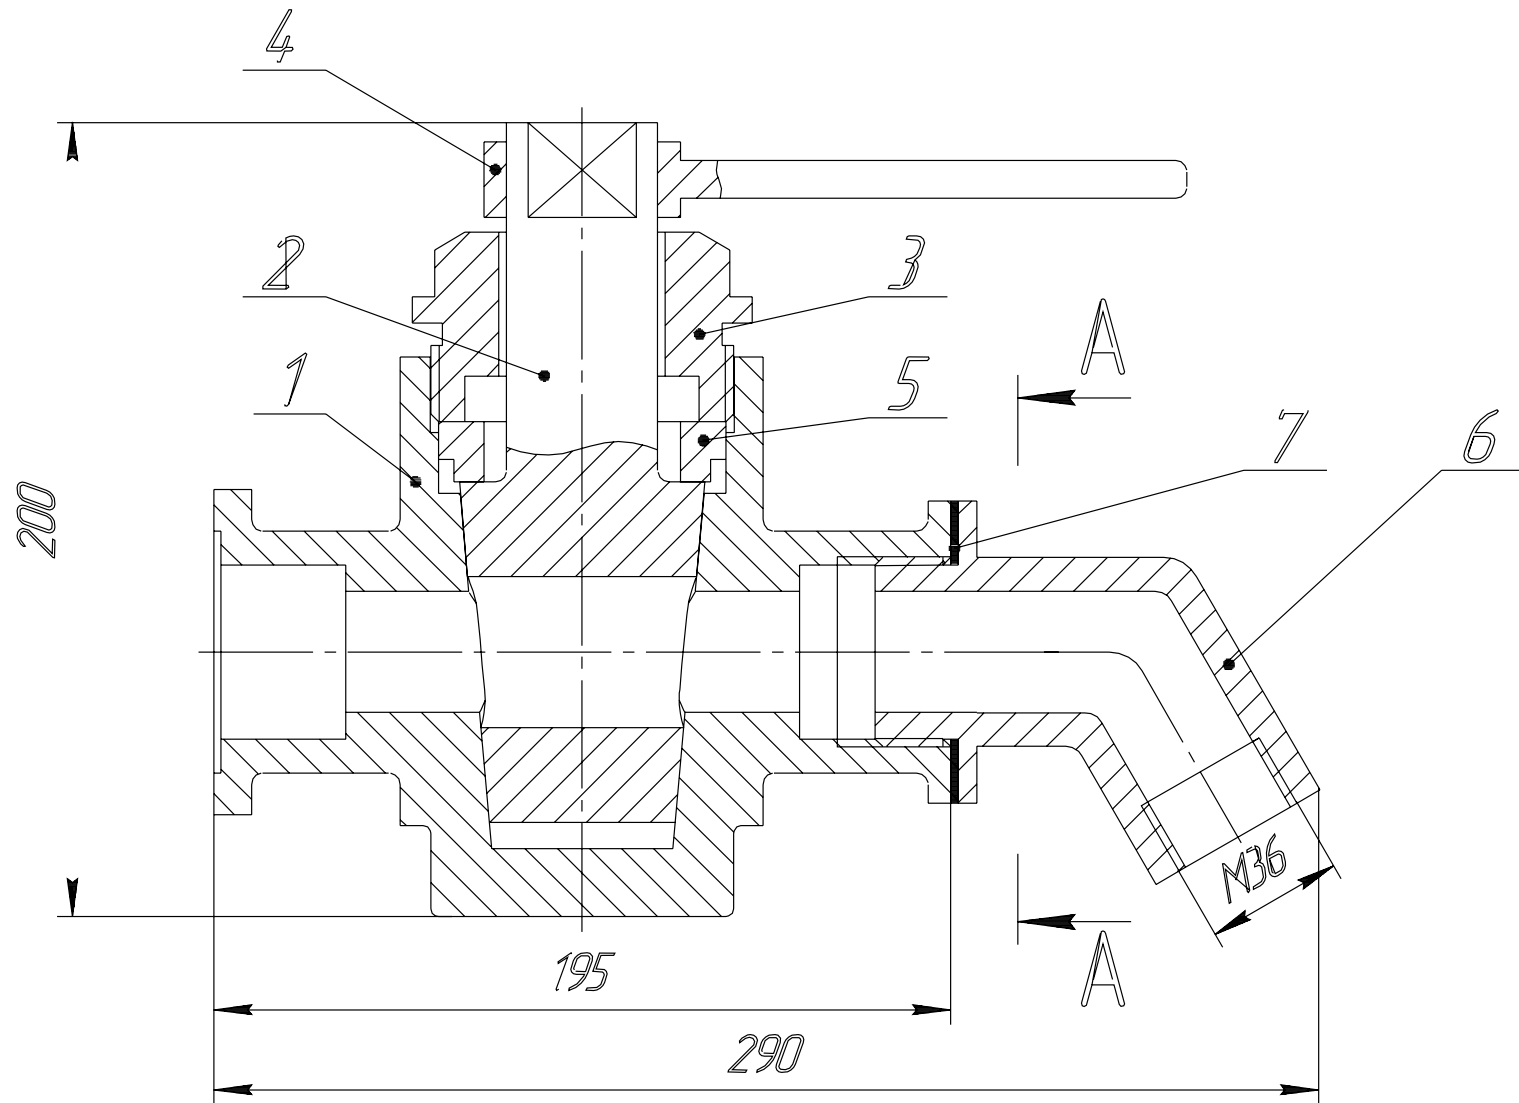


М400.03.00.00.СБ

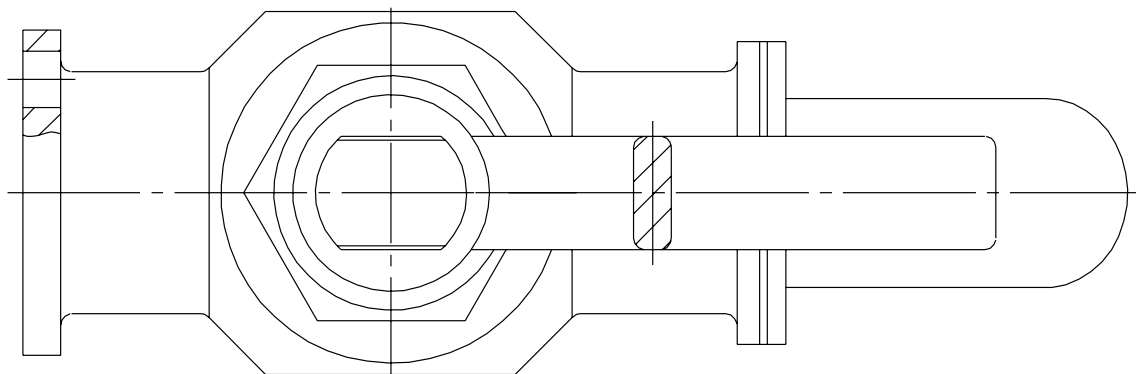

A-A

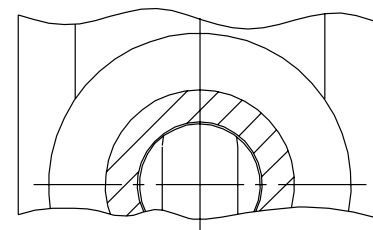

					М400.03.00.00.СБ			
Изм.	Лист	№ докум.	Подп.	Дата	Кран сливной Сборочный чертеж	Дет.	Масса	Масштаб
Разраб.	Дорохов						12,85	1:1
Пров.	Пизанова					Лист	Листов	1
Т.контр.						ПГУП ЛТ-519-3		
Н.контр.								
Утв.								