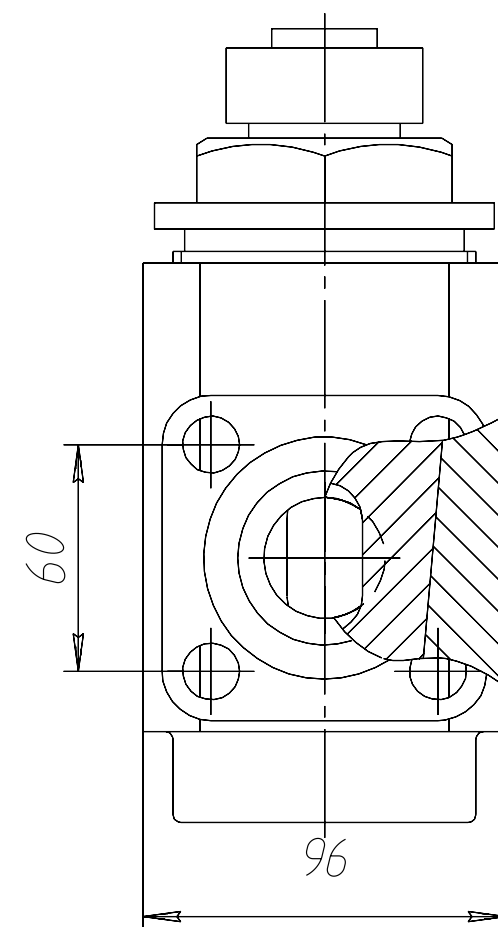
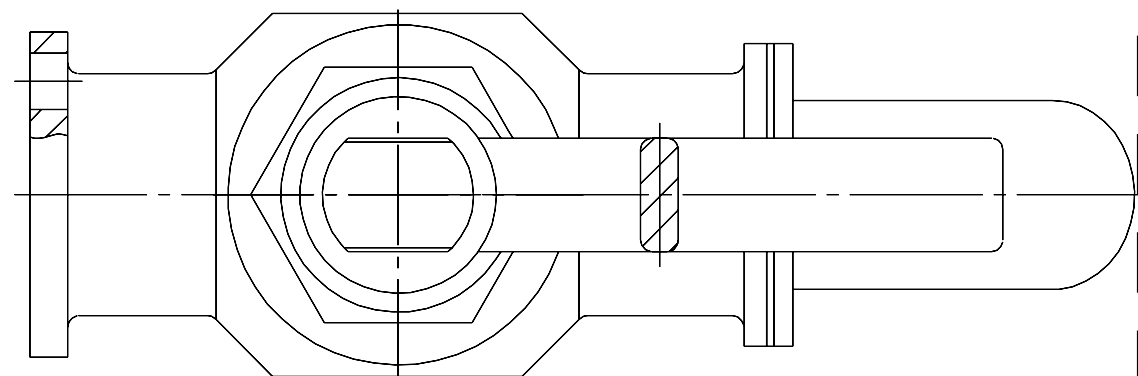
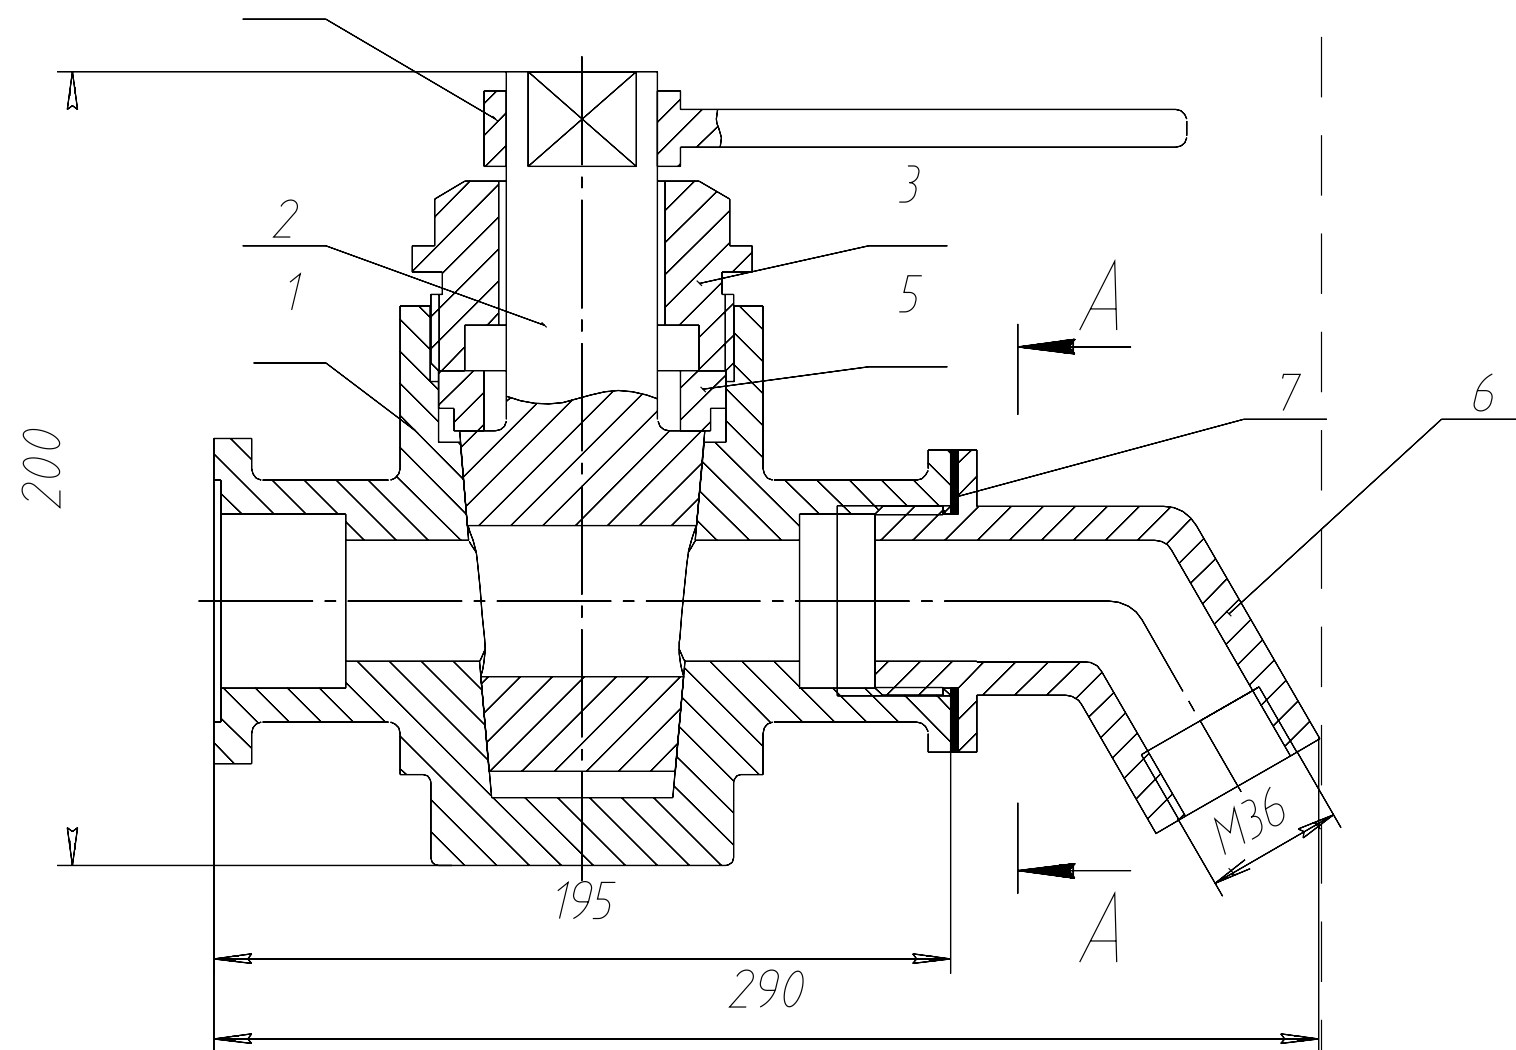
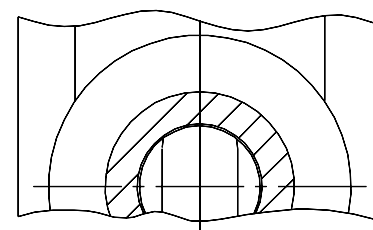


M400 03 00 00 00 00


$$A - A$$


					М400.03.00.00.СБ						
Изм	Лист	№ докум	Подп	Дата	Кран сливной Сборочный чертеж			Лист	Масса	Масштаб	
Разраб	Дорохов									12,85	1:1
Пров	Пузанова										
Т контр								Лист		Листов 1	
Н контр					ПГУПС ЛТ-519-3						
Утв											