

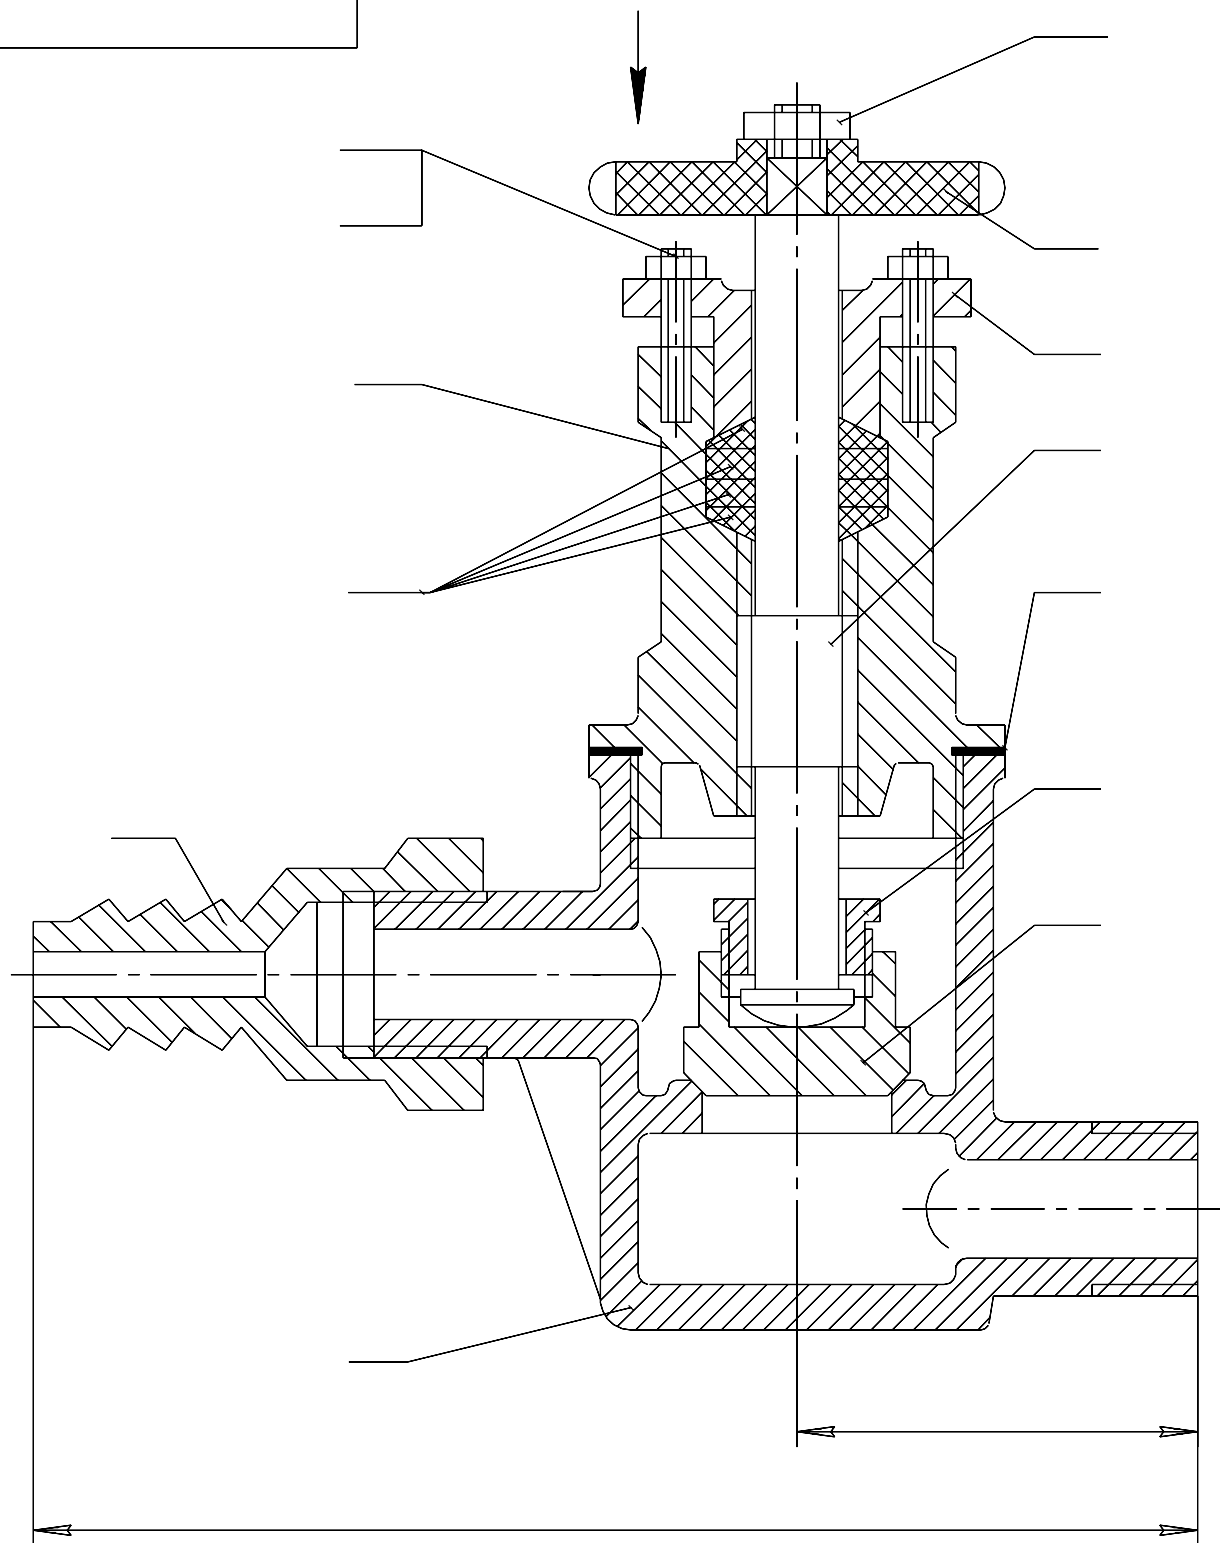
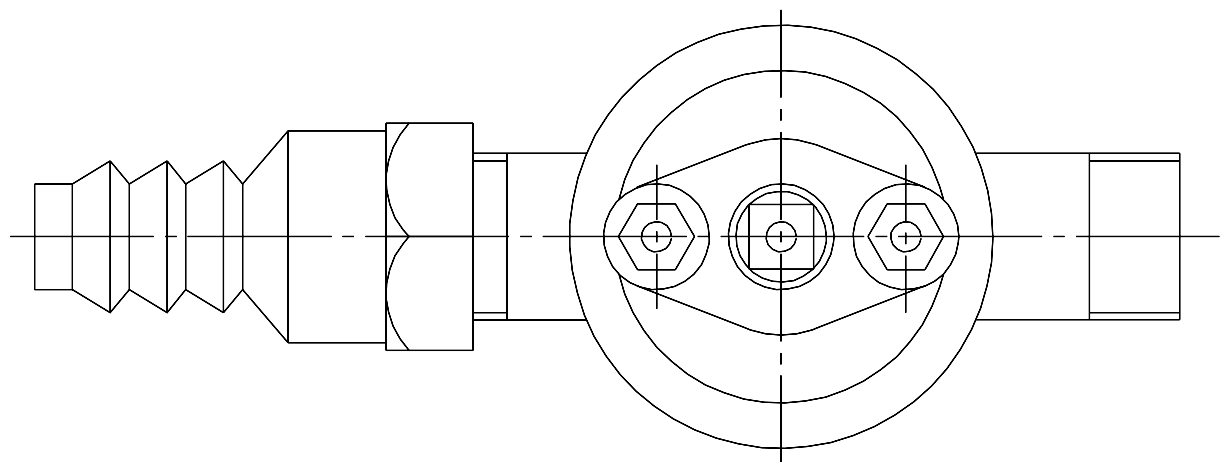


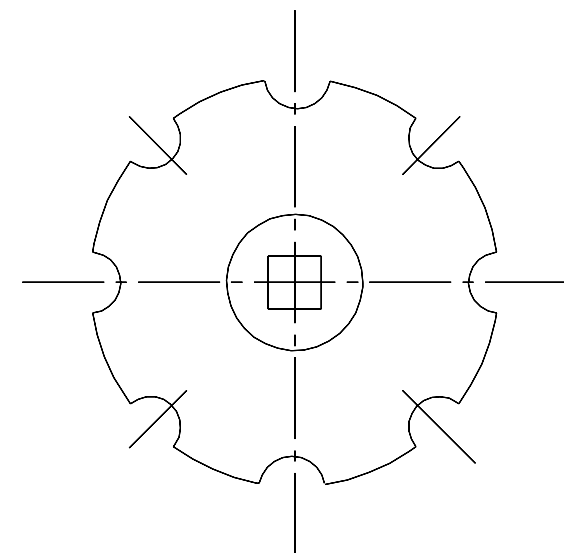

Детали поз 5, 11 усл не показаны

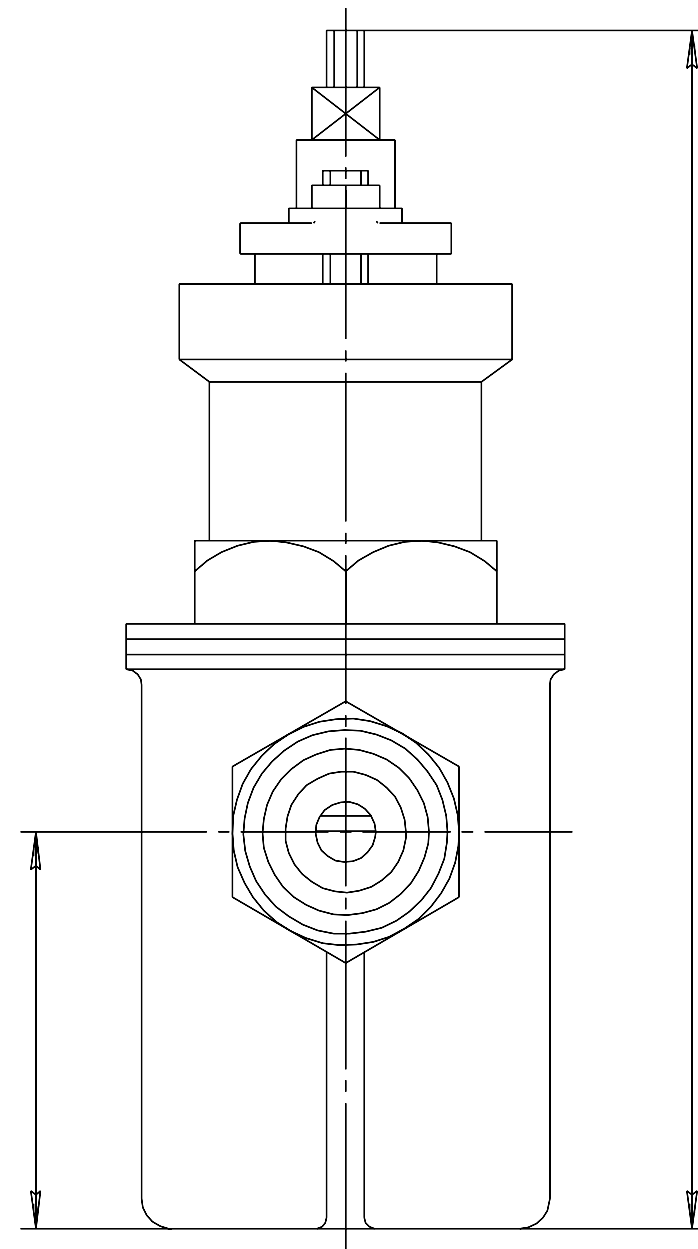

					М400 52 00 00 СД					
Изм	Лист	№ докум	Подп	Дата	Клапан Сборочный чертеж		Лист	Масса	Масштаб	
Разраб	Судоров ДС								12	
Пров	Лузанова									
Т кандр							Лист		Листов	1
Н кандр							АТ-519-3			
УТВ										