

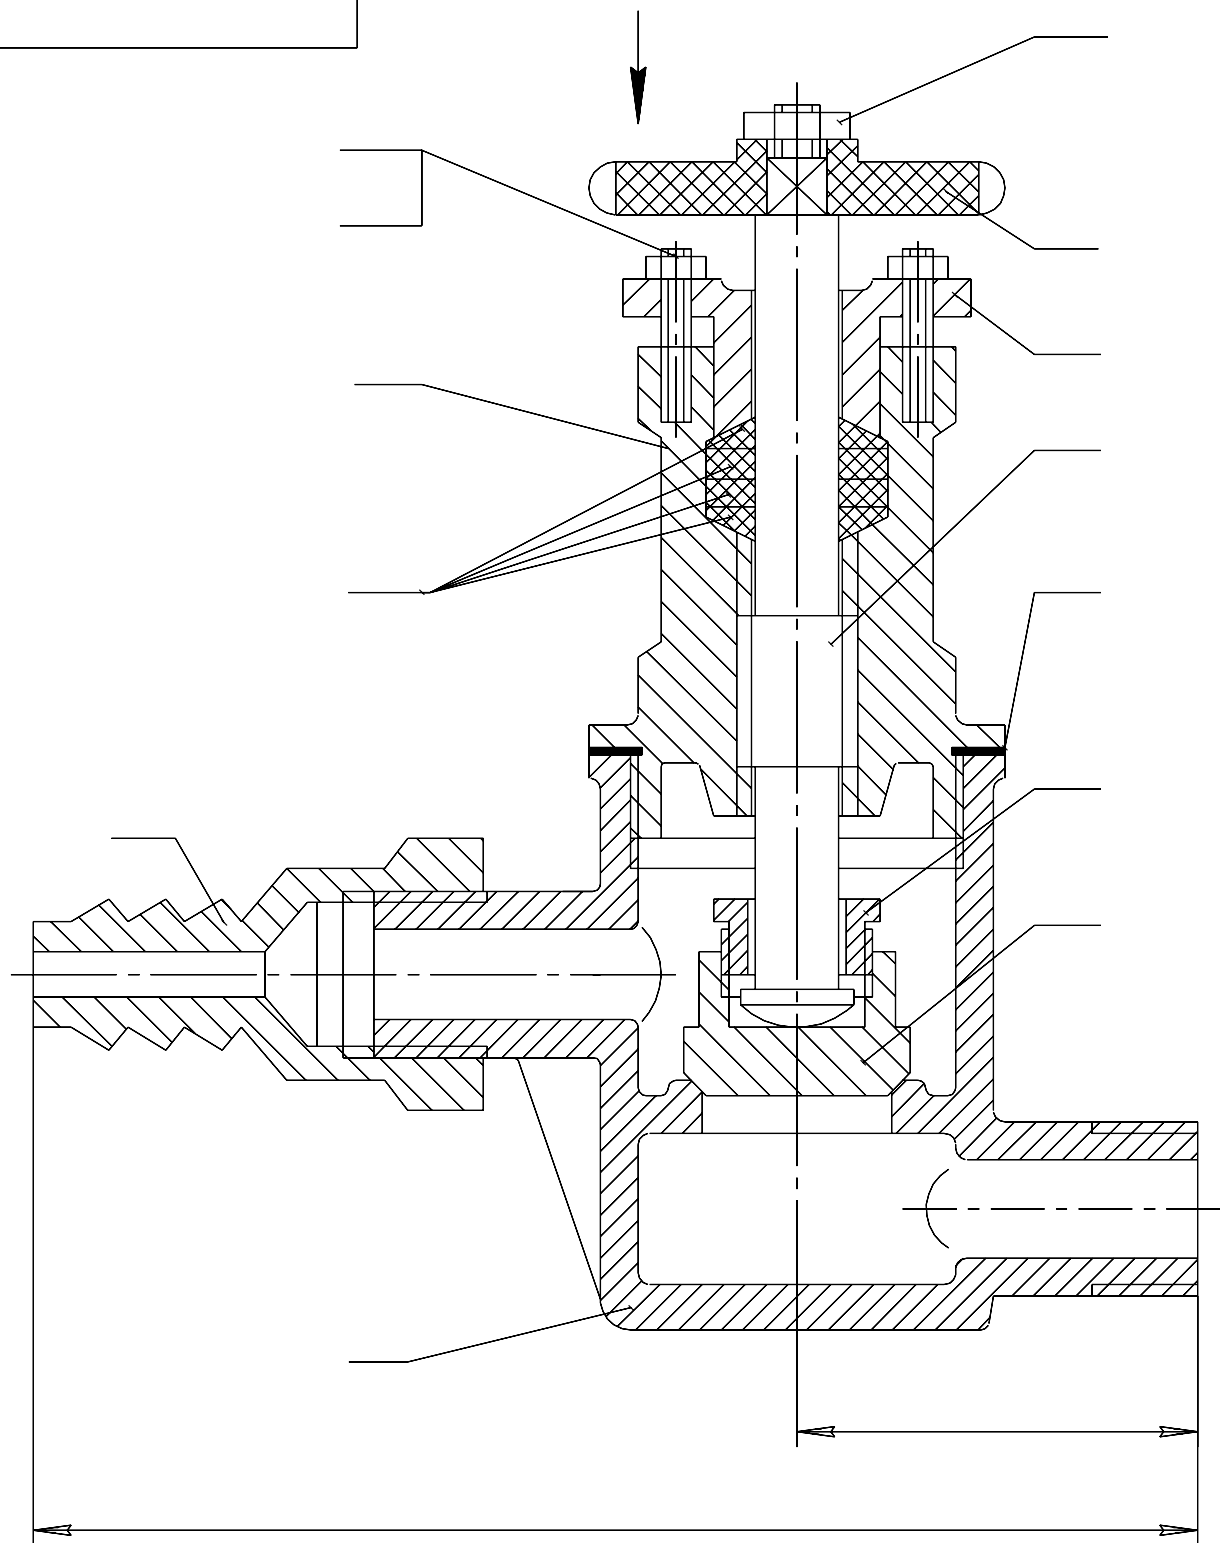
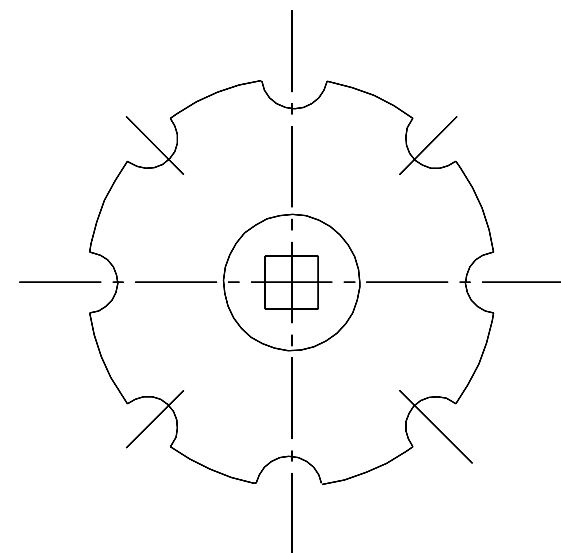


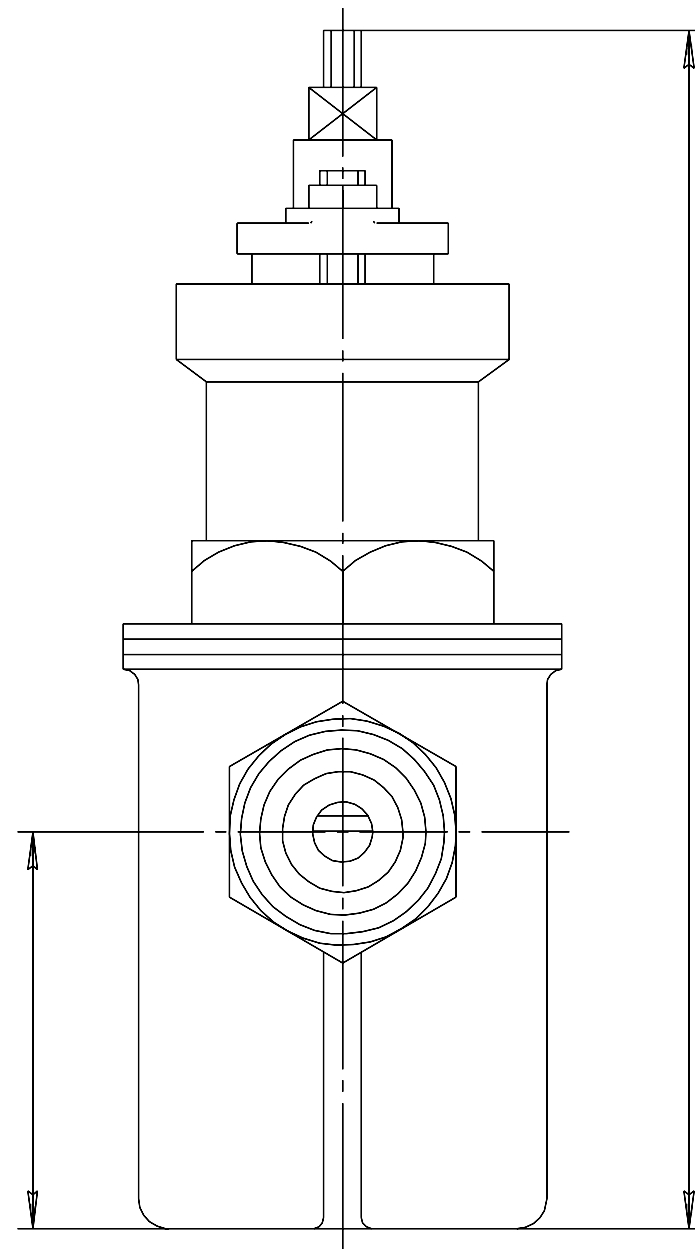

Детали поз 5, 11 усл не показаны

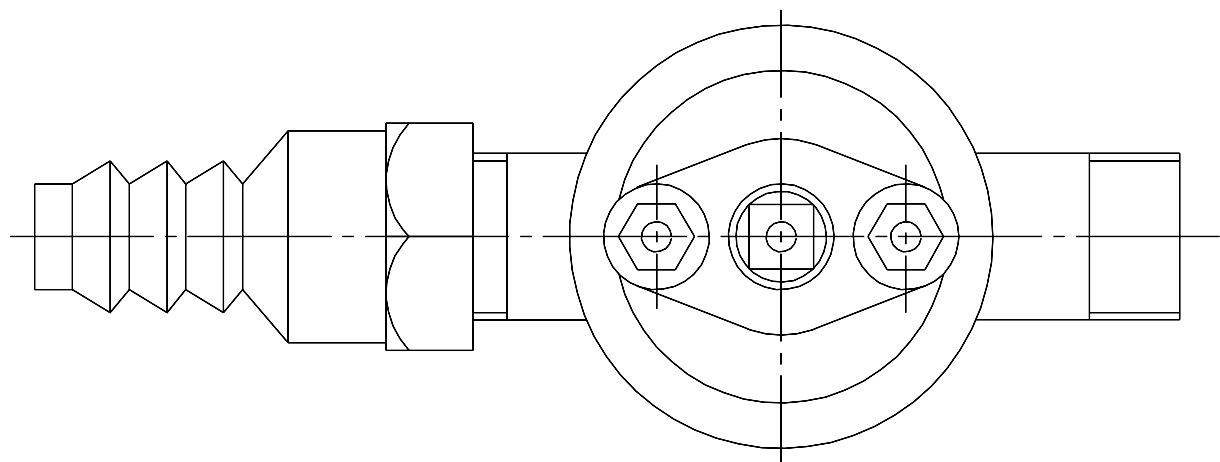

					М400 52 00 00 СД			
Изм	Лист	№ докум	Подп	Дата	Клапан Сборочный чертеж	Лист	Масса	Масштаб
Разраб	Судоров Д С							12
Пров	Лузанова							
Т кандр						Лист	Листов	1
Н кандр						АТ-519-3		
УЛВ								