

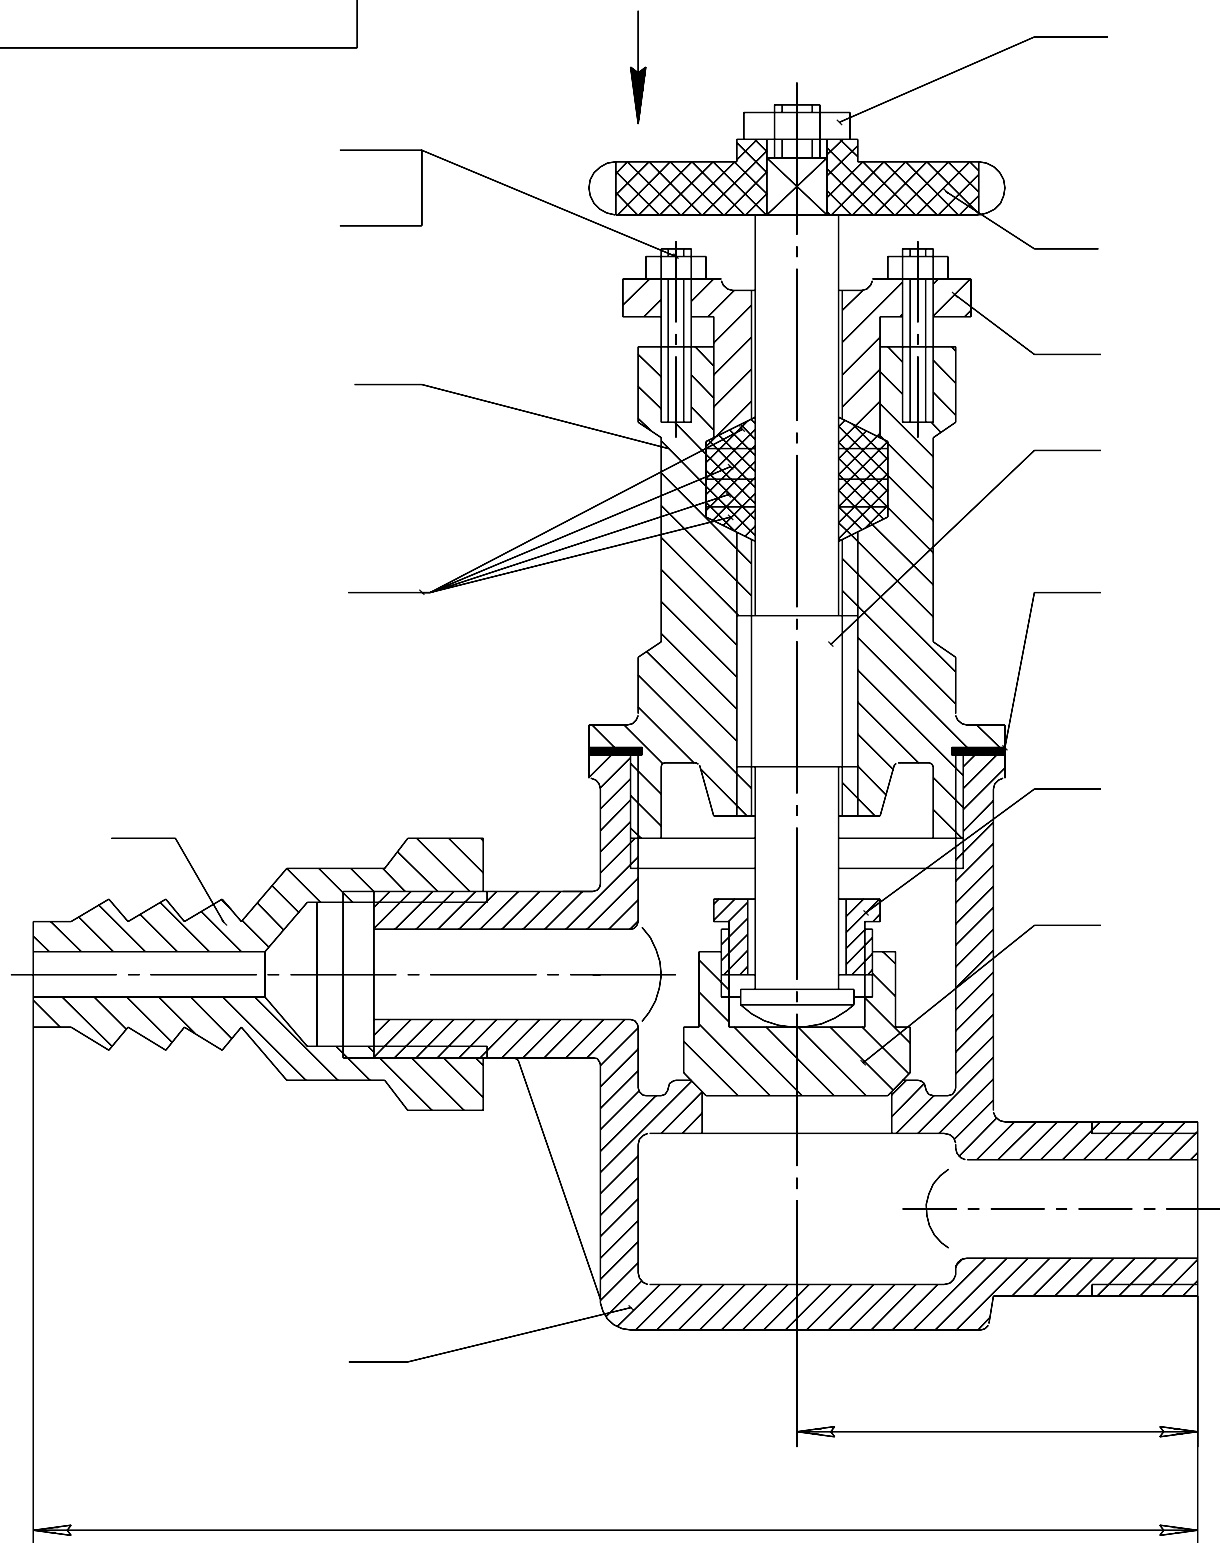
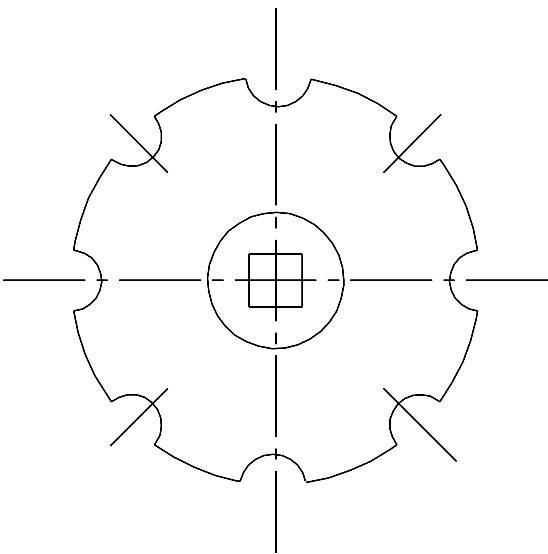


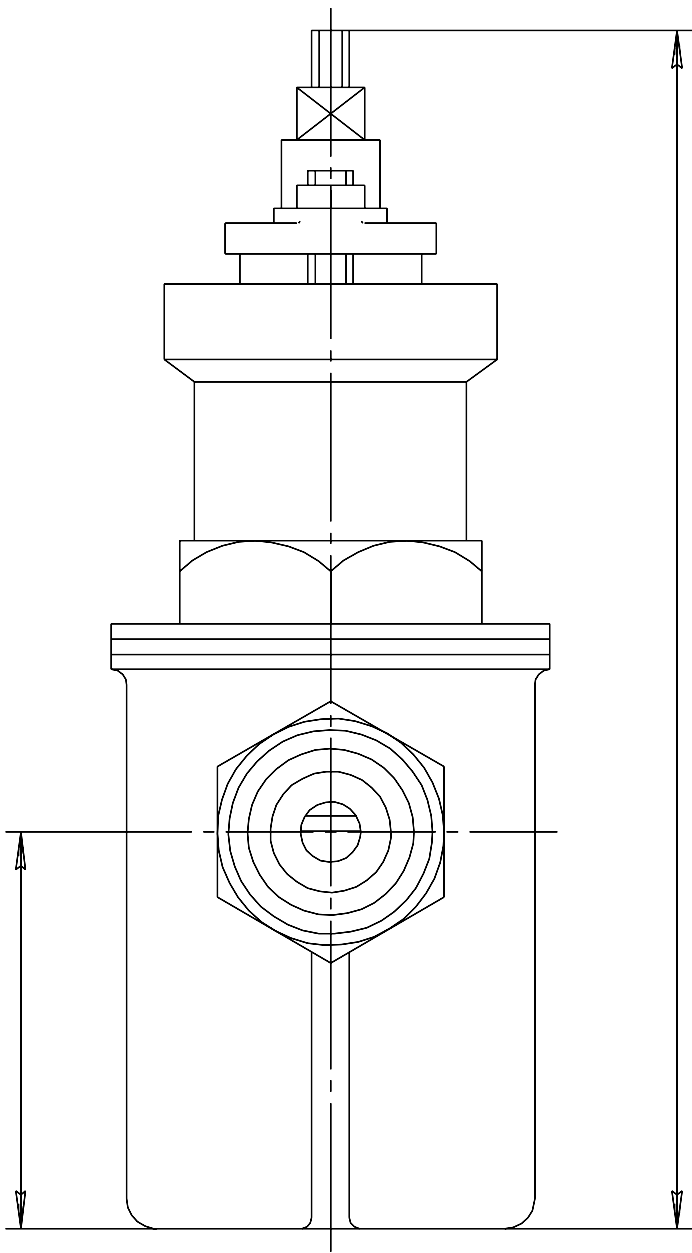

Детали поз 5, 11 усл не показаны

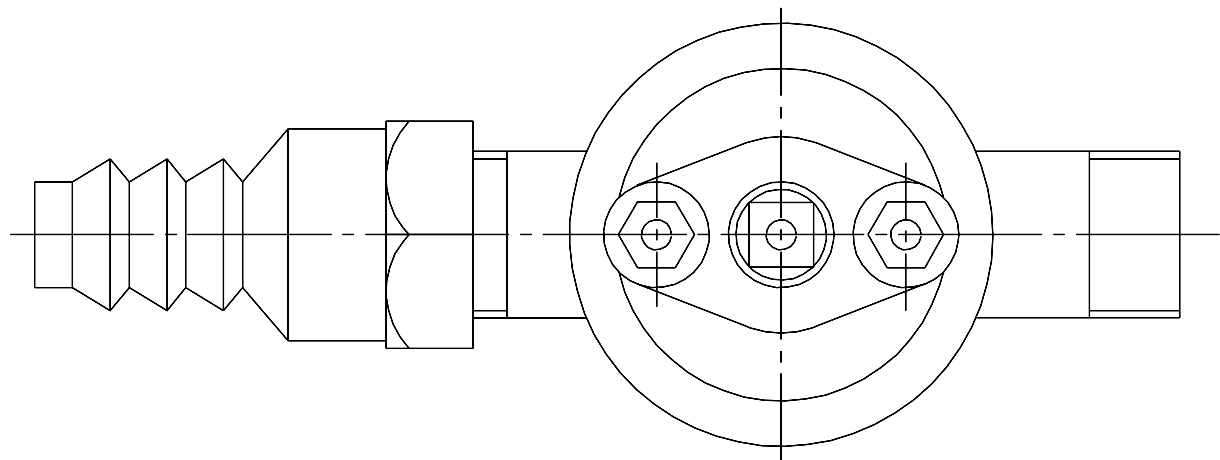

					М400 52 00 00 СД			
Изм	Лист	№ докум	Повт	Дата	Клапан - Сборочный чертеж	Лист	Масса	Масштаб
Разраб	Суворов ДС							12
Пров	Лузанова							
1 каноп						Лист	Листов	1
Н каноп					АТ-519-3			
УЛВ								