
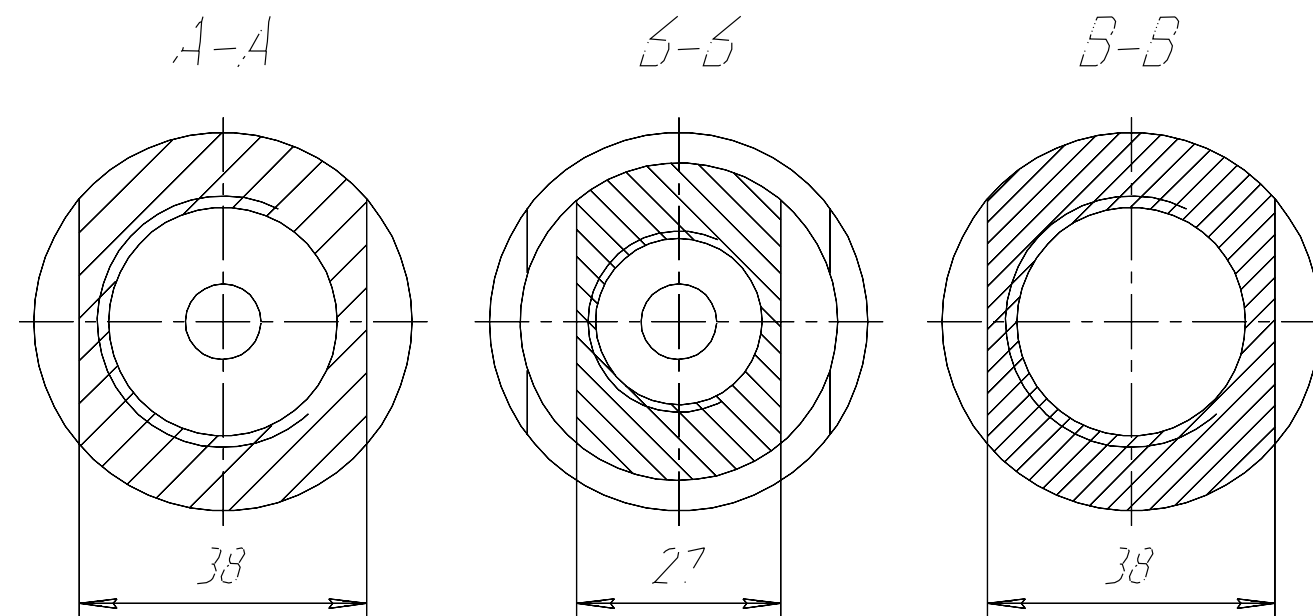


КН.03.03.00.СБ

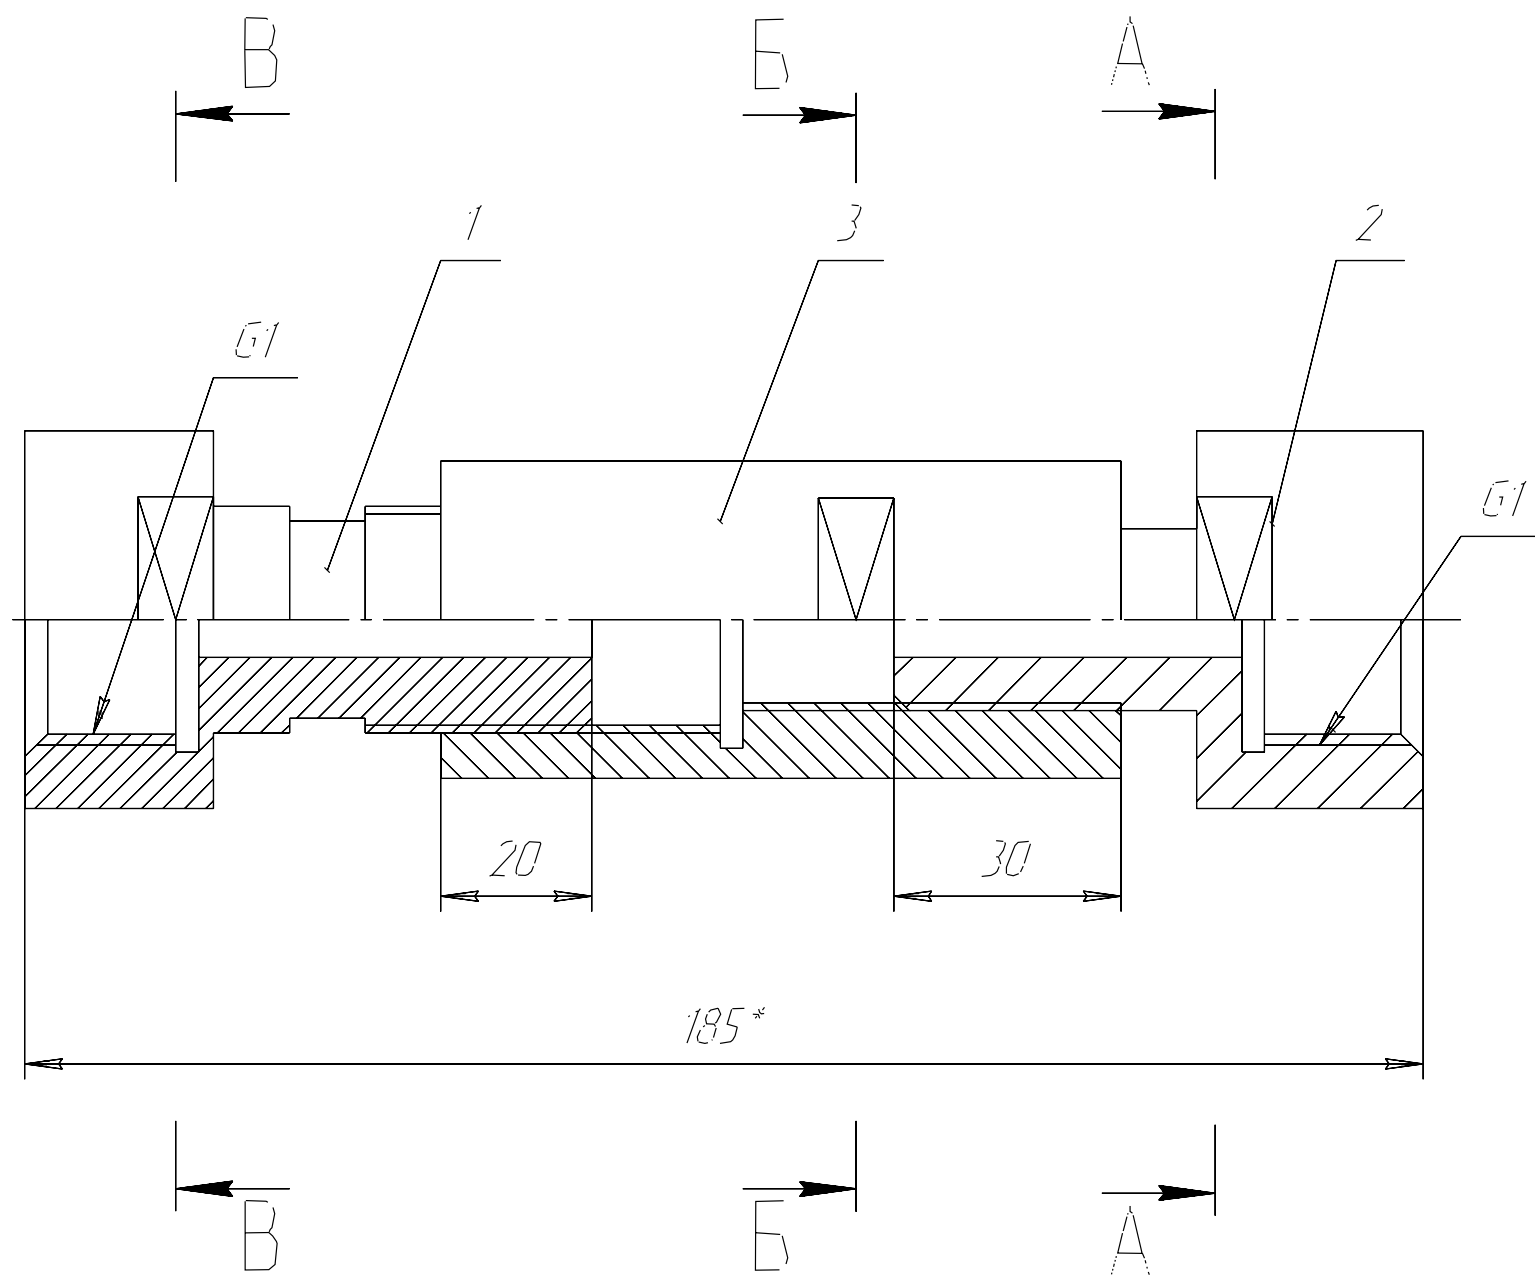

*Размер для справок

					КН.03.03.00.СБ			
Изм.	Лист	№ докум.	Подп.	Дата	Узел Сборочный чертеж	Лист	Масса	Масштаб
Разраб.	Дорохов							1:1
Грб	Гузанава					Лист	Листов	1
Т.контр.						ПГУПС 17-519-3		
Н.контр.								
Утв								