

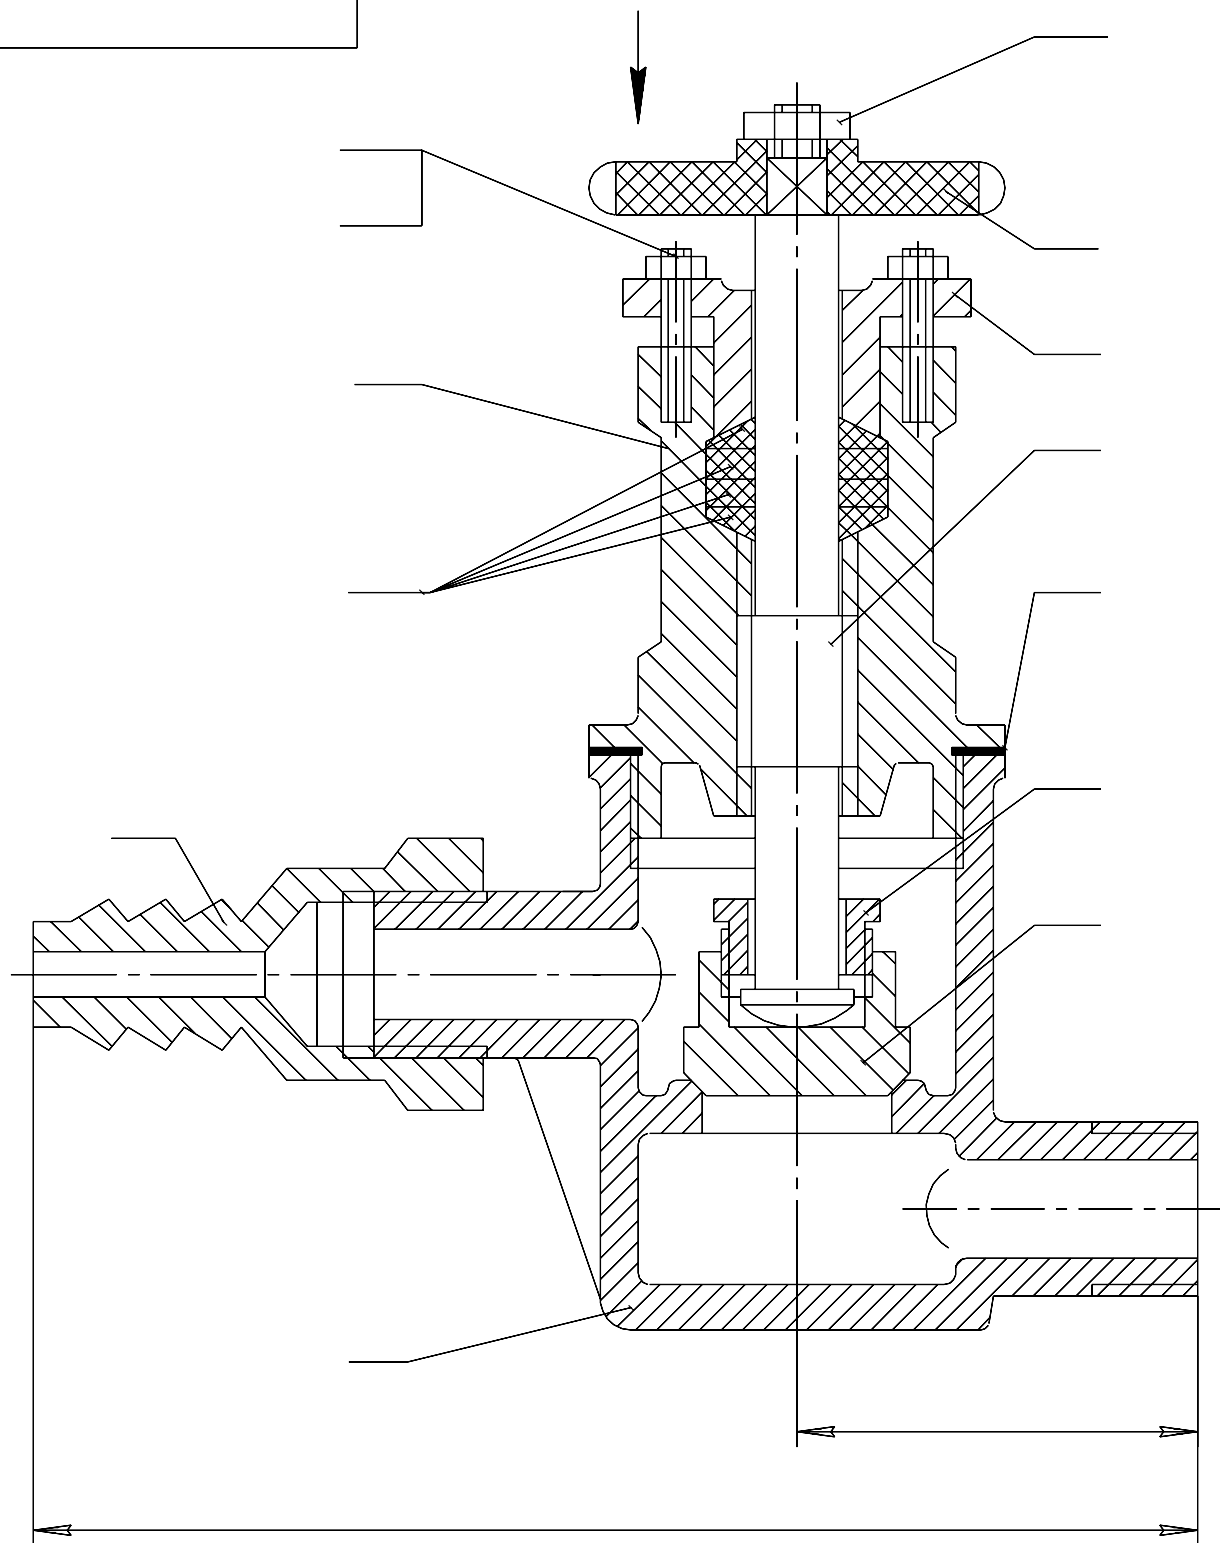
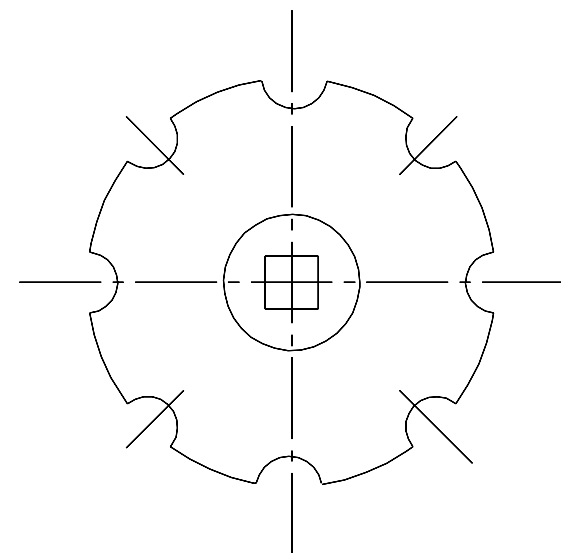


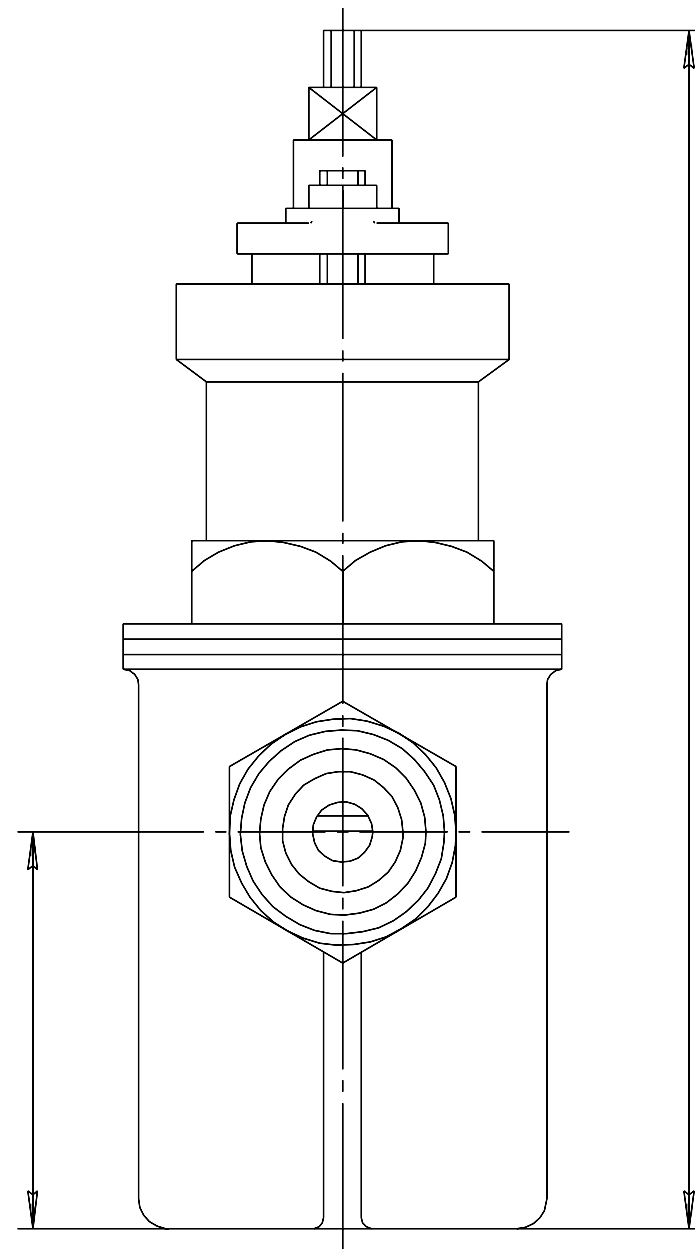

Детали поз 5, 11 усл не показаны

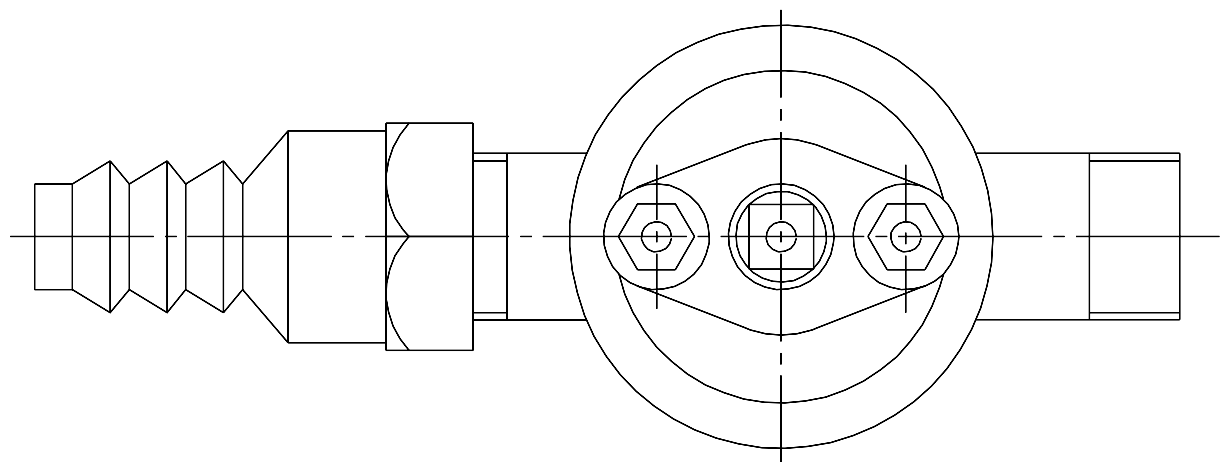

|         |            |         |      |      |                            |          |        |         |
|---------|------------|---------|------|------|----------------------------|----------|--------|---------|
|         |            |         |      |      | М400 52 00 00 СД           |          |        |         |
| Изм     | Лист       | № докум | Подп | Дата | Клапан<br>Сборочный чертеж | Лист     | Масса  | Масштаб |
| Разраб  | Судоров ДС |         |      |      |                            |          |        | 12      |
| Пров    | Лузанова   |         |      |      |                            |          |        |         |
| Т.контр |            |         |      |      |                            | Лист     | Листов | 1       |
| Н.контр |            |         |      |      |                            | АТ-519-3 |        |         |
| УЛВ     |            |         |      |      |                            |          |        |         |