

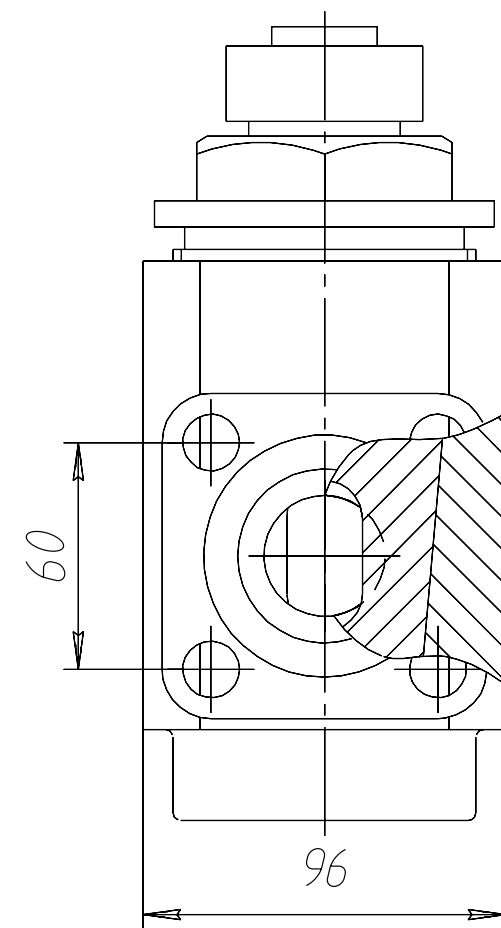
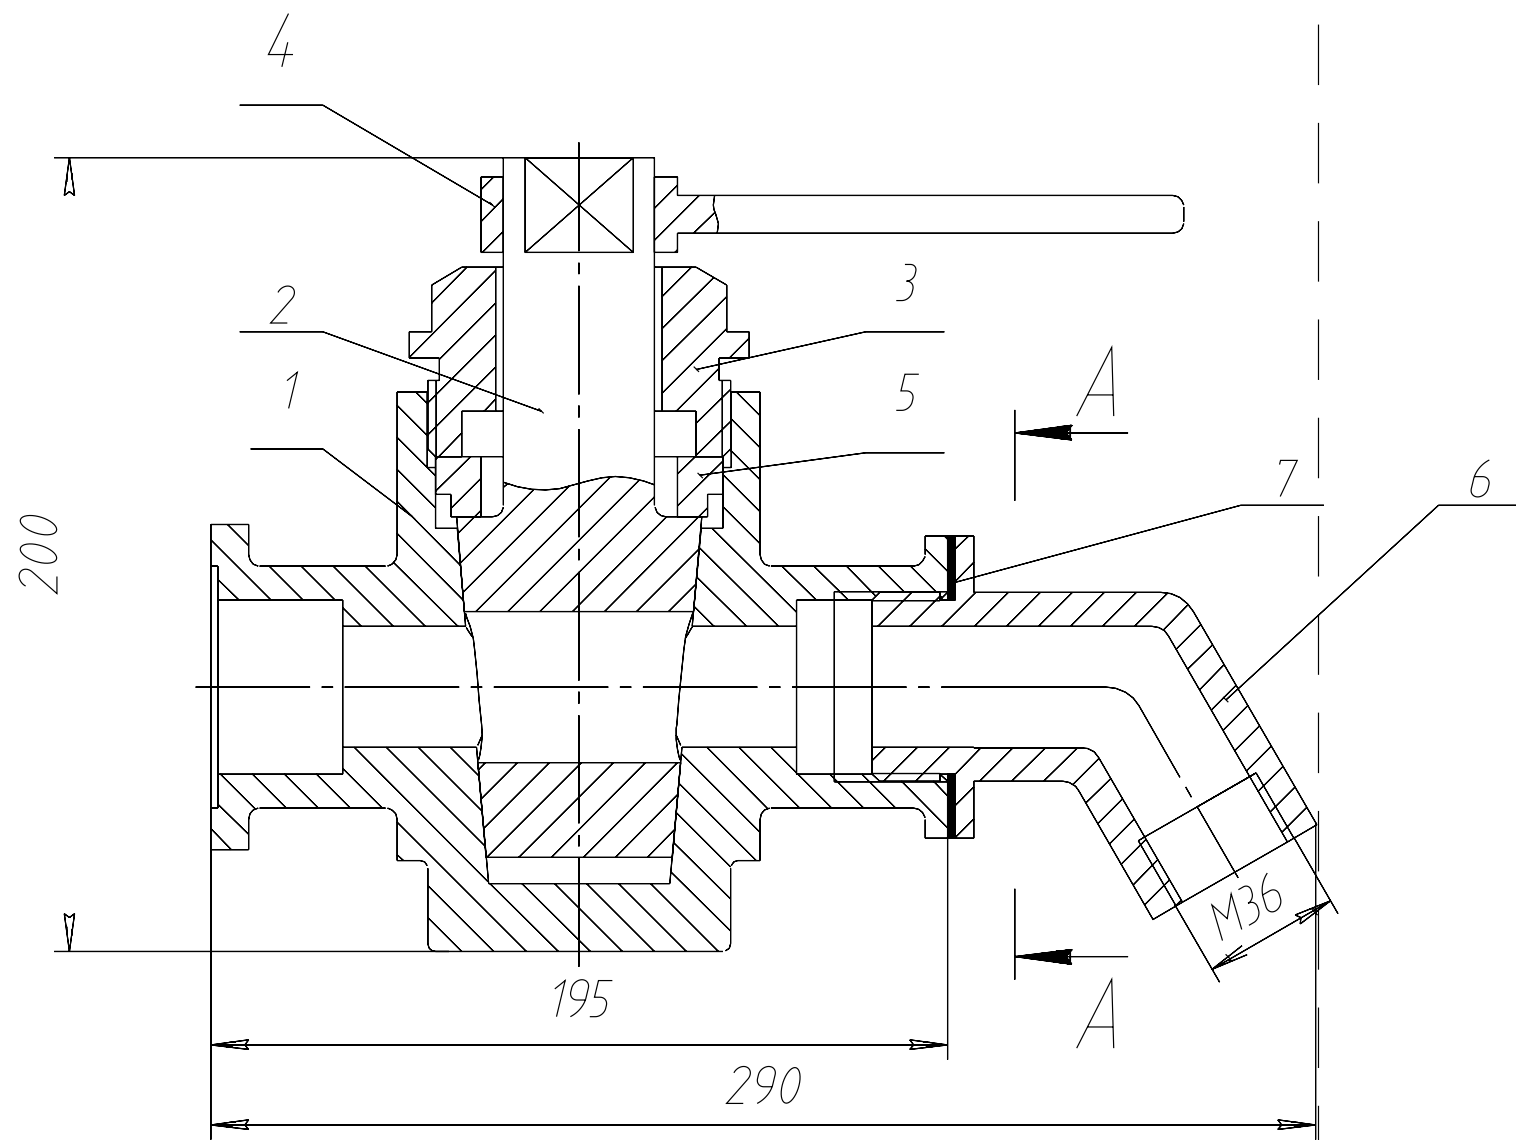


М400.03.00.00.СБ

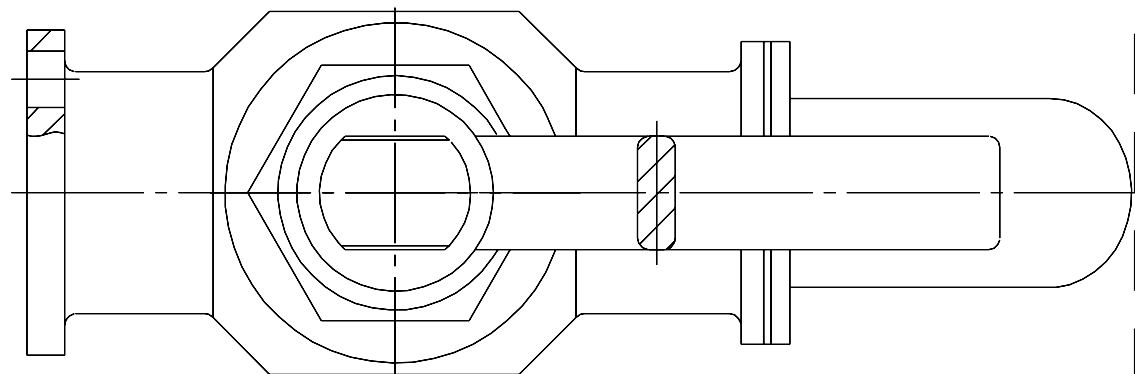

A-A

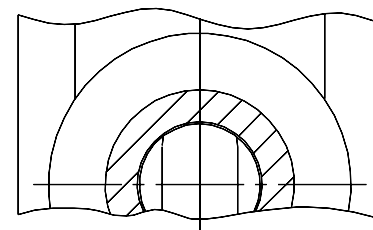

					М400.03.00.00.СБ			
Изм	Лист	№ докум	Подп	Дата	Кран сливной Сборочный чертеж	Лит	Масса	Масштаб
Разраб	Дорохов						12,85	1:1
Пров	Пузанова							
Т контр						Лист	Листов	1
Н контр						ПГУПС		
Утв						ЛТ-519-3		