

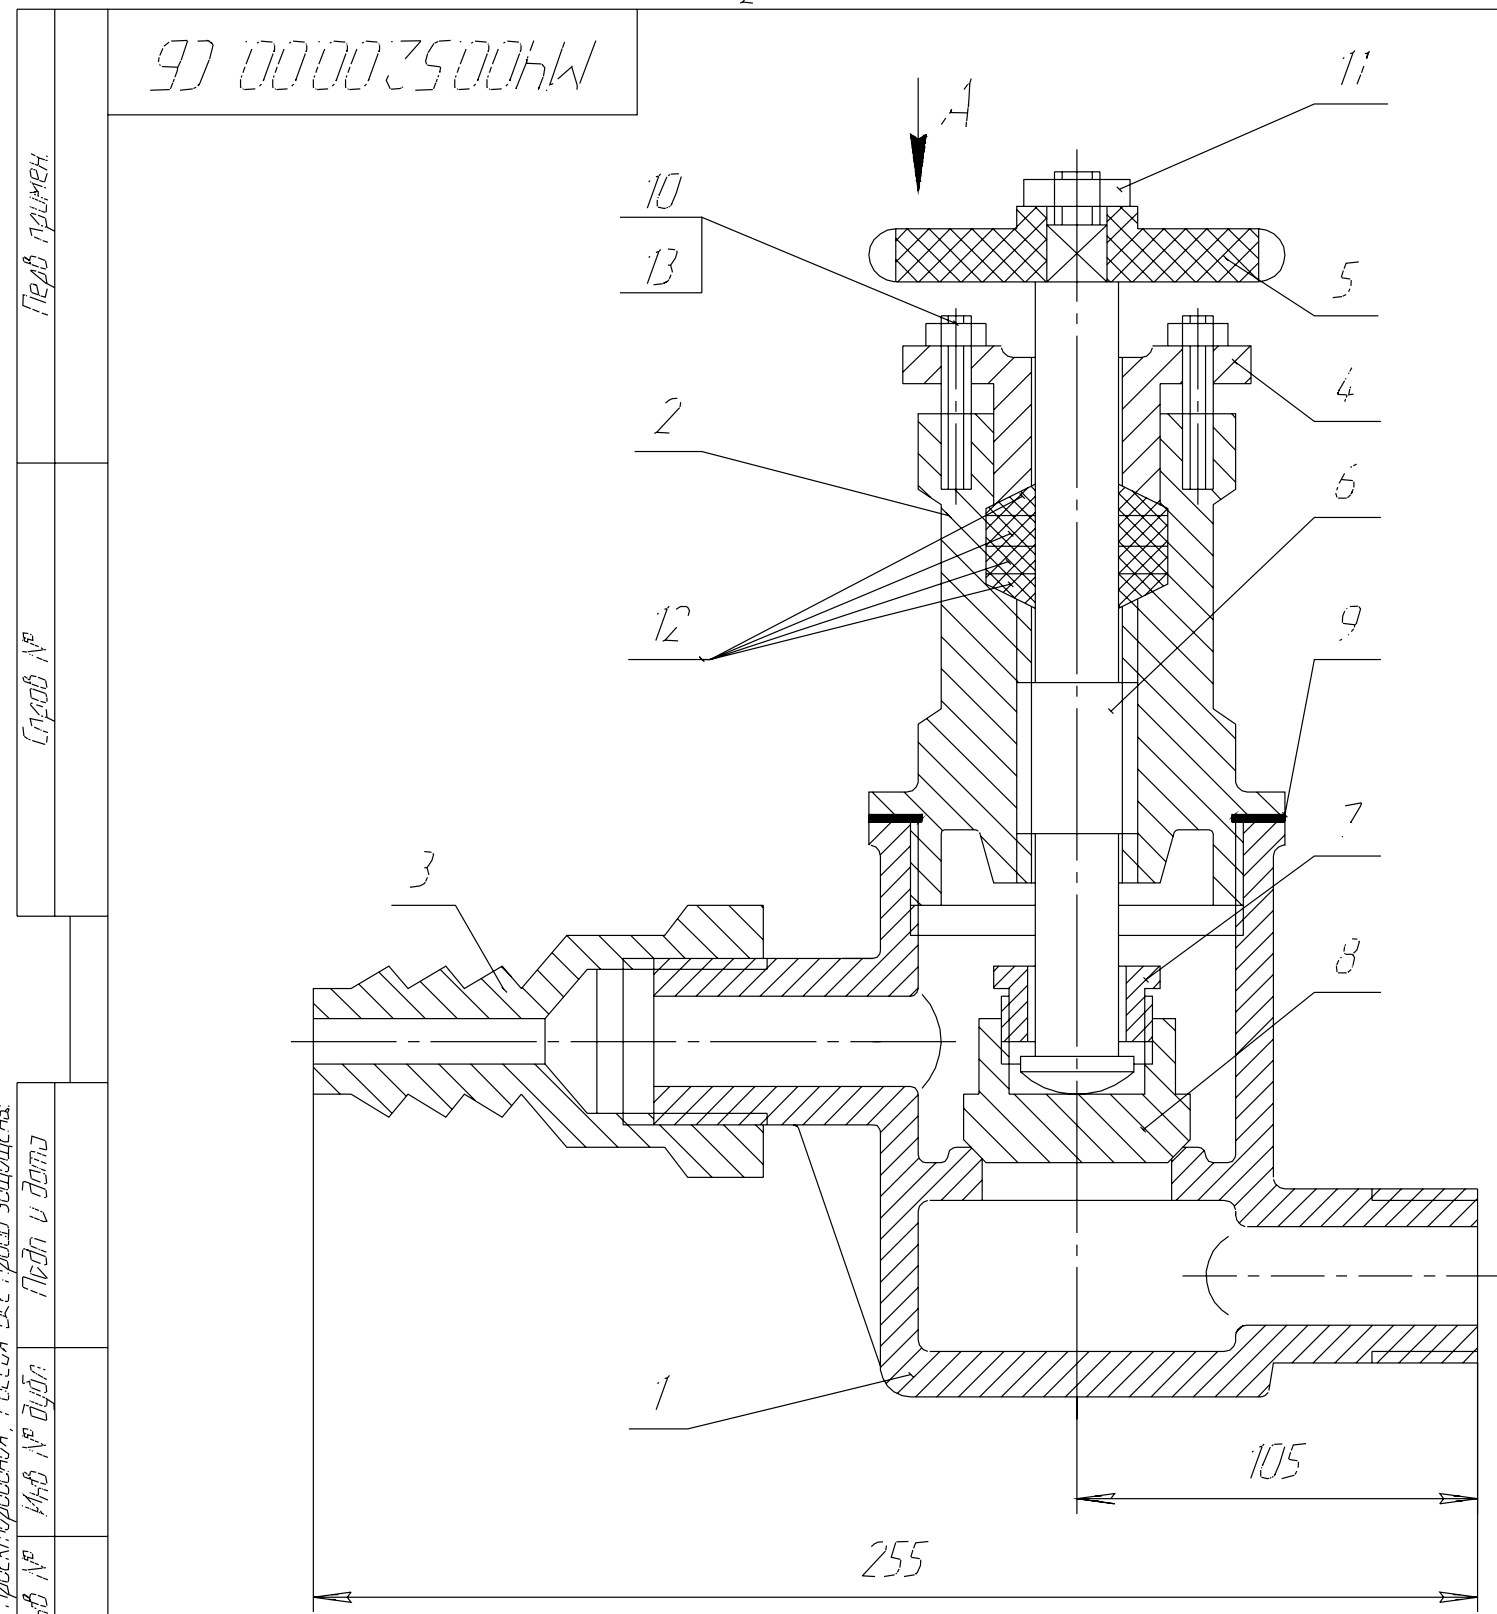


Контракт-36 от 2025-000 "АКОН-Системы проектирования". Актуал для всего здания
Изд № 0001
Подп и дата
Изд № 0001
Подп и дата
Изд № 0001
Подп и дата

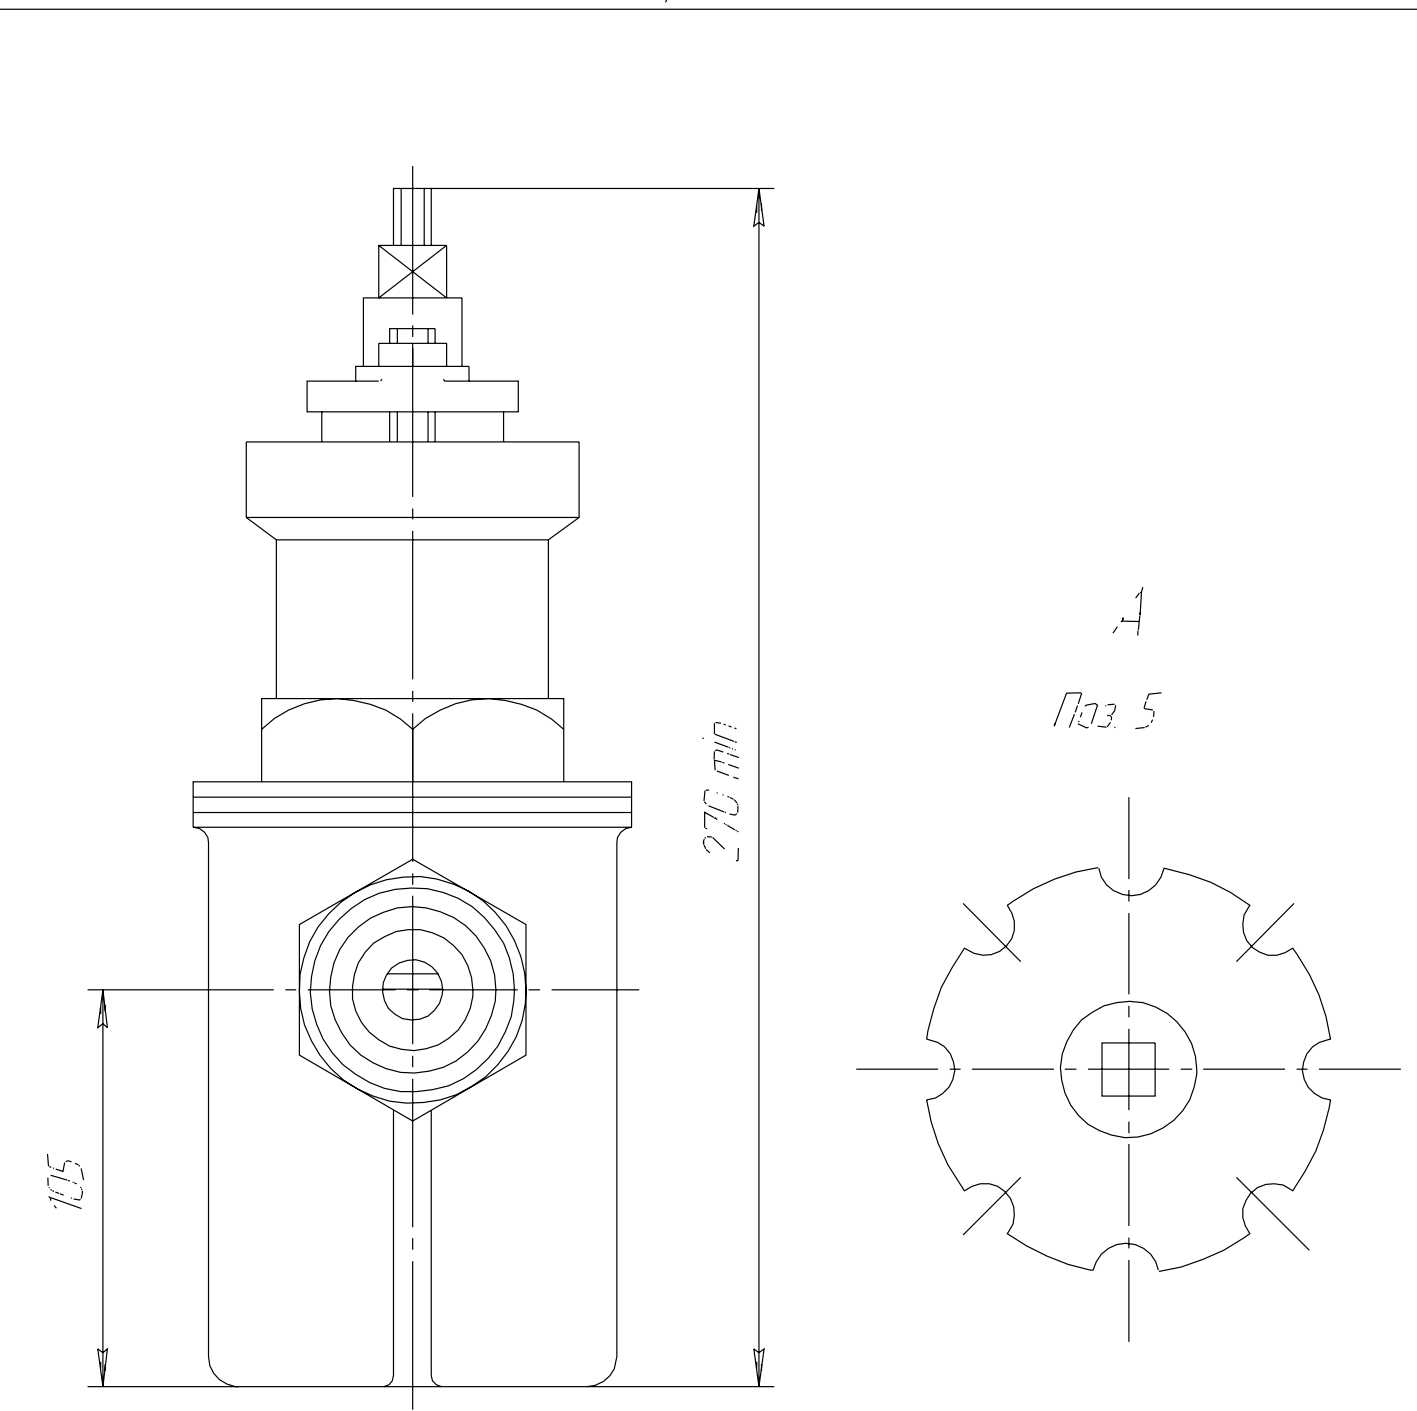

Детали поз 5, 11 усл. не показаны

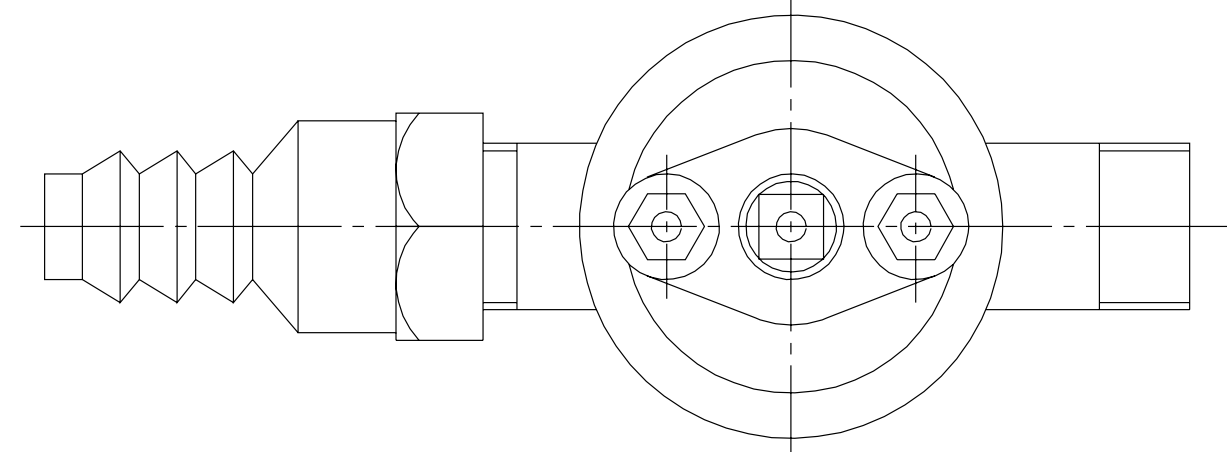

М4005200.00 СБ				Лист	Масса	Масштаб
Изм.	Лист	№ докум	Подп.	Дата		1:2
Разраб	Суборов ДС					
Град	Гузюнова					
Т.контр.						
Н.контр.						
Этб						
К 10.00Н				Лист	Листов	1
Сборочный чертеж				11-519-3		
Копирован				Формат А3		