


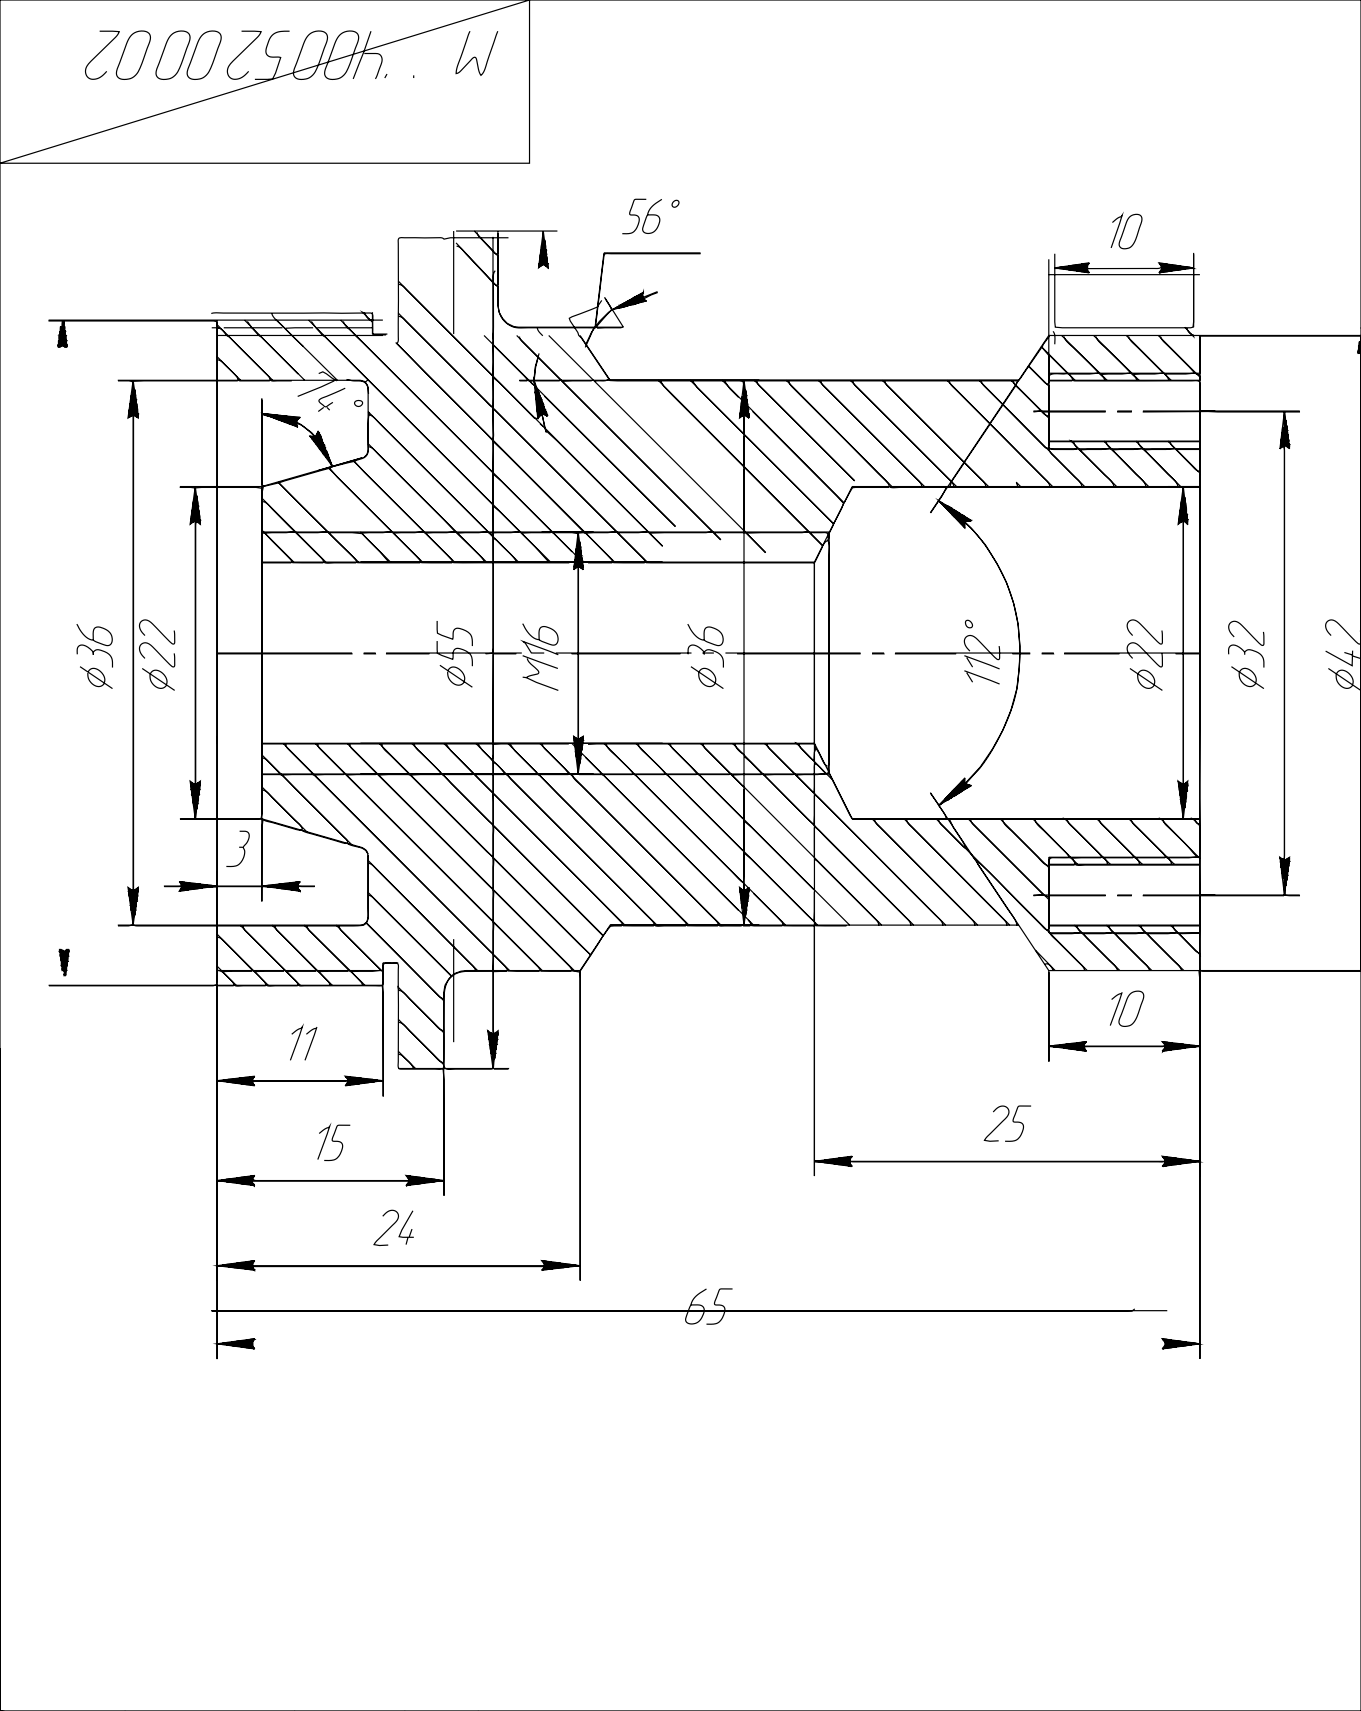

				M400520002		
				Крышка		
Изм	Лист	№ докум	Подп	Дата	Лист	Масса
Разраб	Суваров					21
Пров	Лизанова					
Т контр					Лист	Листов 1
И контр					ЛТ-519-3	
Утв					СЧ15 ГОСТ 1412-79	