
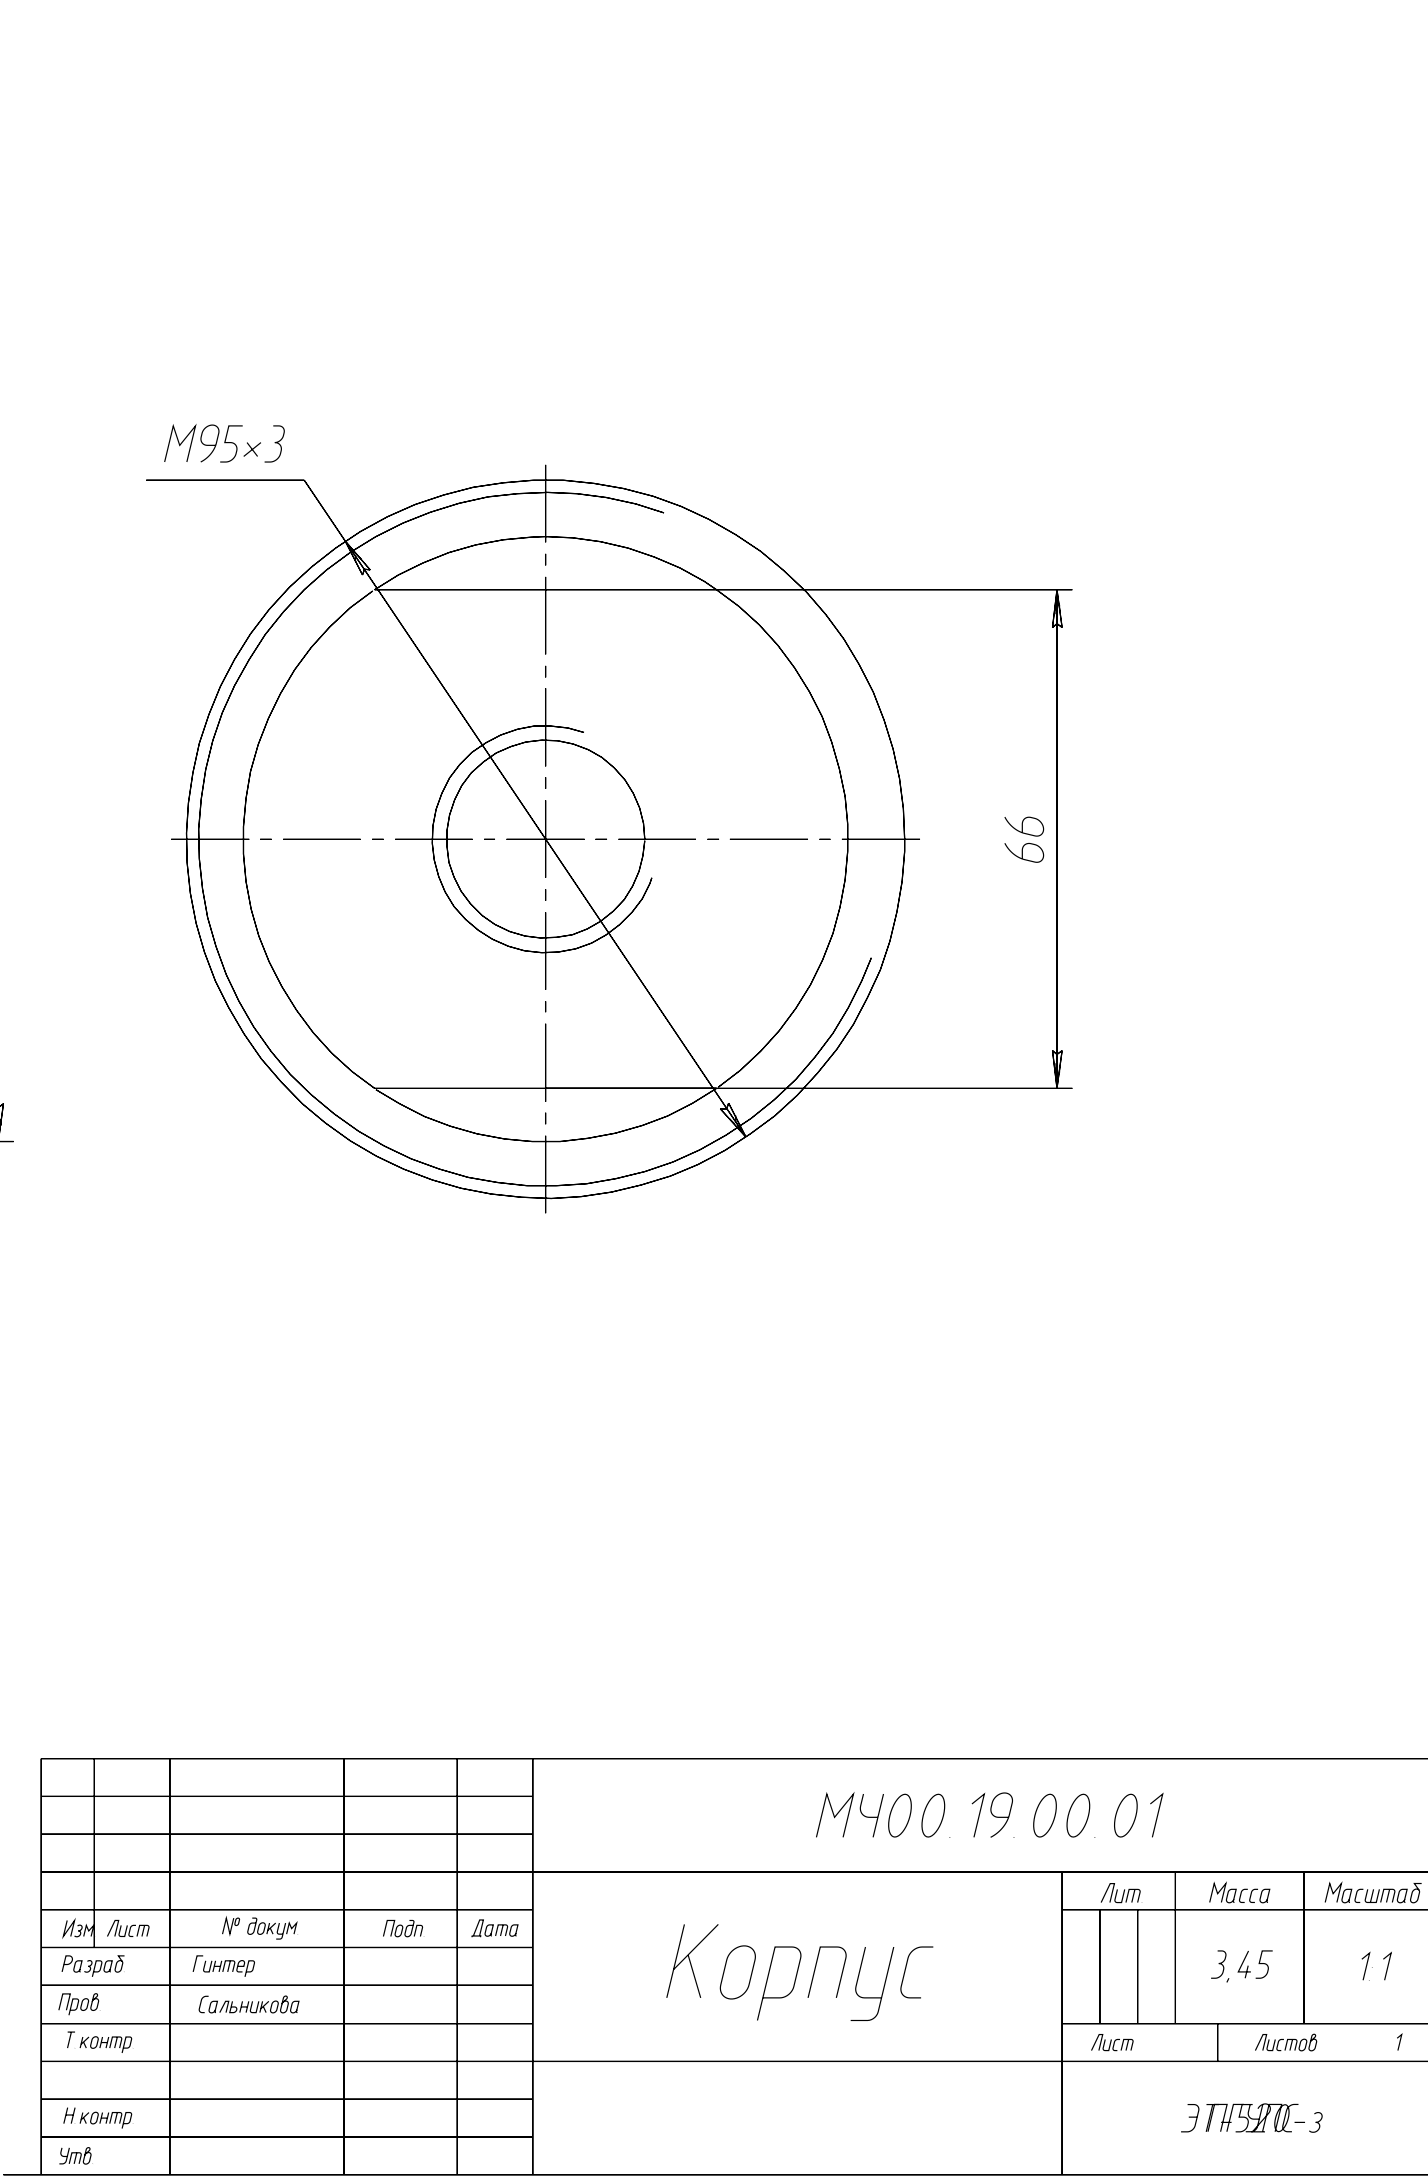


10 00 61 00HW

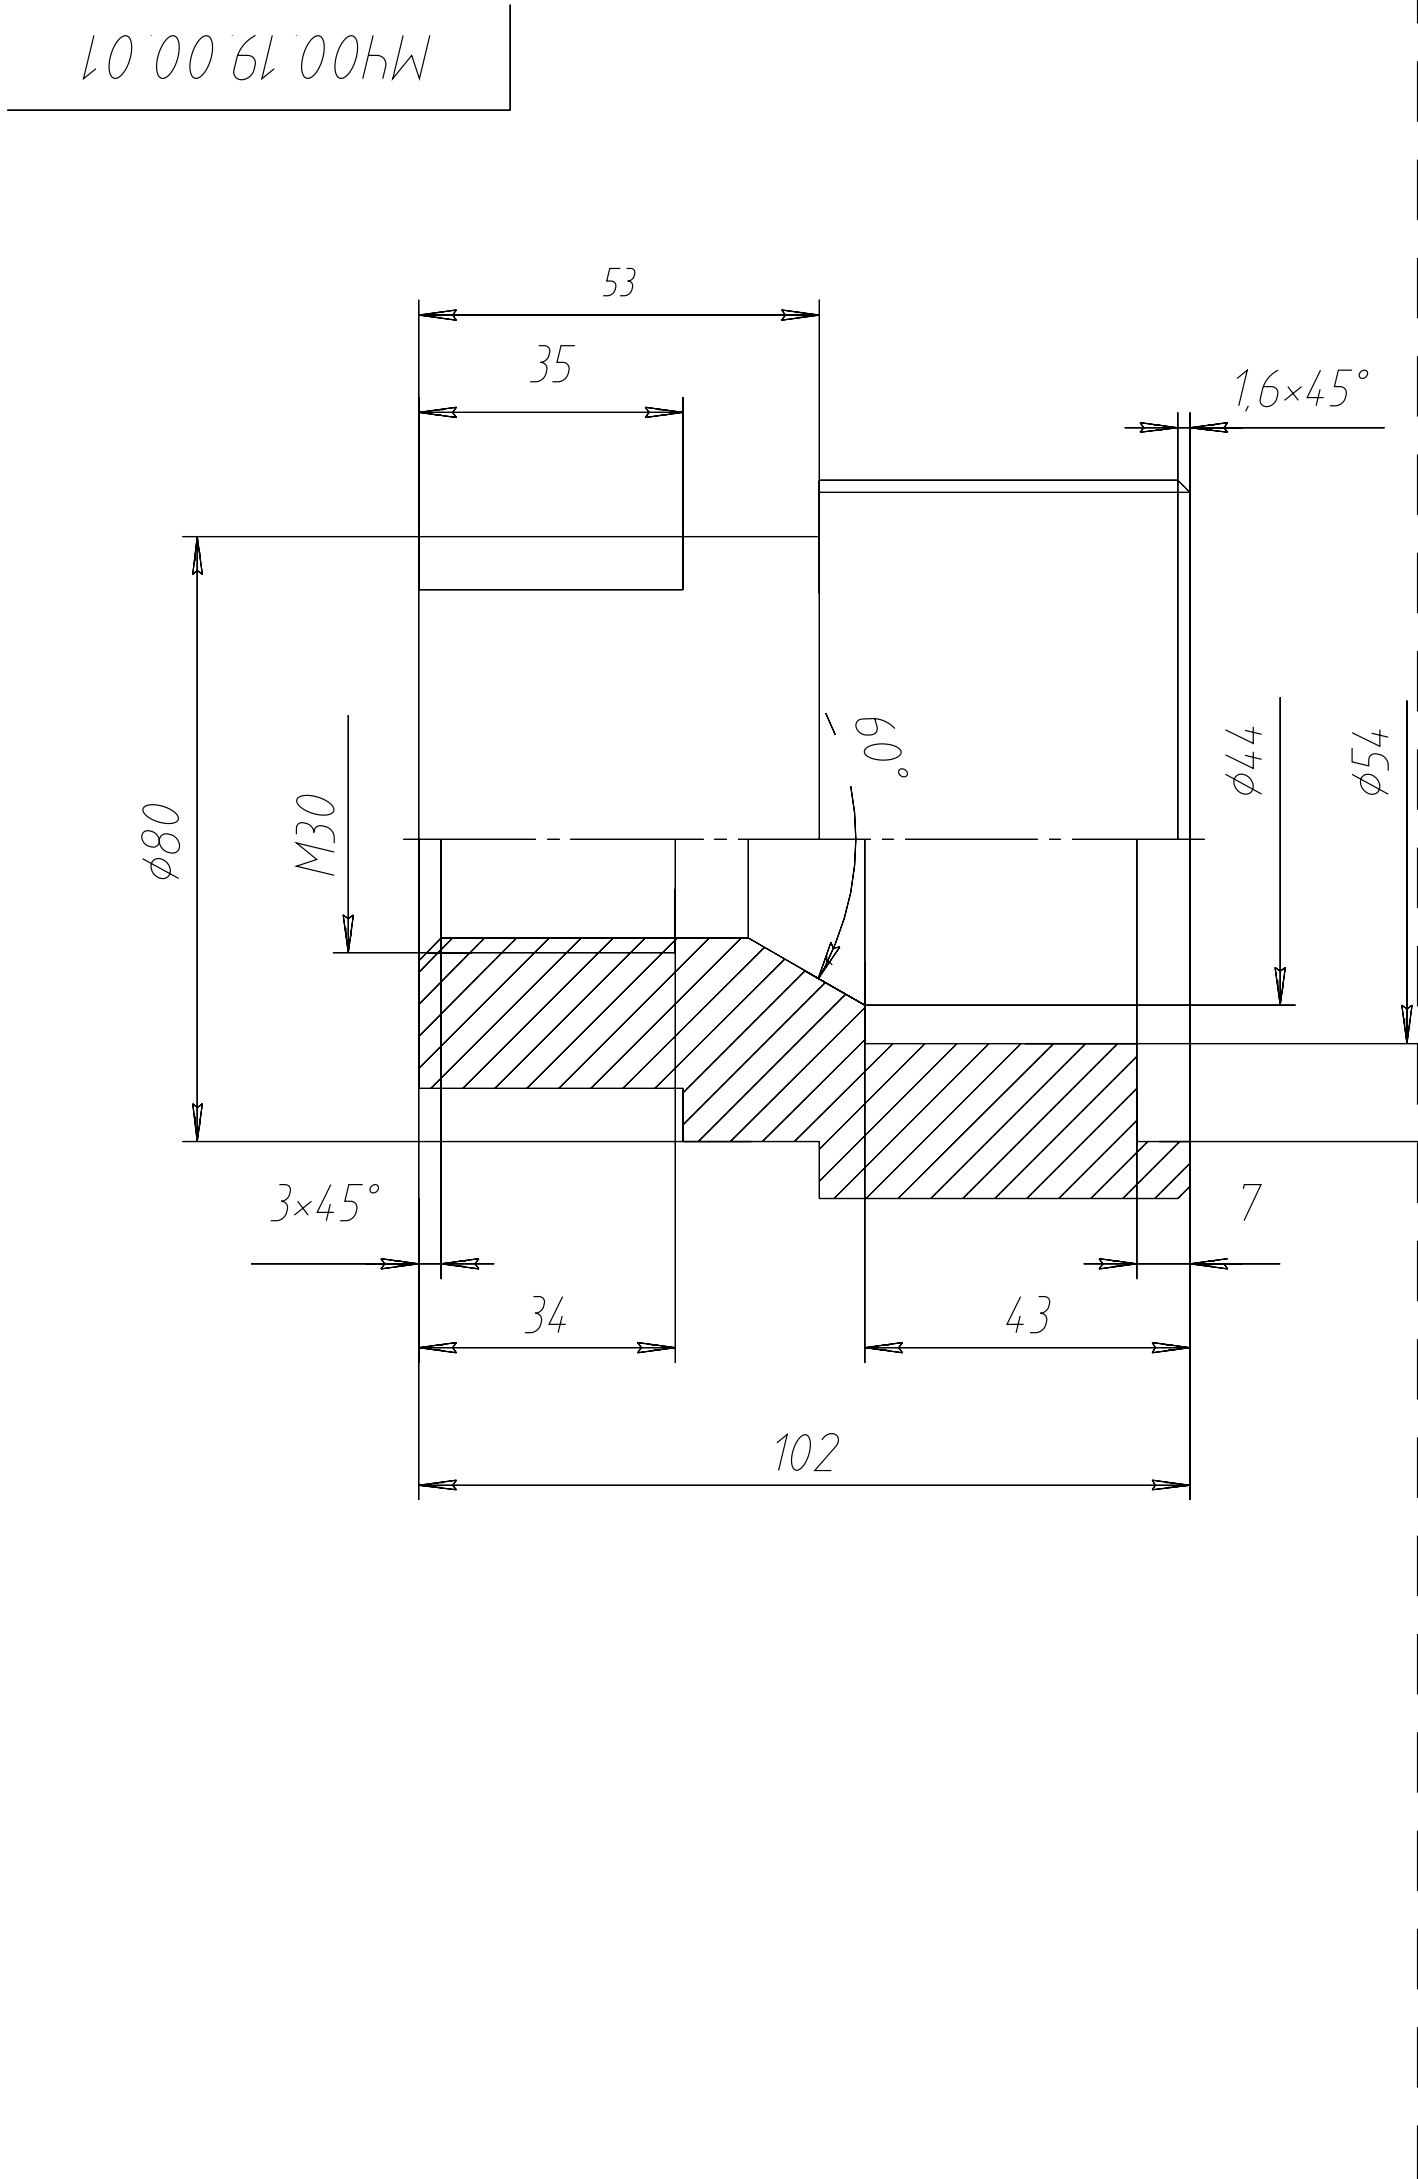

					М400 19 00 01								
					Корпус				Лист		Масса	Масштаб	
Изм	Лист	№ докум	Подп	Дата								3,45	1:1
Разраб		Гинтер											
Пров		Сальникова											
Т контр													
									Лист		Листов	1	
									ЭТН-3				
Н контр													
Утв													