
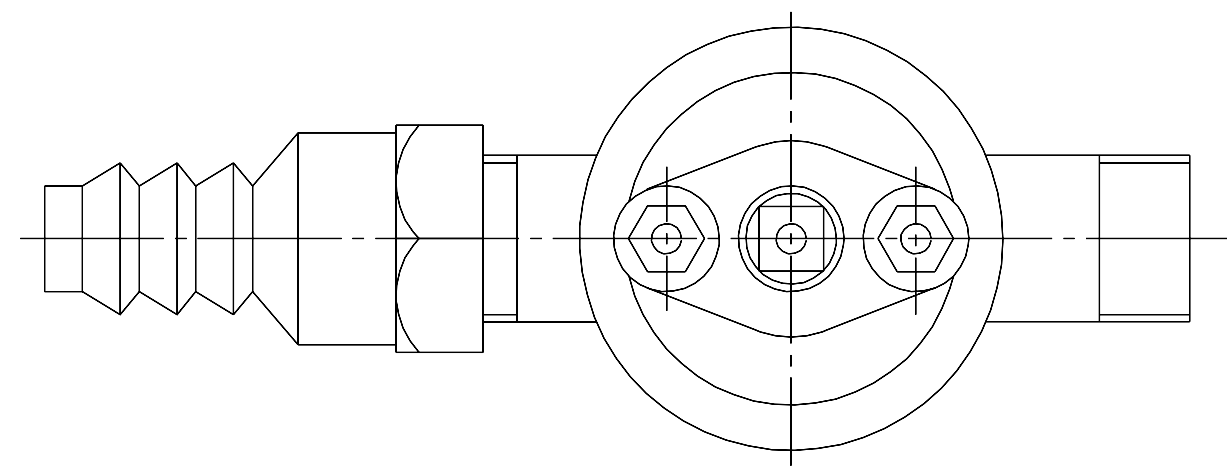
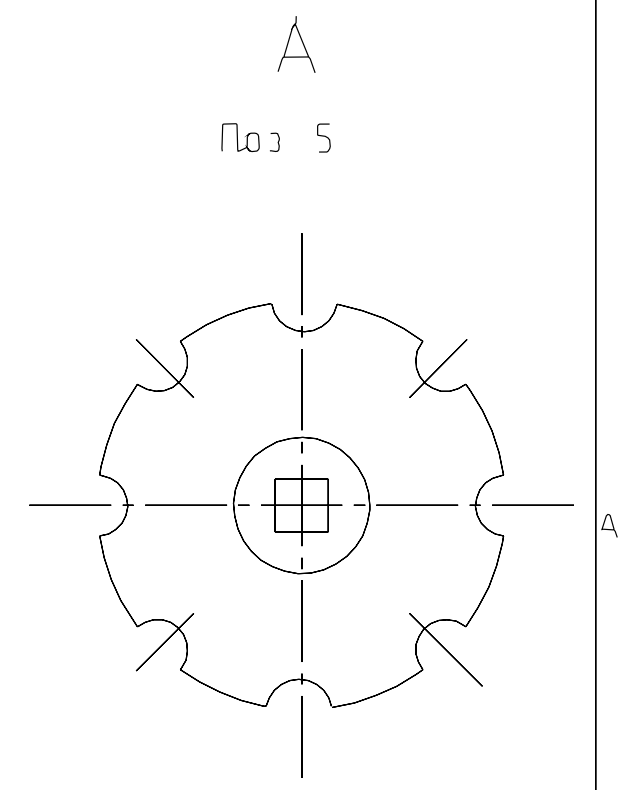
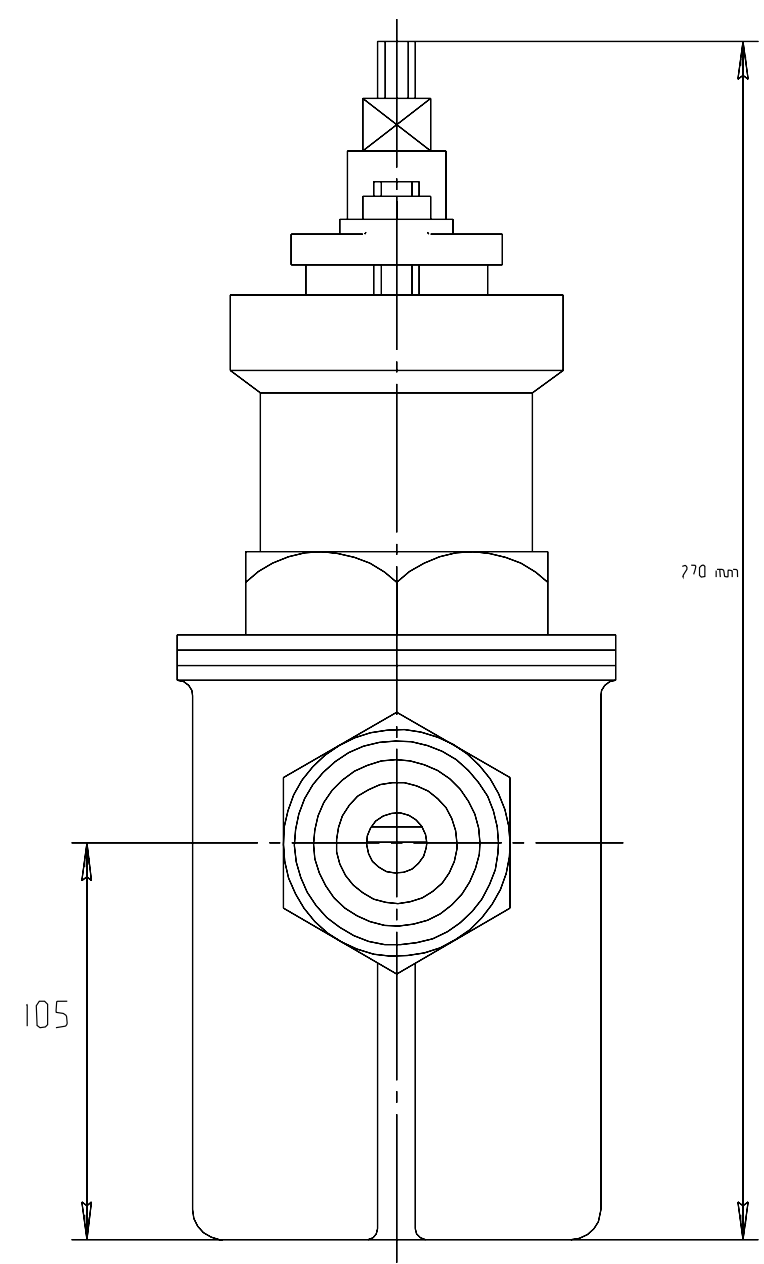


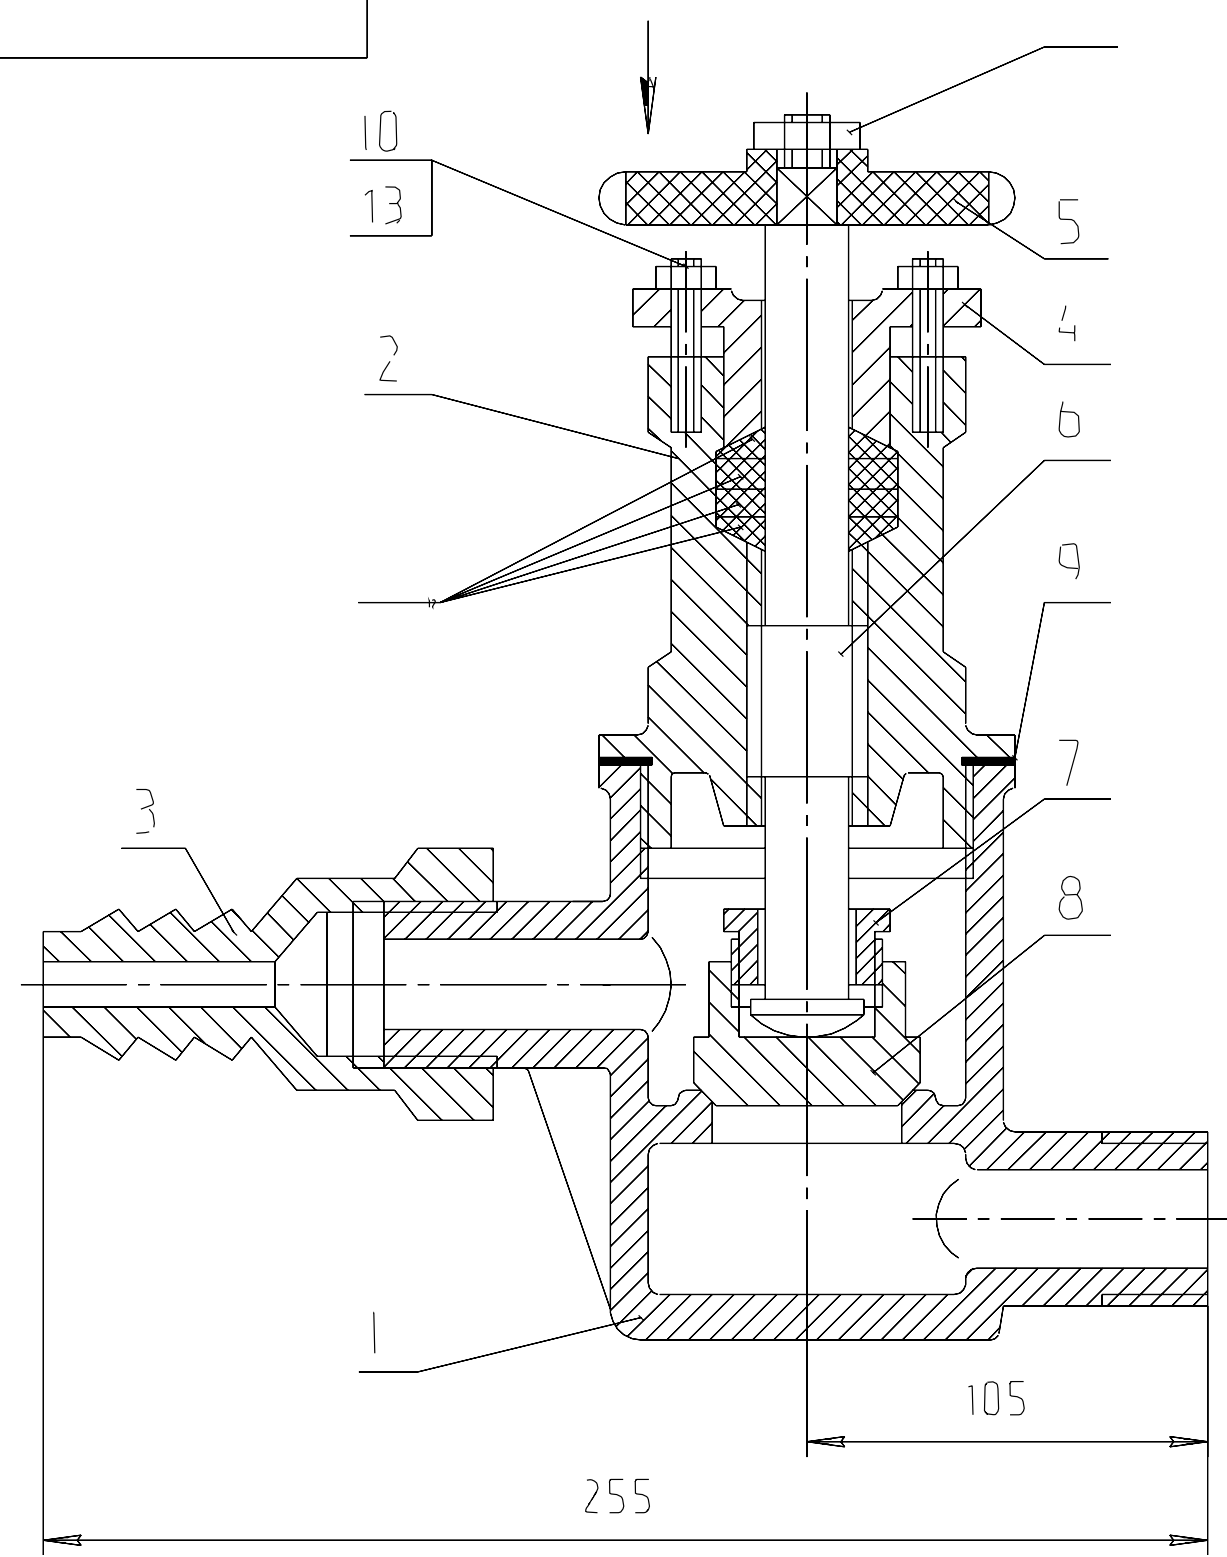

					М400 52 00 00 СД			
Изм	Лист	№ докум	Подп	Дата	Клапан Сборочный чертеж	Лист	Масса	Масштаб
Разраб	Судоров А С							12
Пров	Лузанова							
Т.контр						Лист	Листов	1
Н.контр								
УЛВ								
						АТ-519-3		