
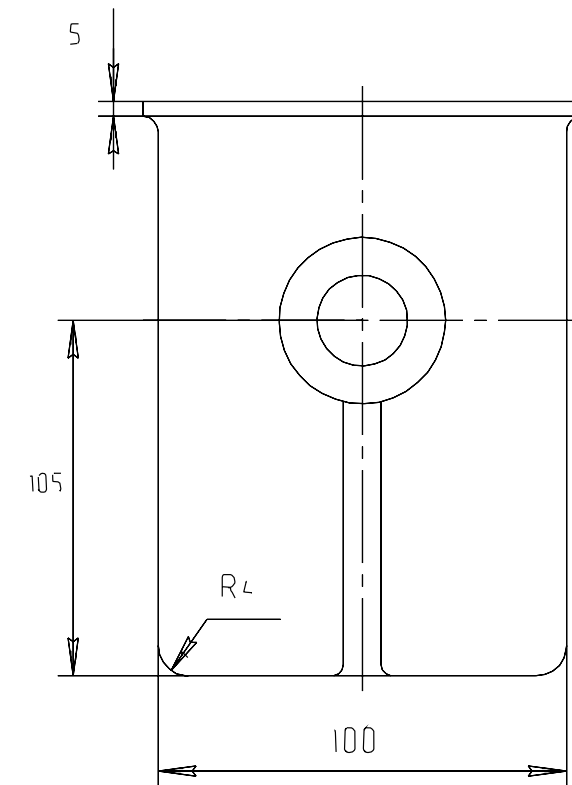


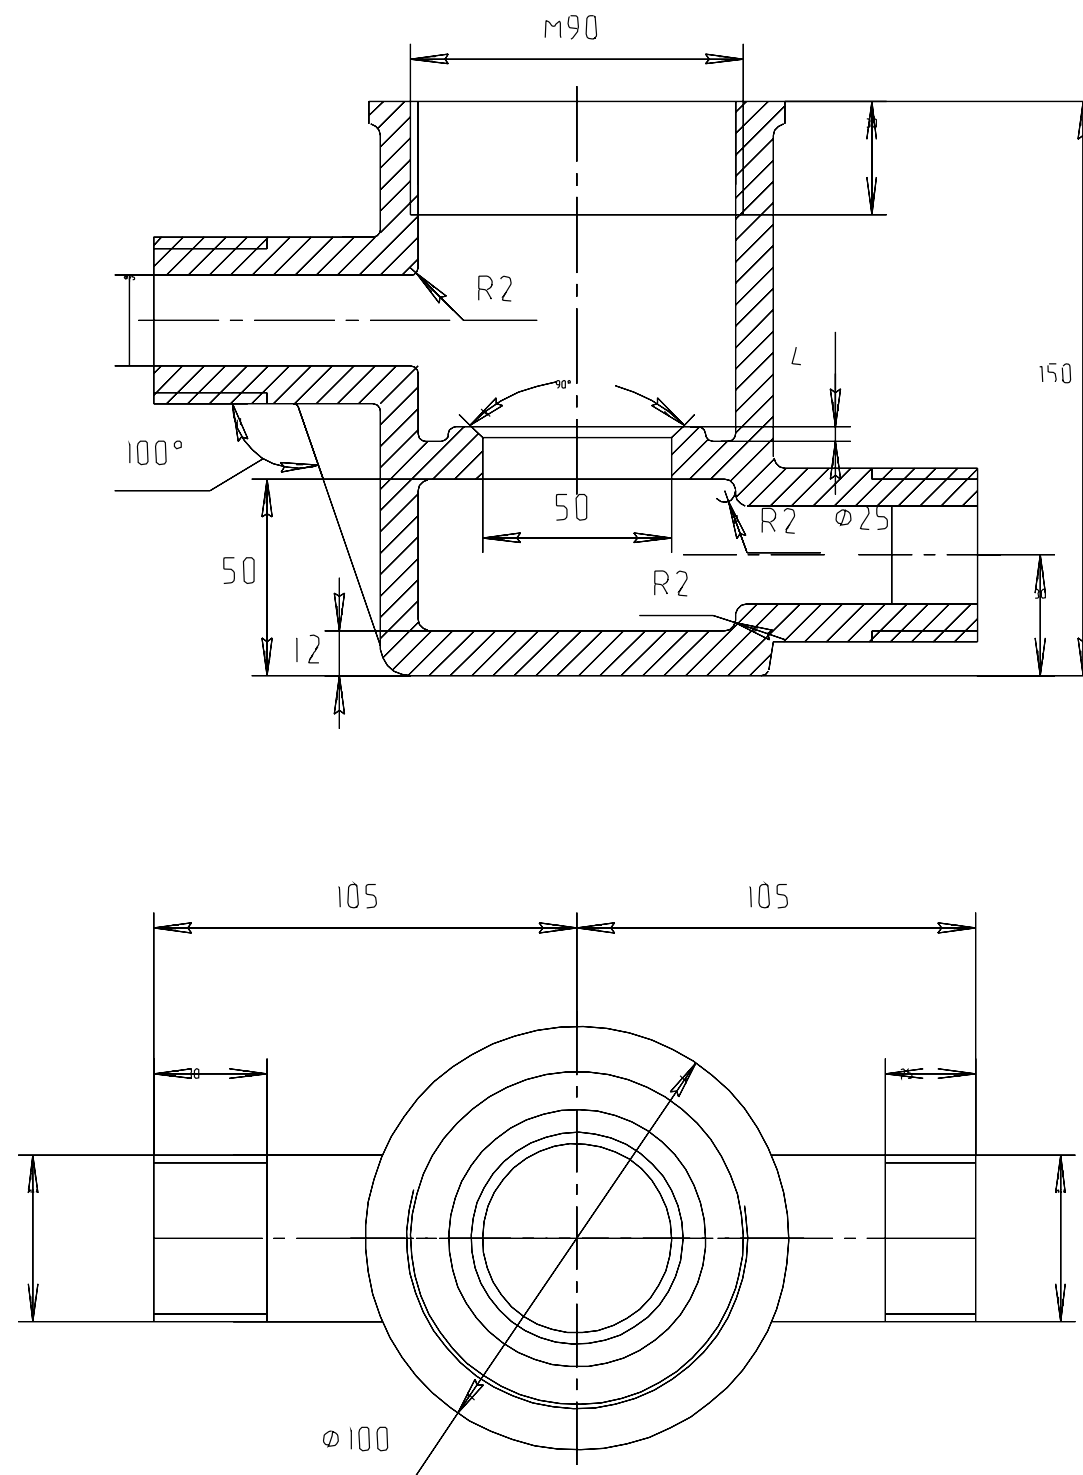

					М400 52 00 01				
					КОРПУС	ЛИСТ		МАССА	МАСШТАБ
Изм	Лист	№ докум	Подп	Дата					12
Разраб		Судоров ДС							
Пров		Лузанова							
Т.контр						Лист		Листов	1
Н.контр					СЧ 15 ГОСТ 1412-79	АТ-519-3			
УЛВ									