
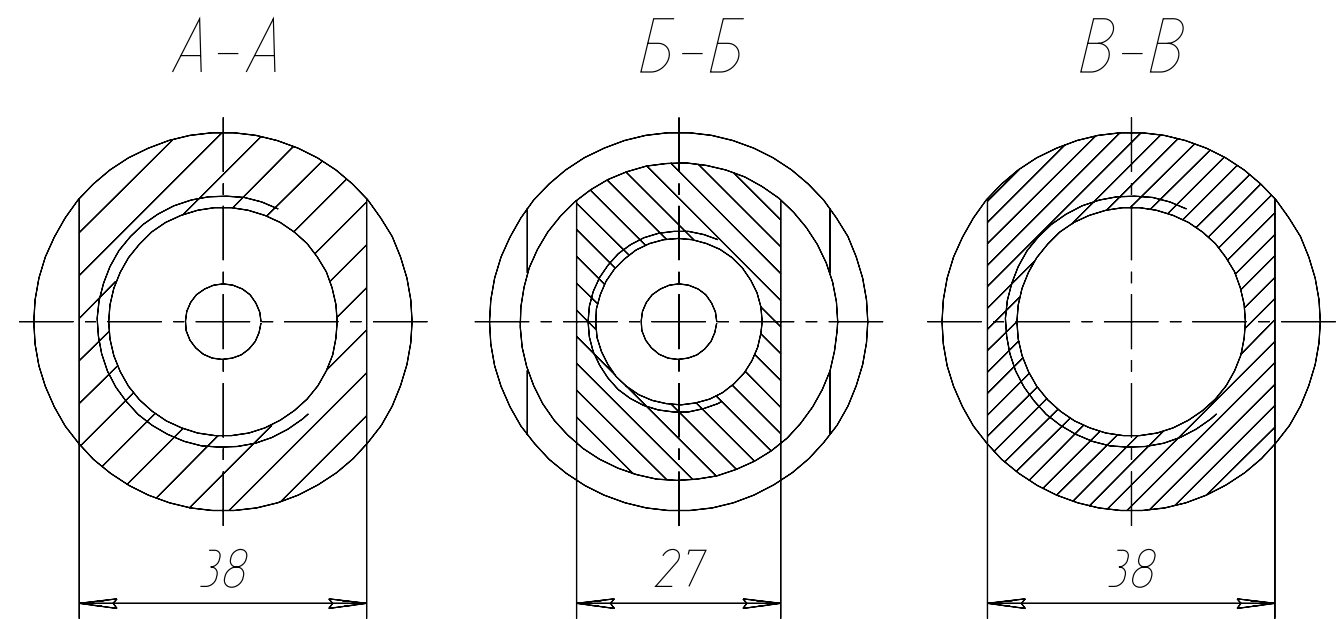


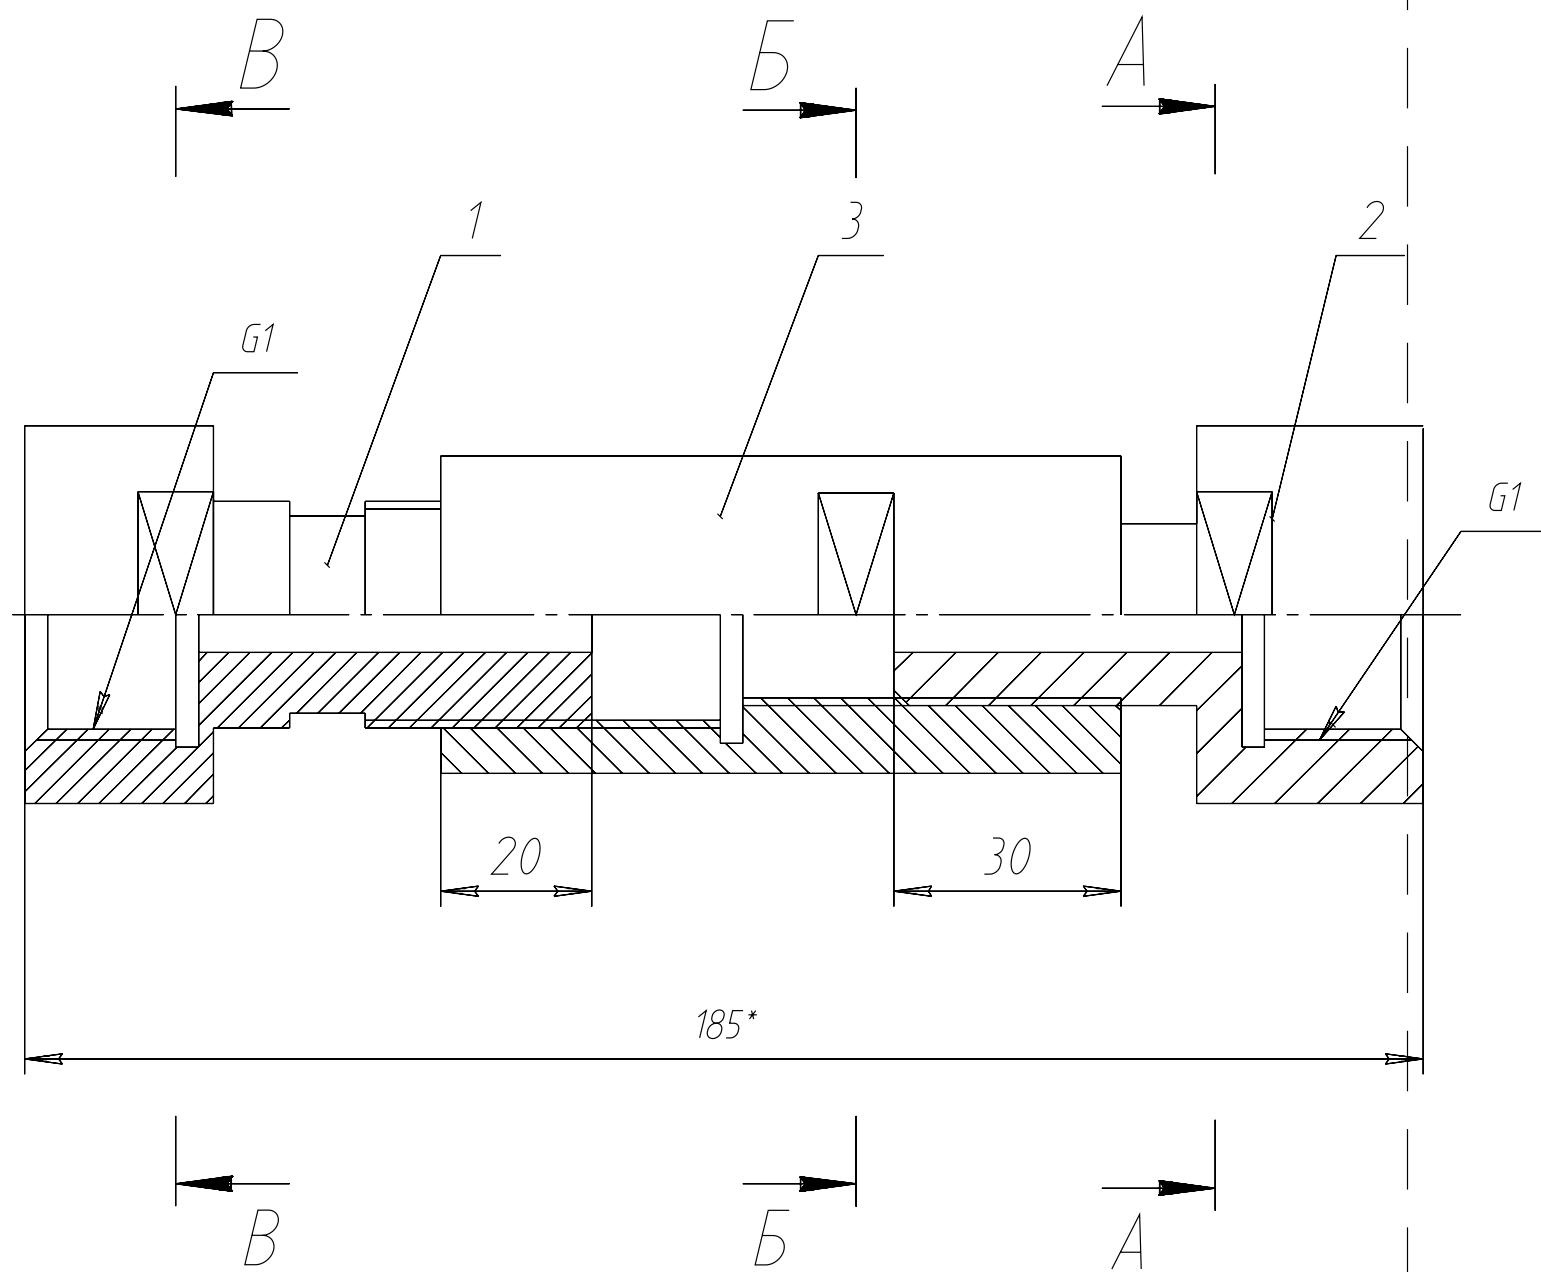

*Размер для справок

					КНГ 03 03 00 СБ			
					Узел Сборочный чертеж	Лист	Масса	Масштаб
Изм	Лист	№ докум	Подп	Дата				11
Разраб		Дорохов						
Пров		Пузанова						
Т контр						Лист	Листов	1
Н контр						ПГУПС		
Утв						ЛТ-519-3		